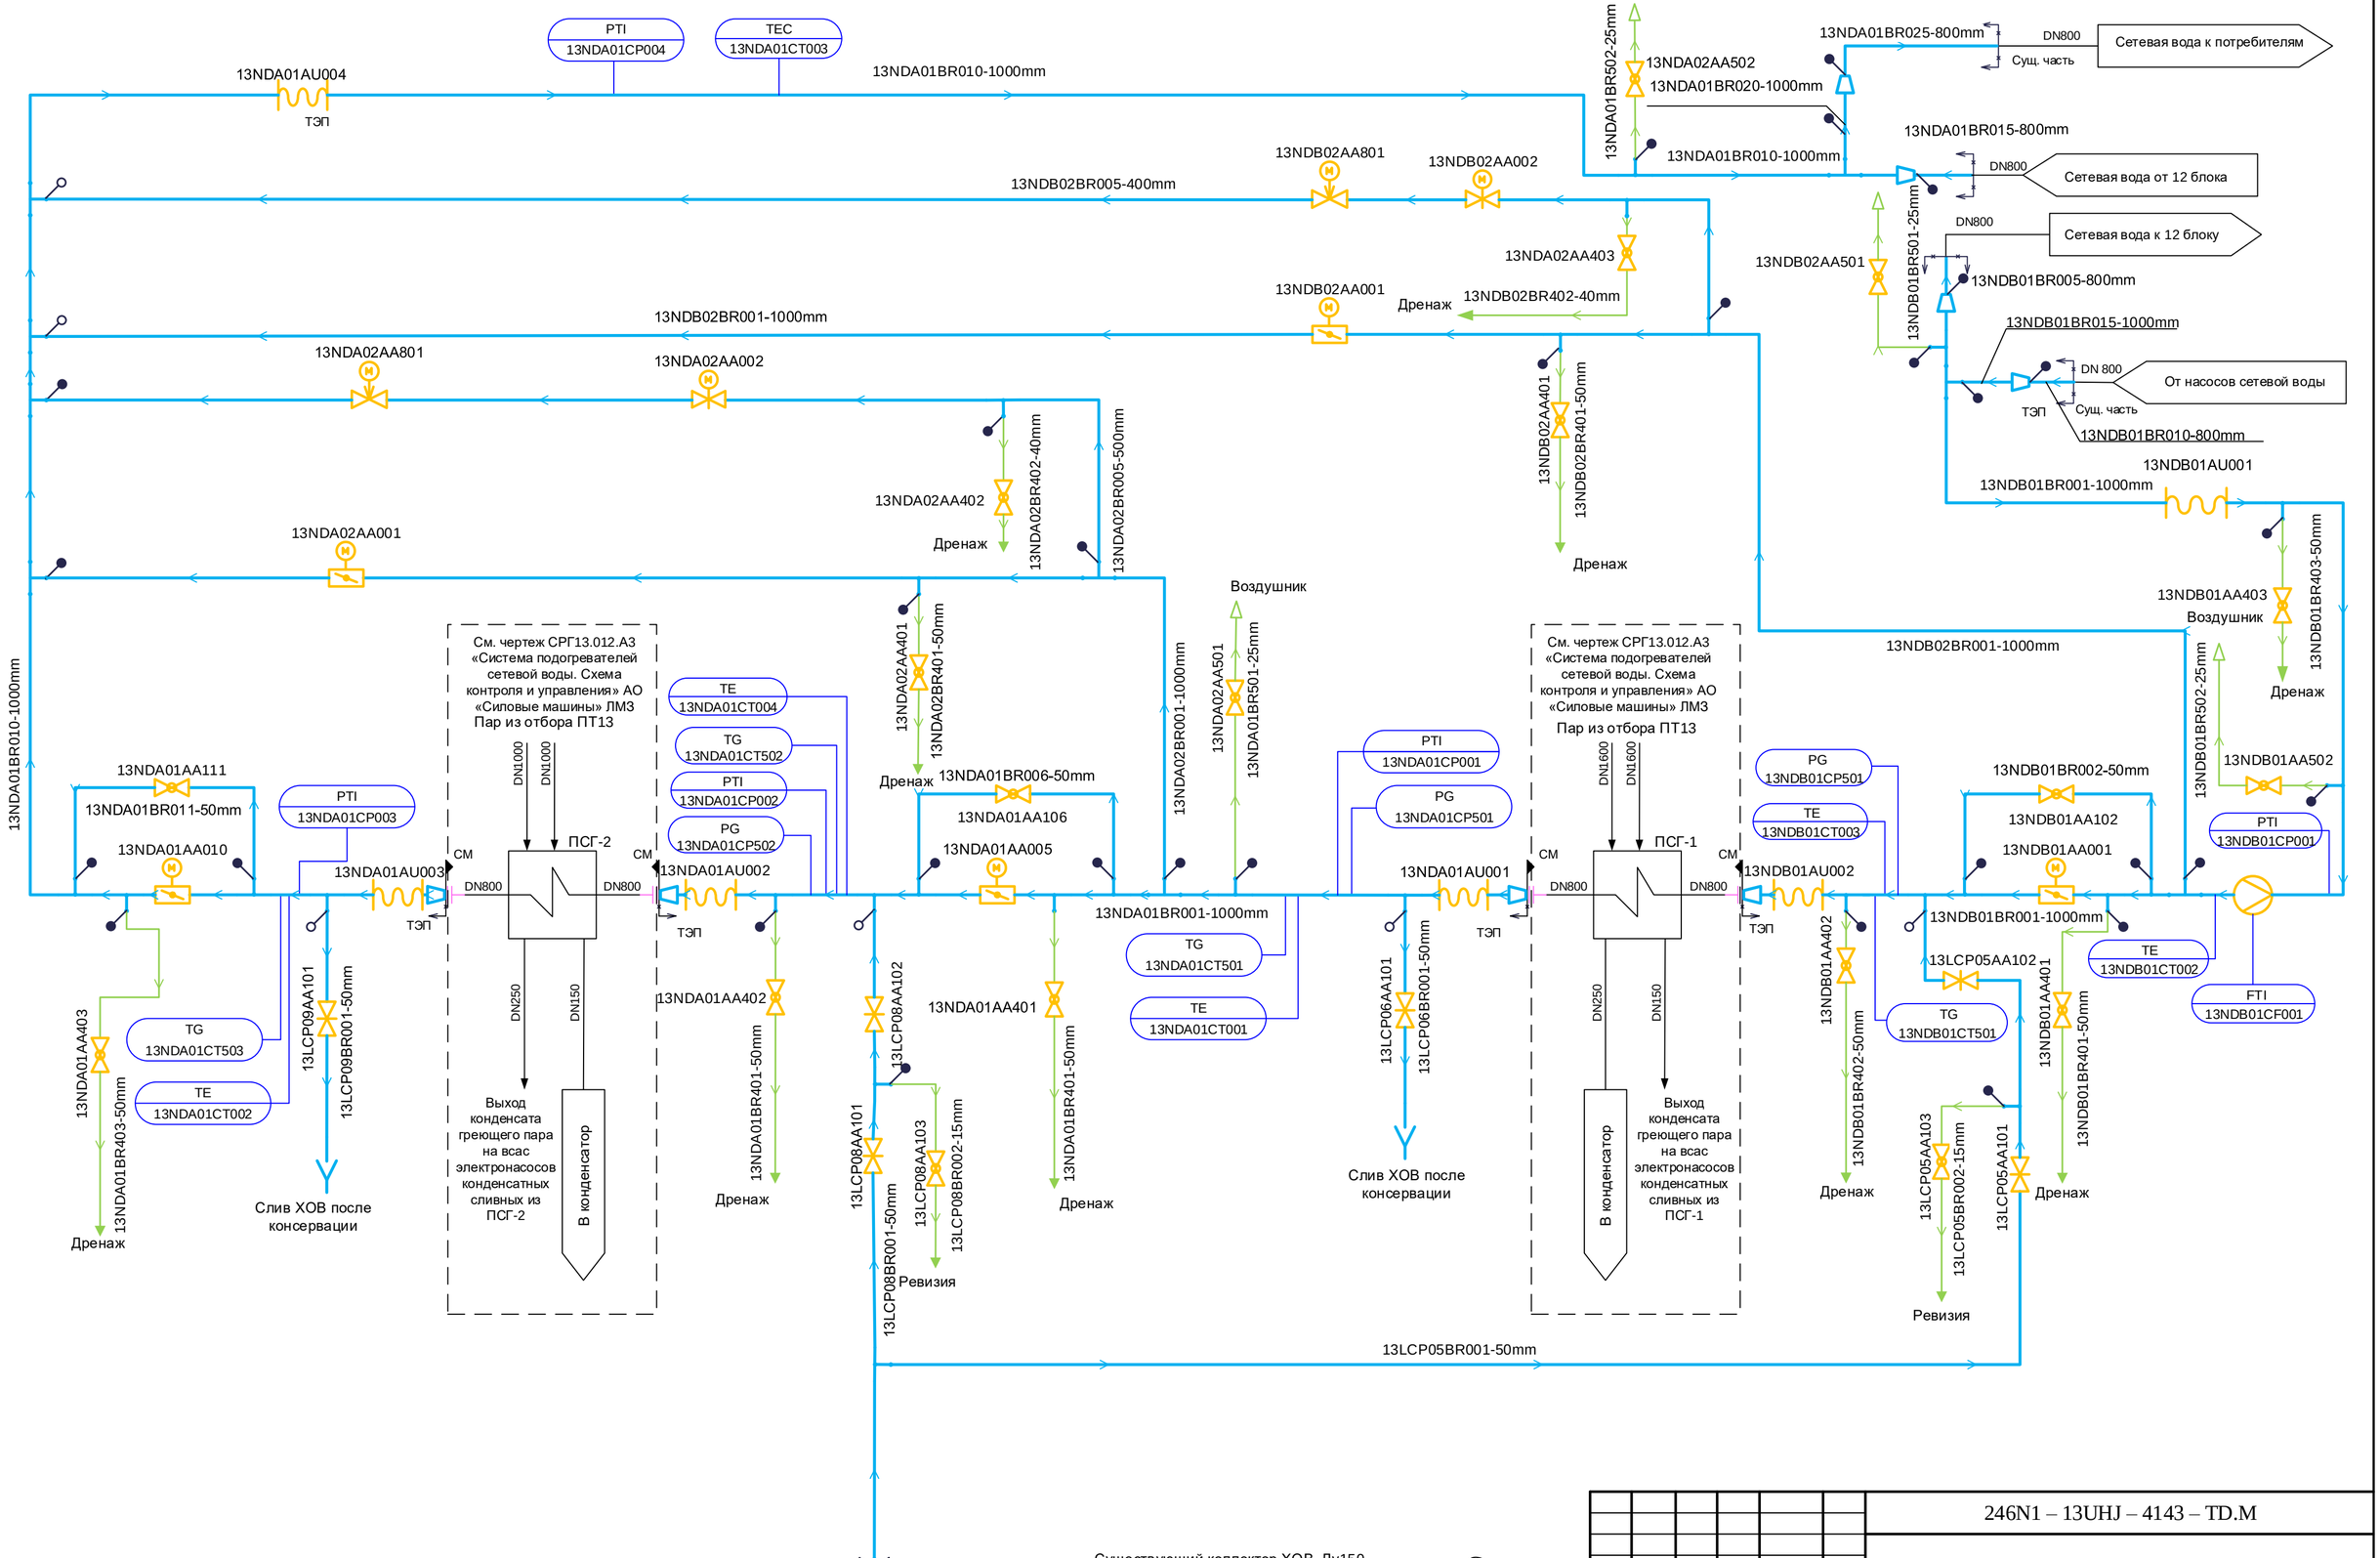

3	-	Зам.	1351-23		08.2023	246N1 – 13UHJ – 4143 – TD.M
Изм.	Кол.уч	Лист	№ док.	Подп.	Дата	Модернизация генерирующего объекта Сургутская ГРЭС-1 (13Г)
Разработал		Яковлева			08.2023	Главный корпус. PI-диаграмма трубопроводов сетевой воды
Проверил		Сладков			08.2023	Стадия: Р; Лист: 2; Листов:
Н. контр.		Астраханцев			08.2023	PI-диаграмма трубопроводов сетевой воды. Системы NDA, NDB

АКЦИОНЕРНОЕ ОБЩЕСТВО ИНСТИТУТ ТЕПЛОЭЛЕКТРОПРОЕКТ Г. МОСКВА

Согласовано
ОАСУ Соболева

Подпись и дата

Инв. № подл.

Формат А2