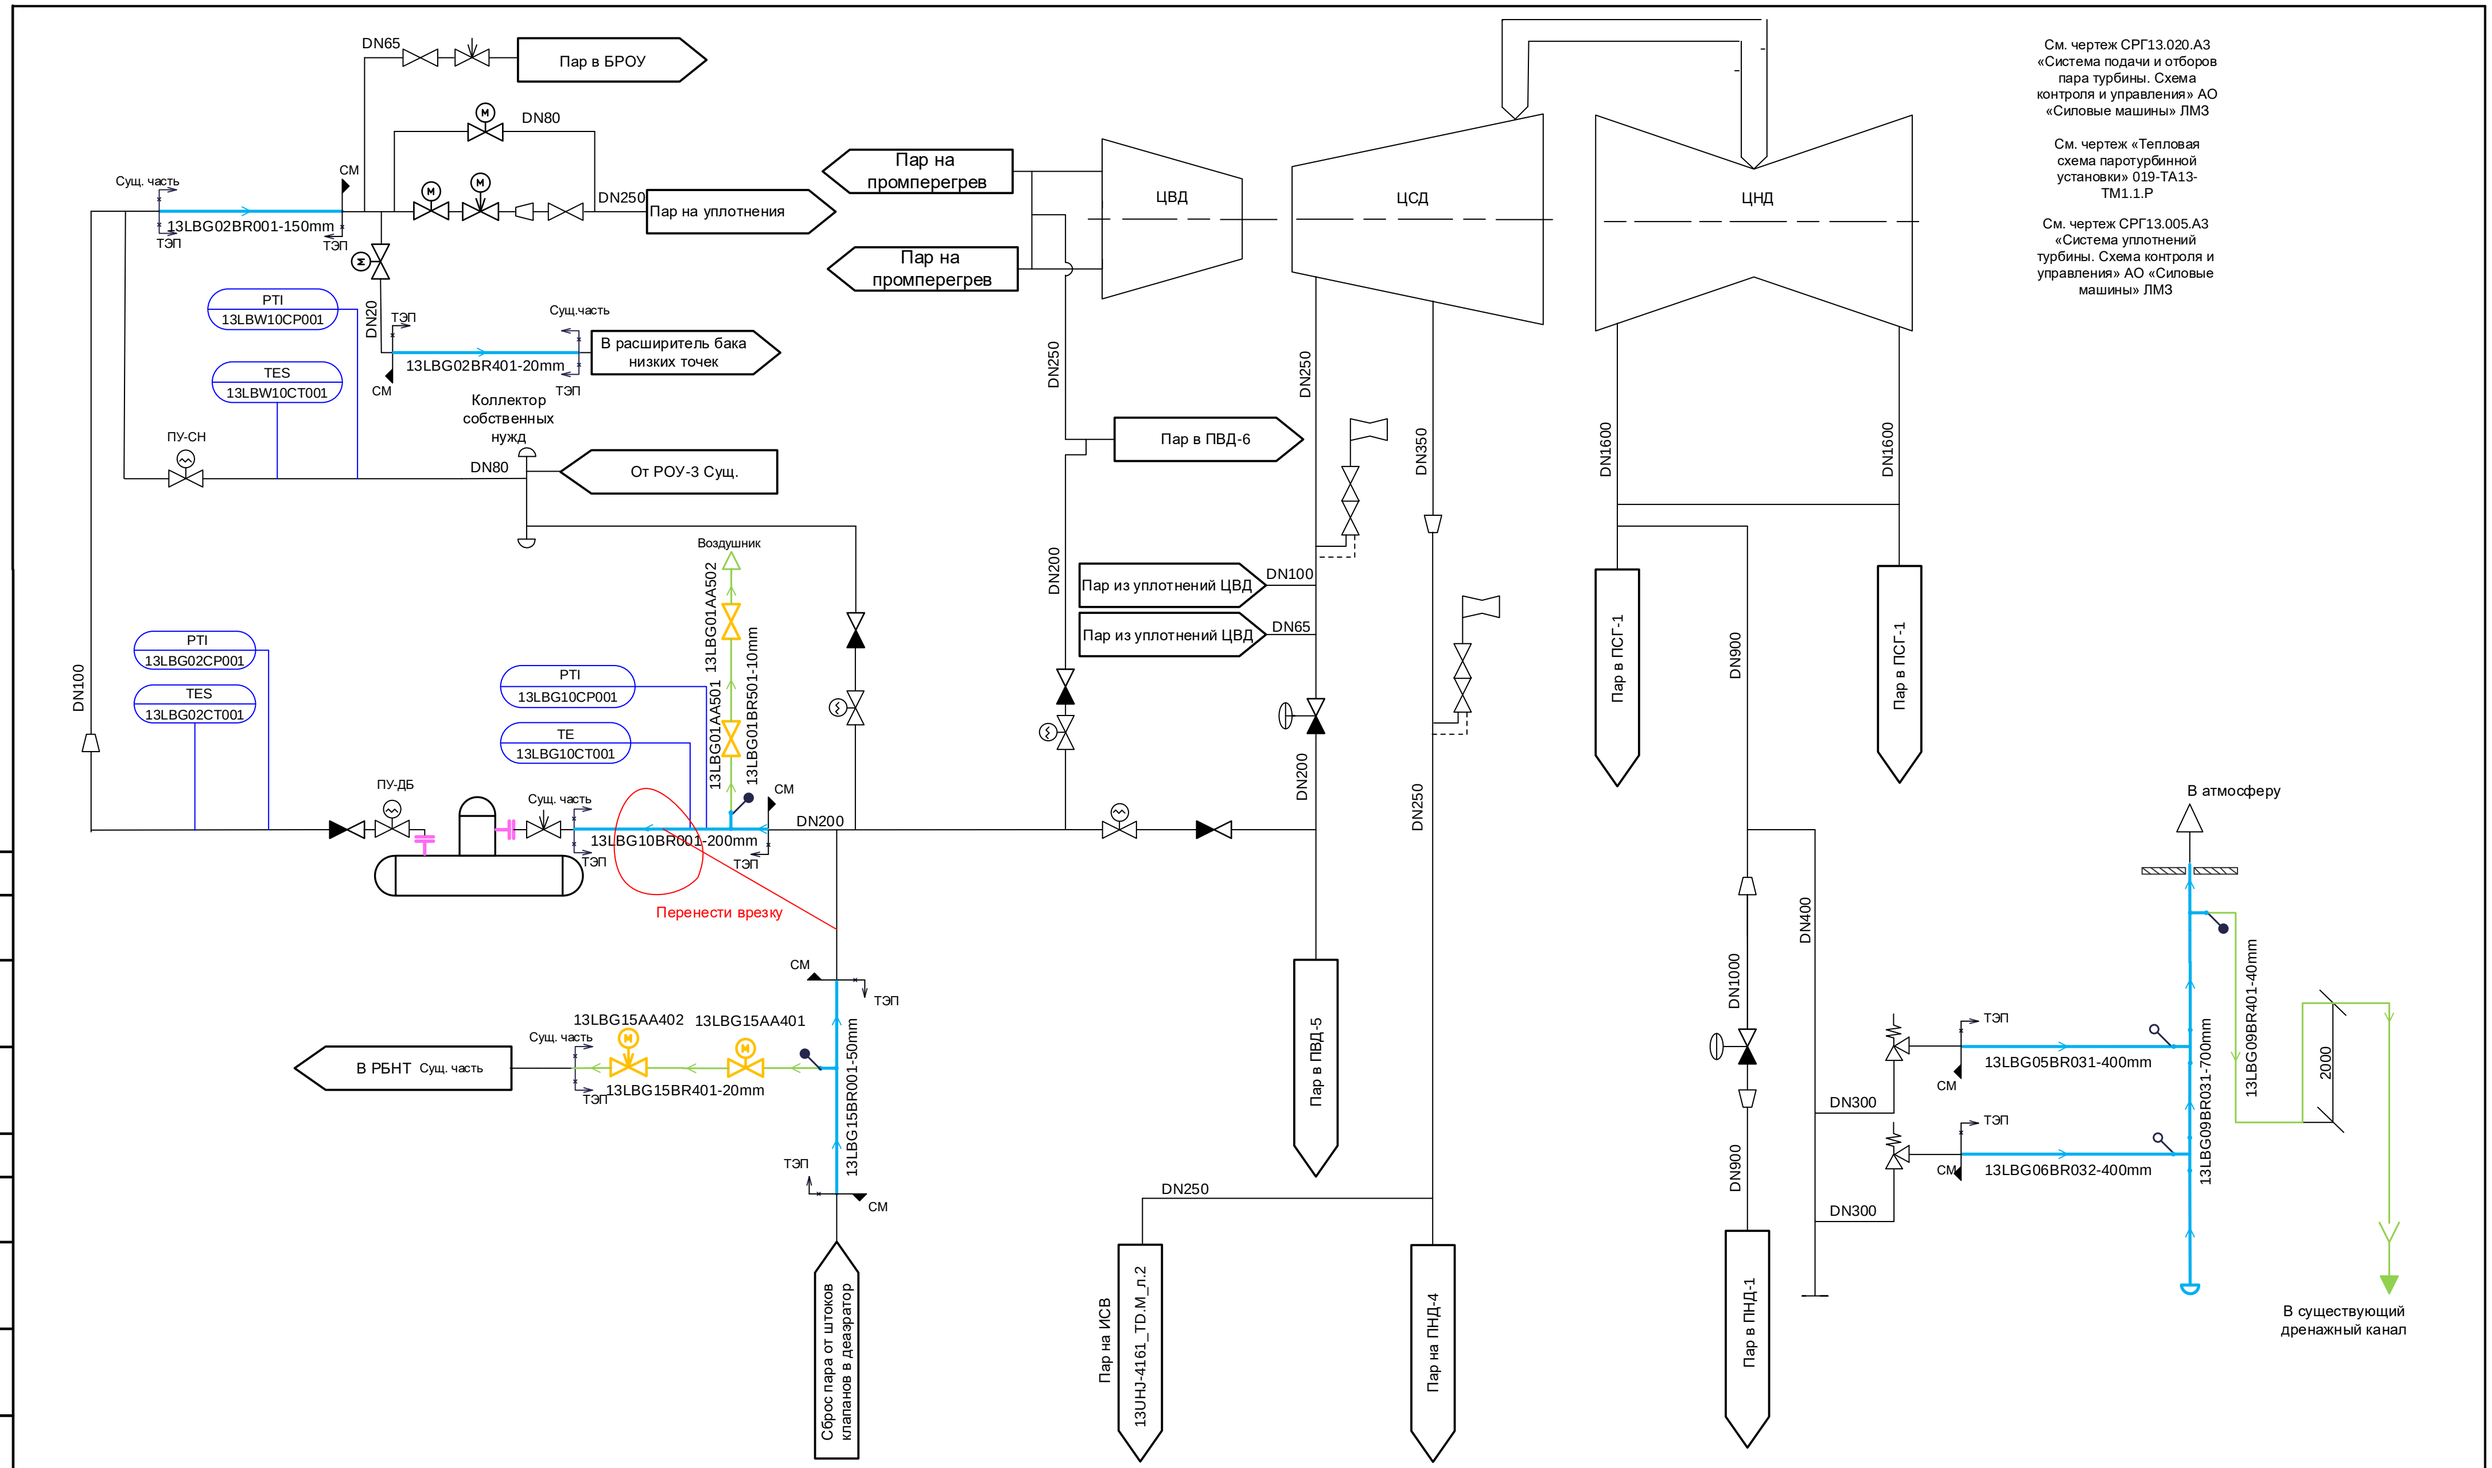

См. чертеж СРГ13.020.А3 «Система подачи и отборов пара турбины. Схема контроля и управления» АО «Силовые машины» ЛМЗ

См. чертеж «Тепловая схема паротурбинной установки» 019-ТА13-ТМ1.1.Р

См. чертеж СРГ13.005.А3 «Система уплотнений турбины. Схема контроля и управления» АО «Силовые машины» ЛМЗ

Существующая часть Сургутской ГРЭС-1 — АО «Институт Теплоэлектропроект» (ТЭП) - граница проектирования

АО «Силовые Машины» (СМ) — АО «Институт Теплоэлектропроект» (ТЭП) - граница проектирования

Согласовано: ОАСУ Соболева

Взам. инв. № | Подпись и дата | Инв. № подл.

Изм.	Кол.уч	Лист	№ док.	Подп.	Дата
5	-	Зам.	63924		

246N1–13UHJ–4148–TD.M

Модернизация генерирующего объекта Сургутская ГРЭС-1 (13г)

Разработал	Гусев	Главный корпус. PI-диаграмма трубопроводов пара собственных нужд	Стадия: Р; Лист: 2; Листов:
Проверил	Демина		
Н. контр.	Черемушкина	PI-диаграмма трубопроводов пара собственных нужд. Система LBG.	АКЦИОНЕРНОЕ ОБЩЕСТВО ИНСТИТУТ ТЕПЛОЭЛЕКТРОПРОЕКТ Г. МОСКВА

Формат А2