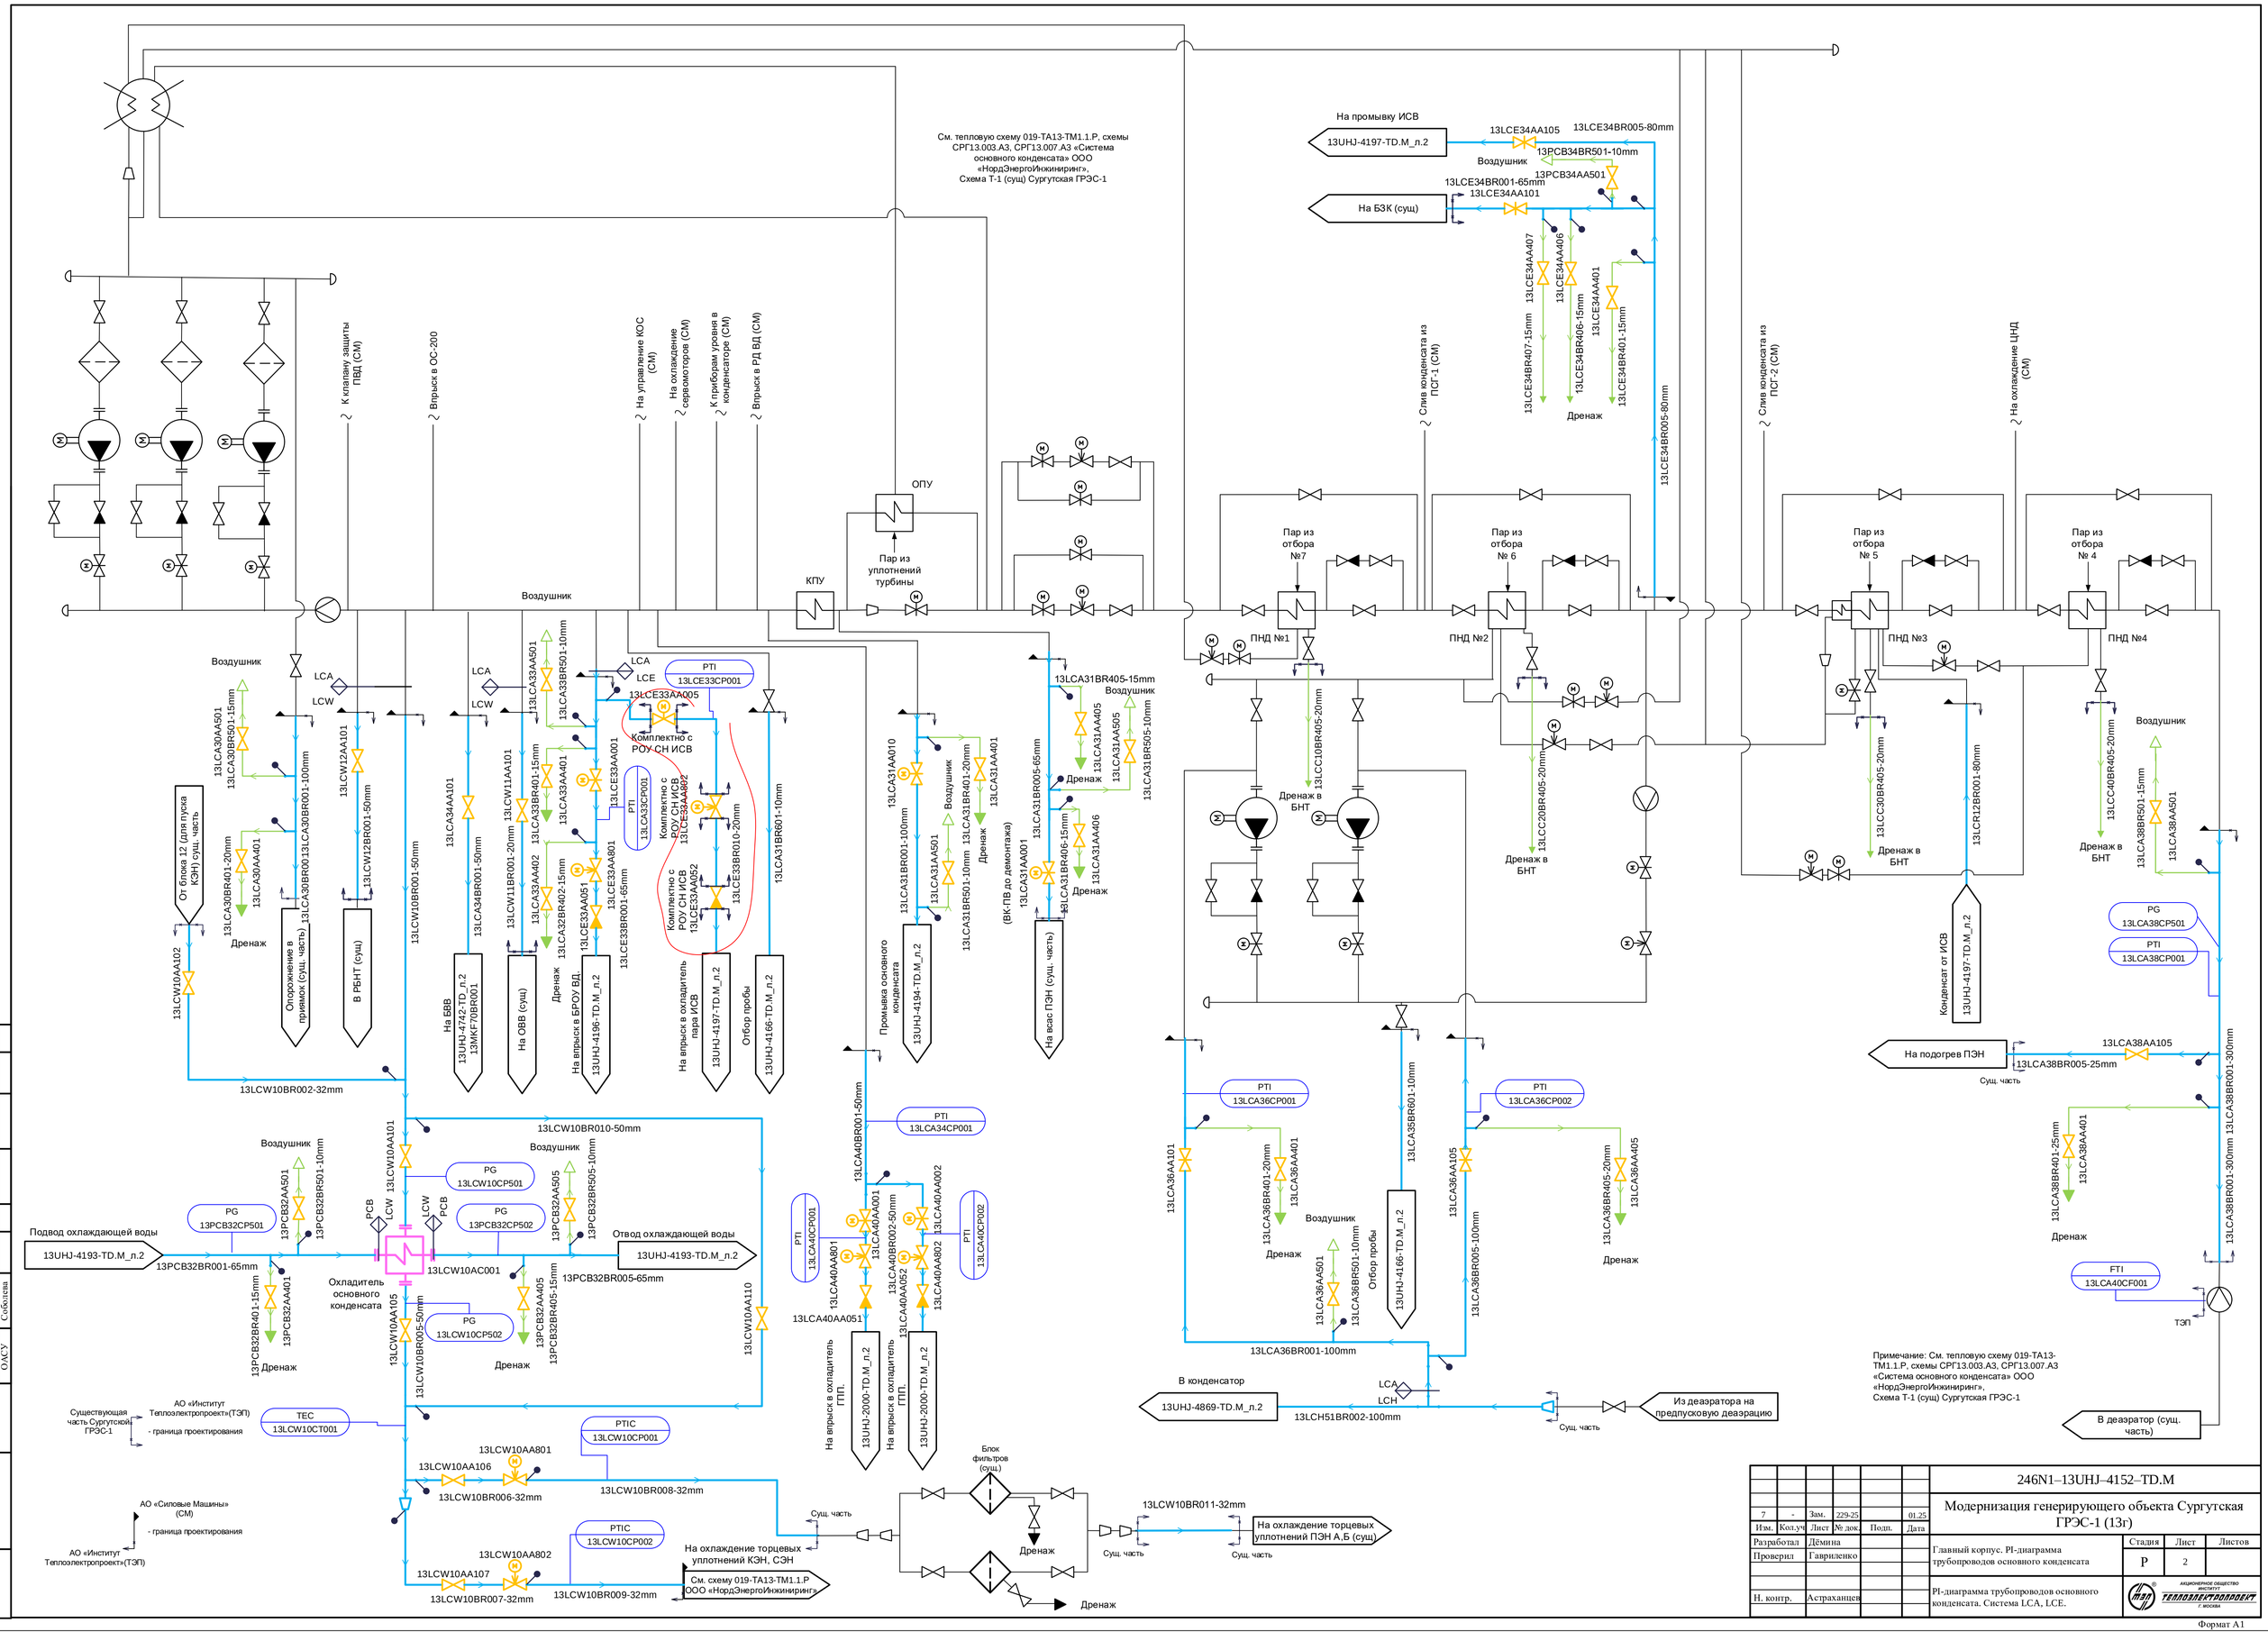

Изм.	Кол.уч	Лист	№ док.	Подп.	Дата
7	-	Зам.	229-25		01.25

246N1–13UHJ–4152–TD.M

Модернизация генерирующего объекта Сургутская ГРЭС-1 (13г)

Разработал	Дёмина	
Проверил	Гавриленко	
Н. контр.	Астраханцев	

Главный корпус. PI-диаграмма трубопроводов основного конденсата

PI-диаграмма трубопроводов основного конденсата. Система LCA, LCE.

Стадия	Лист	Листов
Р	2	

АКЦИОНЕРНОЕ ОБЩЕСТВО ИНСТИТУТ ТЕПЛОЭЛЕКТРОПРОЕКТ г. МОСКВА

Согласовано

ОАСУ Соболева

Взам. инв. №

Подпись и дата

Инв. № подл.

Формат А1