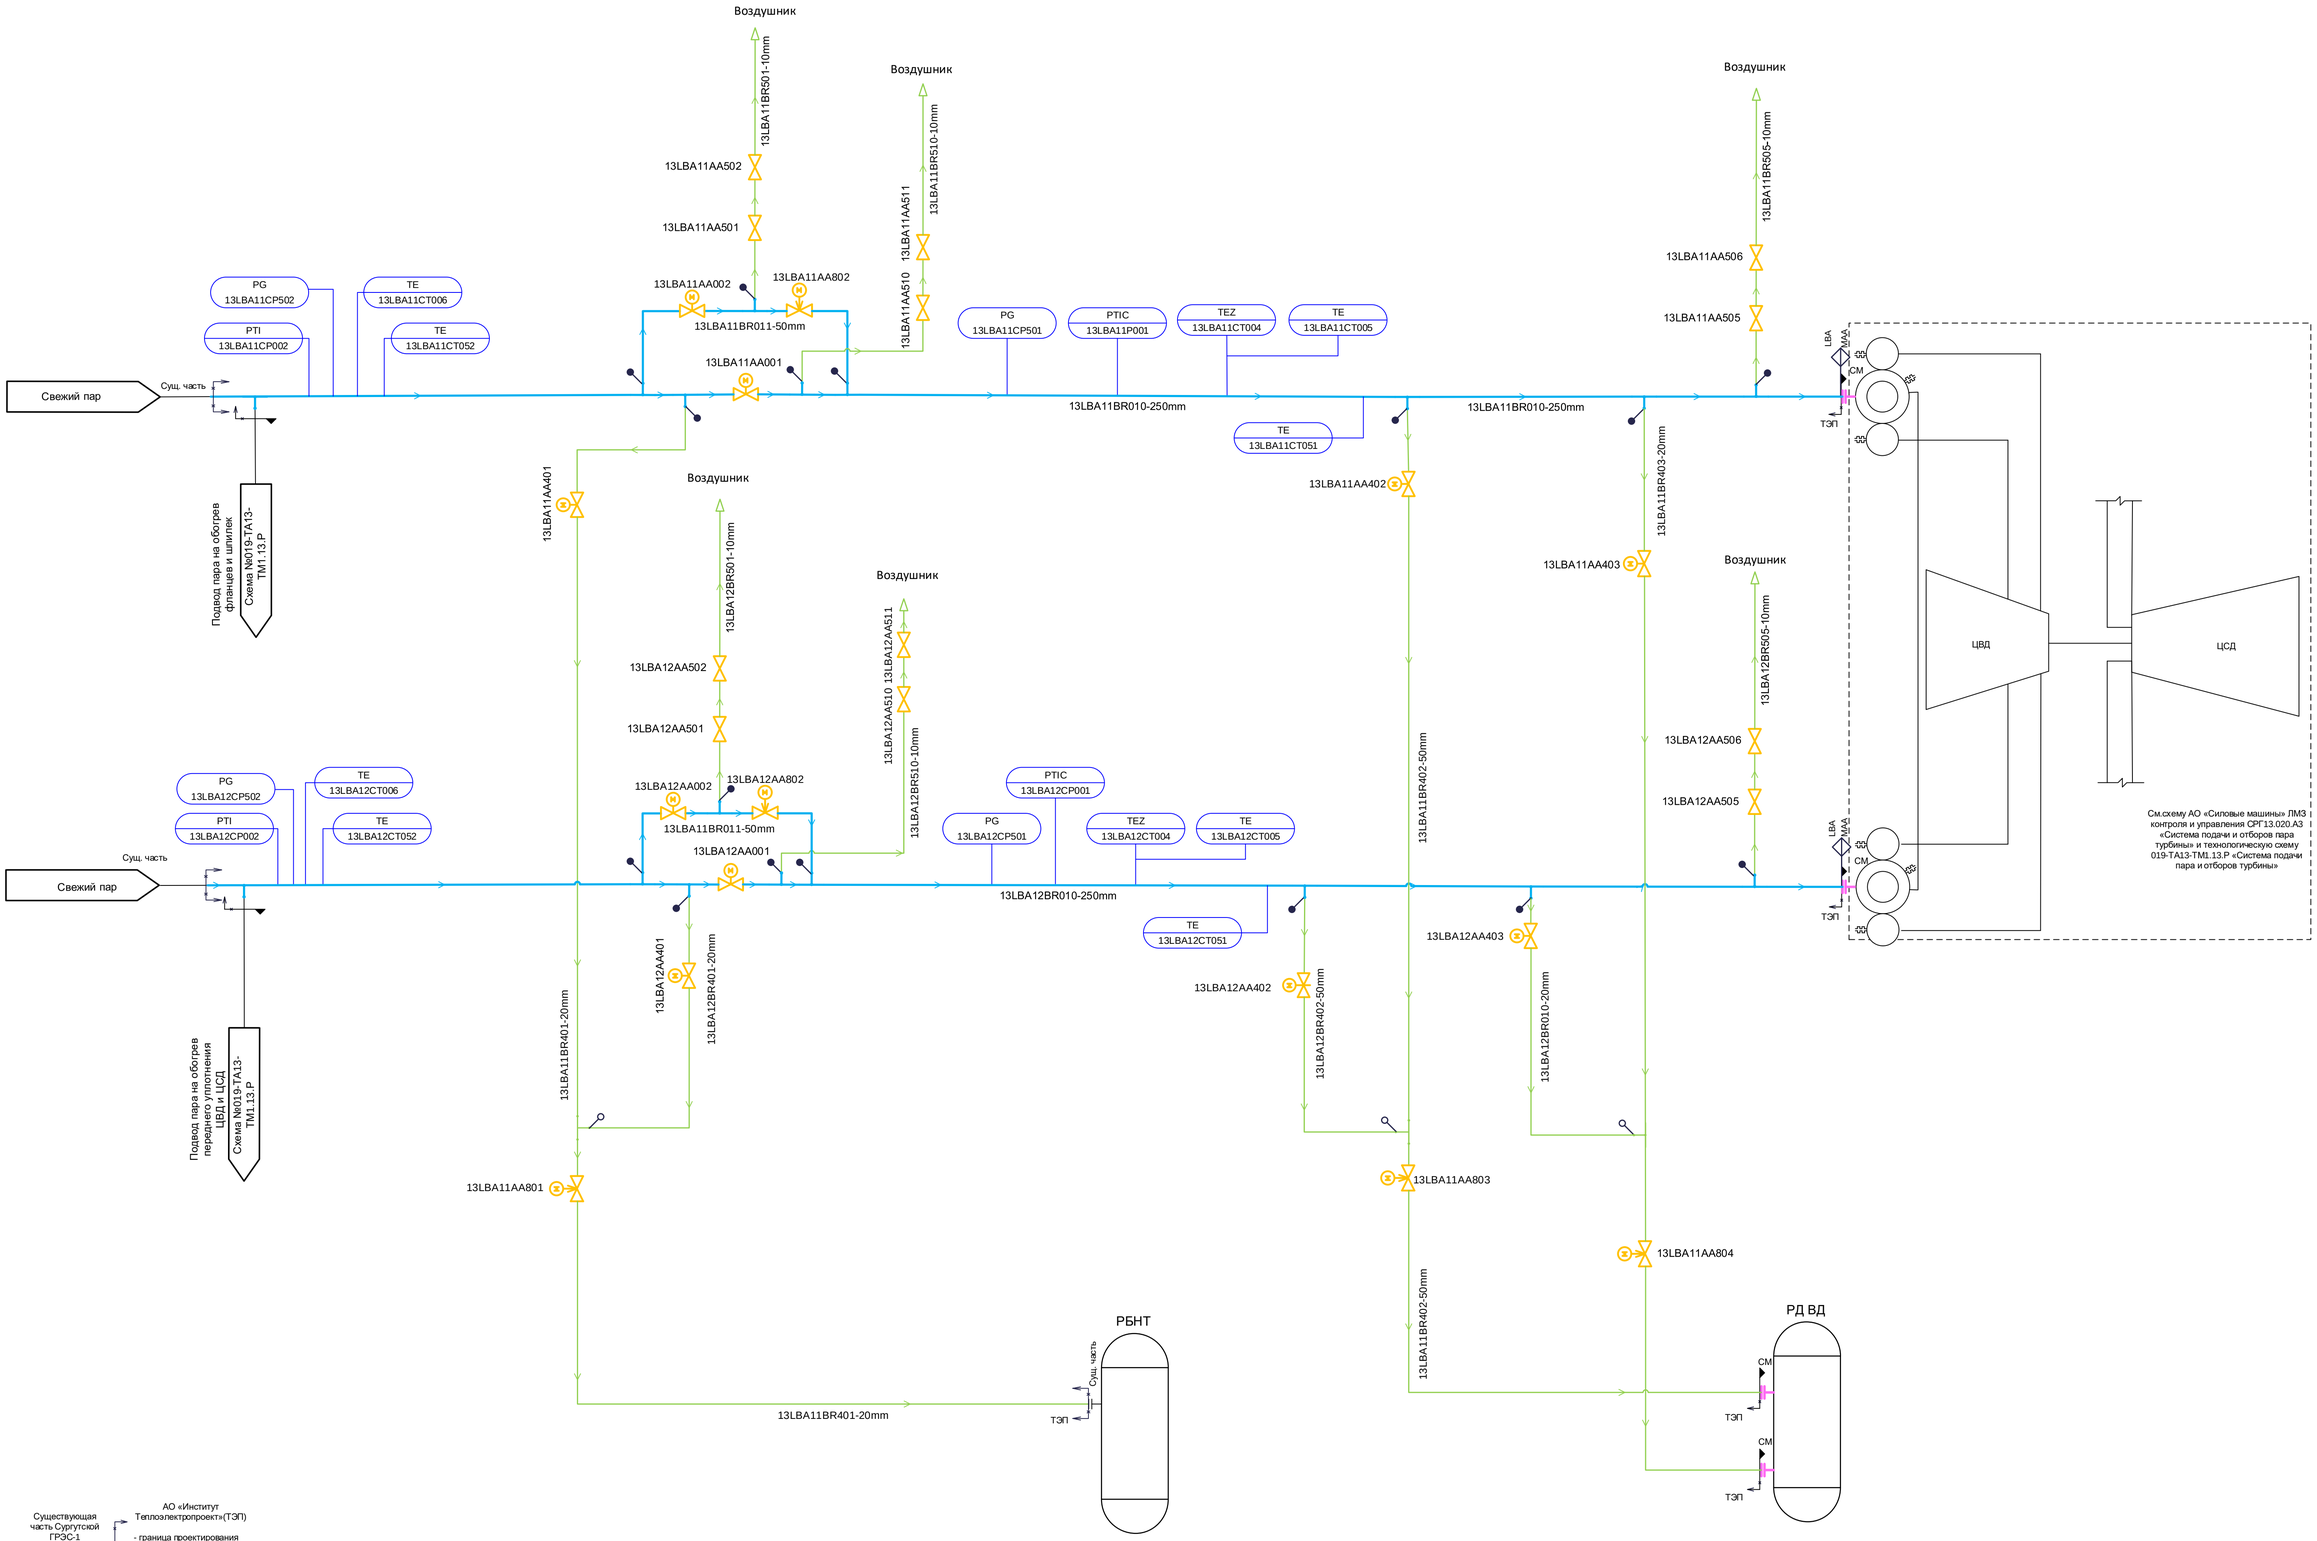

6	-	Зам.	1989-24		07.24	246N1 – 13UHJ – 4159 – TD.M
Изм.	Кол.уч	Лист	№ док.	Подп.	Дата	Модернизация генерирующего объекта Сургутская ГРЭС-1 (13Г)
Разработал		Гусев				Главный корпус. PI-диаграмма свежего пара
Проверил		Демина				Стадия: Р; Лист: 2; Листов:
Н. контр.		Черемушкина				PI-диаграмма свежего пара. Система LBA.

АКЦИОНЕРНОЕ ОБЩЕСТВО ИНСТИТУТ ТЕПЛОЭЛЕКТРОПРОЕКТ Г. МОСКВА

Согласовано: ОАСУ Собчева

Взам. инв. № | Подпись и дата | Инв. № подл.

Формат А1