См. схему «Система маслоснабжения смазки. Схема контроля и управления» ЛМЗ № СРГ13.001.А3 АО «Силовые машины»

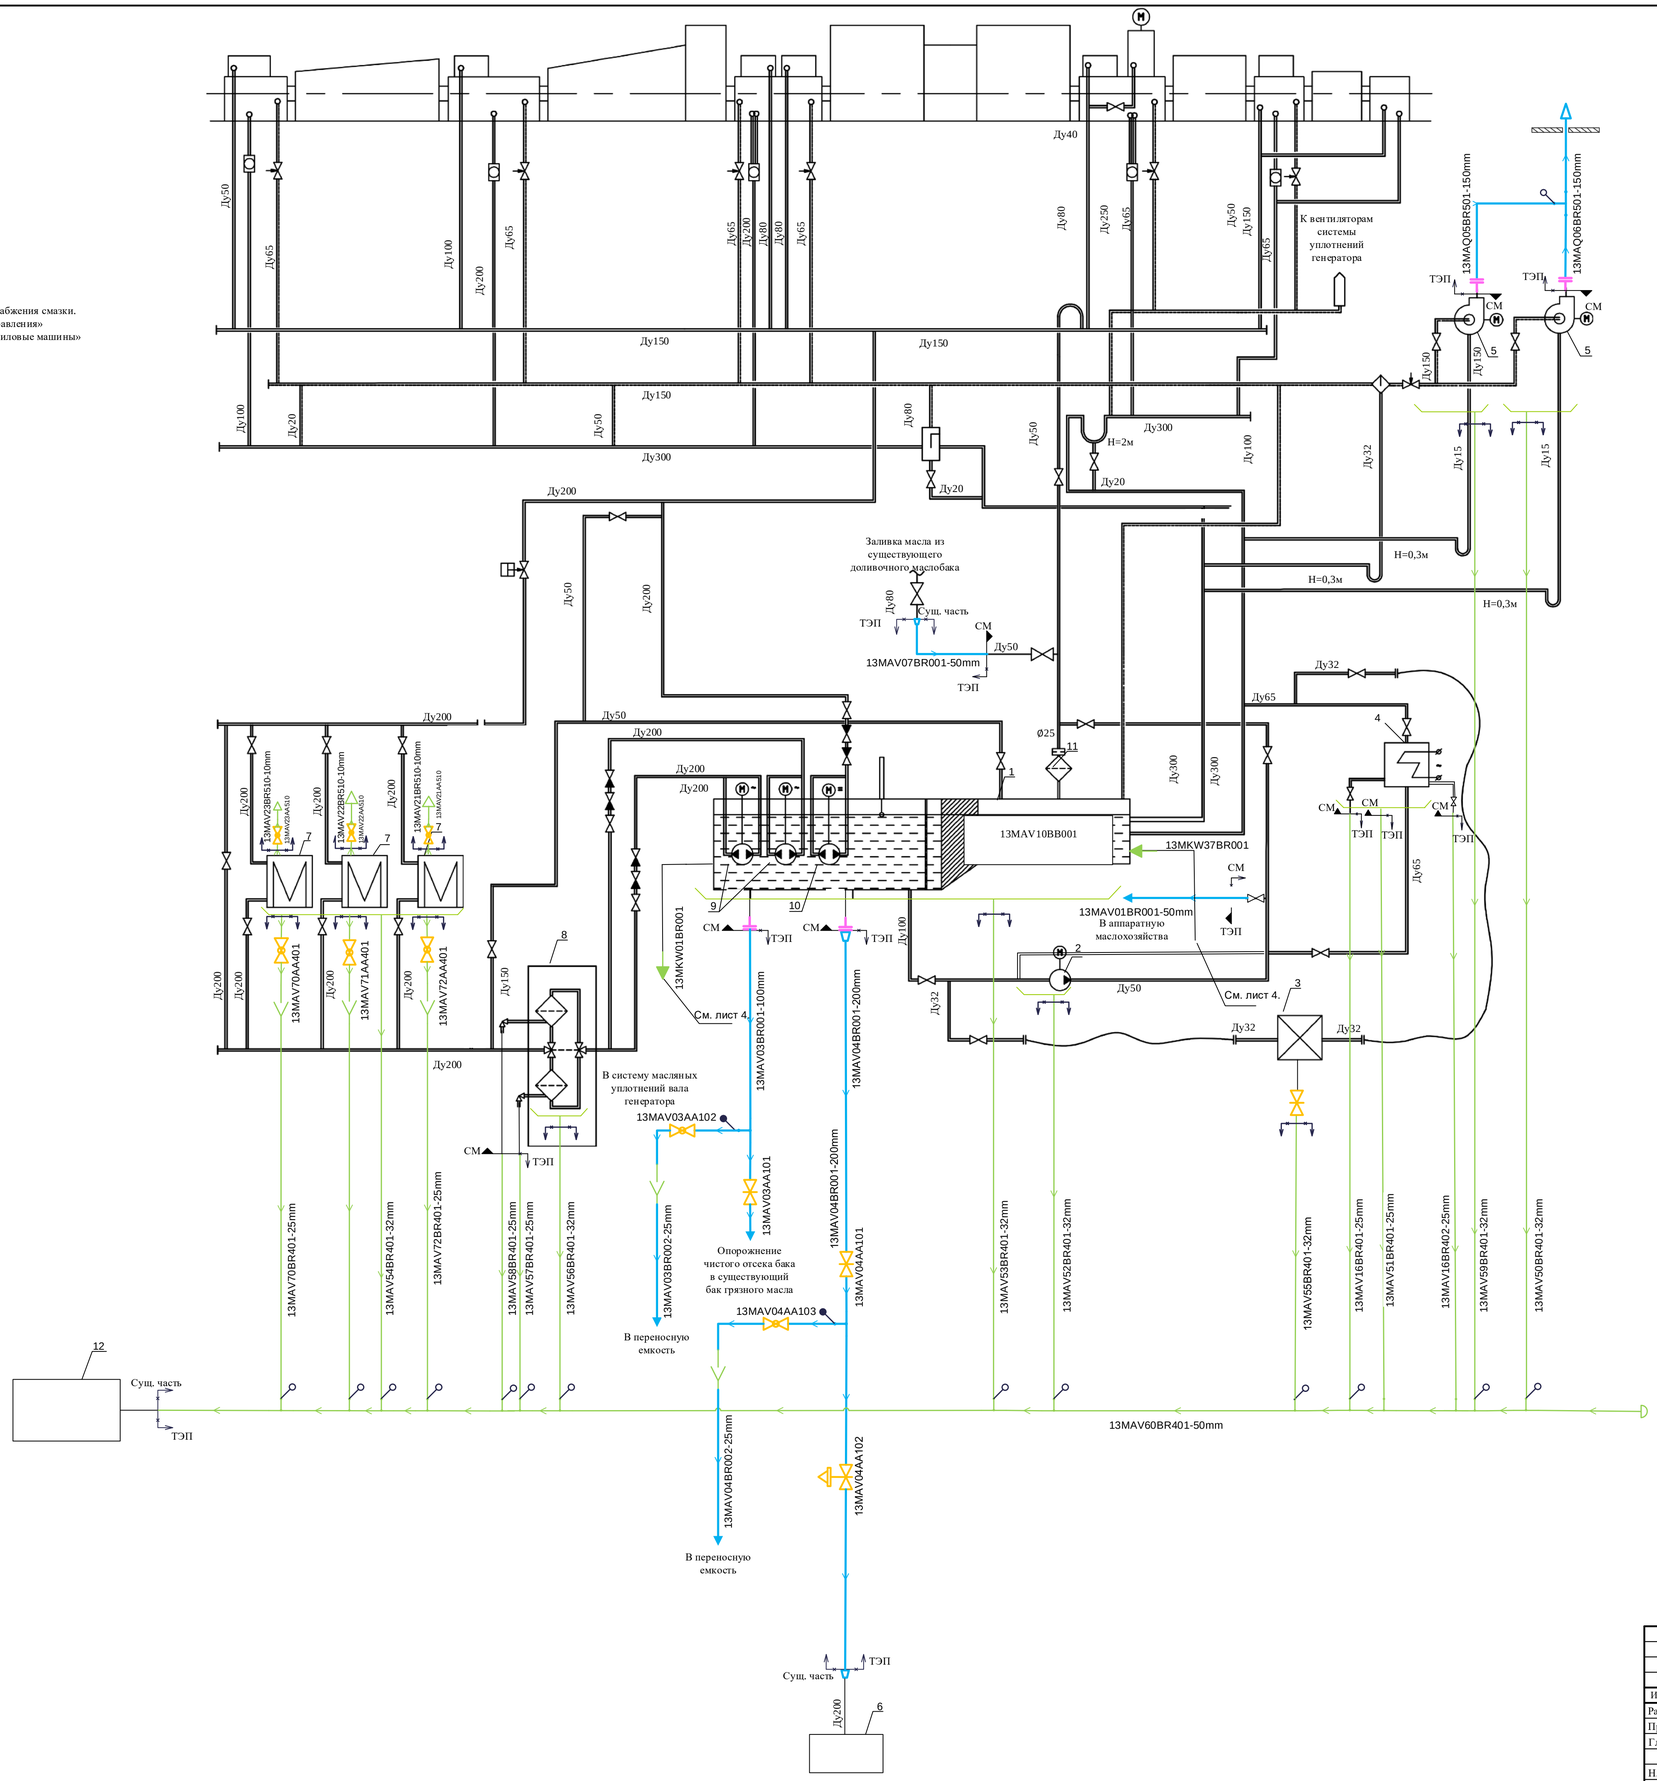

Перечень оборудования

Поз.	Наименование	Кол.
1	Бак масляный ПТ №13	1
2	Насос циркуляции и фильтрации масла	1
3	Агрегат для очистки масла	1
4	Электронагреватель масла	1
5	Вентилятор отсоса масляных паров из бака системы смазки	2
6	Подземный бак аварийного слива масла	1
7	Маслоохладитель системы смазки ПТ	3
8	Дуплексный фильтр	1
9	Насос системы смазки	2
10	Насос аварийный системы смазки	1
11	Фильтр тонкой очистки	1
12	Бак сбора грязного масла V=4 м3	1

Условные обозначения

	Задвижка с ручным колонковым приводом
	Запорная арматура с ручным приводом
	Вентиль
	Обратный клапан
	Клапан для опорожнения
	Фильтр

Примечание:
1)Задвижка 13MAV04AA101
С ручным приводом открыта и опломбирована при эксплуатации.
2)Задвижка 13MAV04AA402 оснащена колонковым приводом.

Существующая часть Сургутской ГРЭС-1 — АО «Институт Теплоэлектропроект» (ТЭП) - граница проектирования

АО «Силовые Машины» (СМ) - граница проектирования — АО «Институт Теплоэлектропроект» (ТЭП)

Согласовано
ОАСУ Соболева

Взам. инв. №
Подпись и дата
Инв. № подл.

5	-	Зам.	1858-23			
Изм.	Кол.уч	Лист	№ док.	Подп.	Дата	

246N1-13UHJ-4160-TD.M

Модернизация генерирующего объекта Сургутская ГРЭС-1 (13г)

Разработал	Гусев	
Проверил	Демина	
Гл.спец.	Ястребов	
Н. контр.	Черемушкина	

Главный корпус
PI-диаграмма трубопроводов маслоснабжения турбоустановки

Стадия	Лист	Листов
Р	2	

PI-диаграмма трубопроводов маслоснабжения системы смазки турбины. Система MAV

АКЦИОНЕРНОЕ ОБЩЕСТВО ИНСТИТУТ ТЕПЛОЭЛЕКТРОПРОЕКТ г. МОСКВА

Формат А1