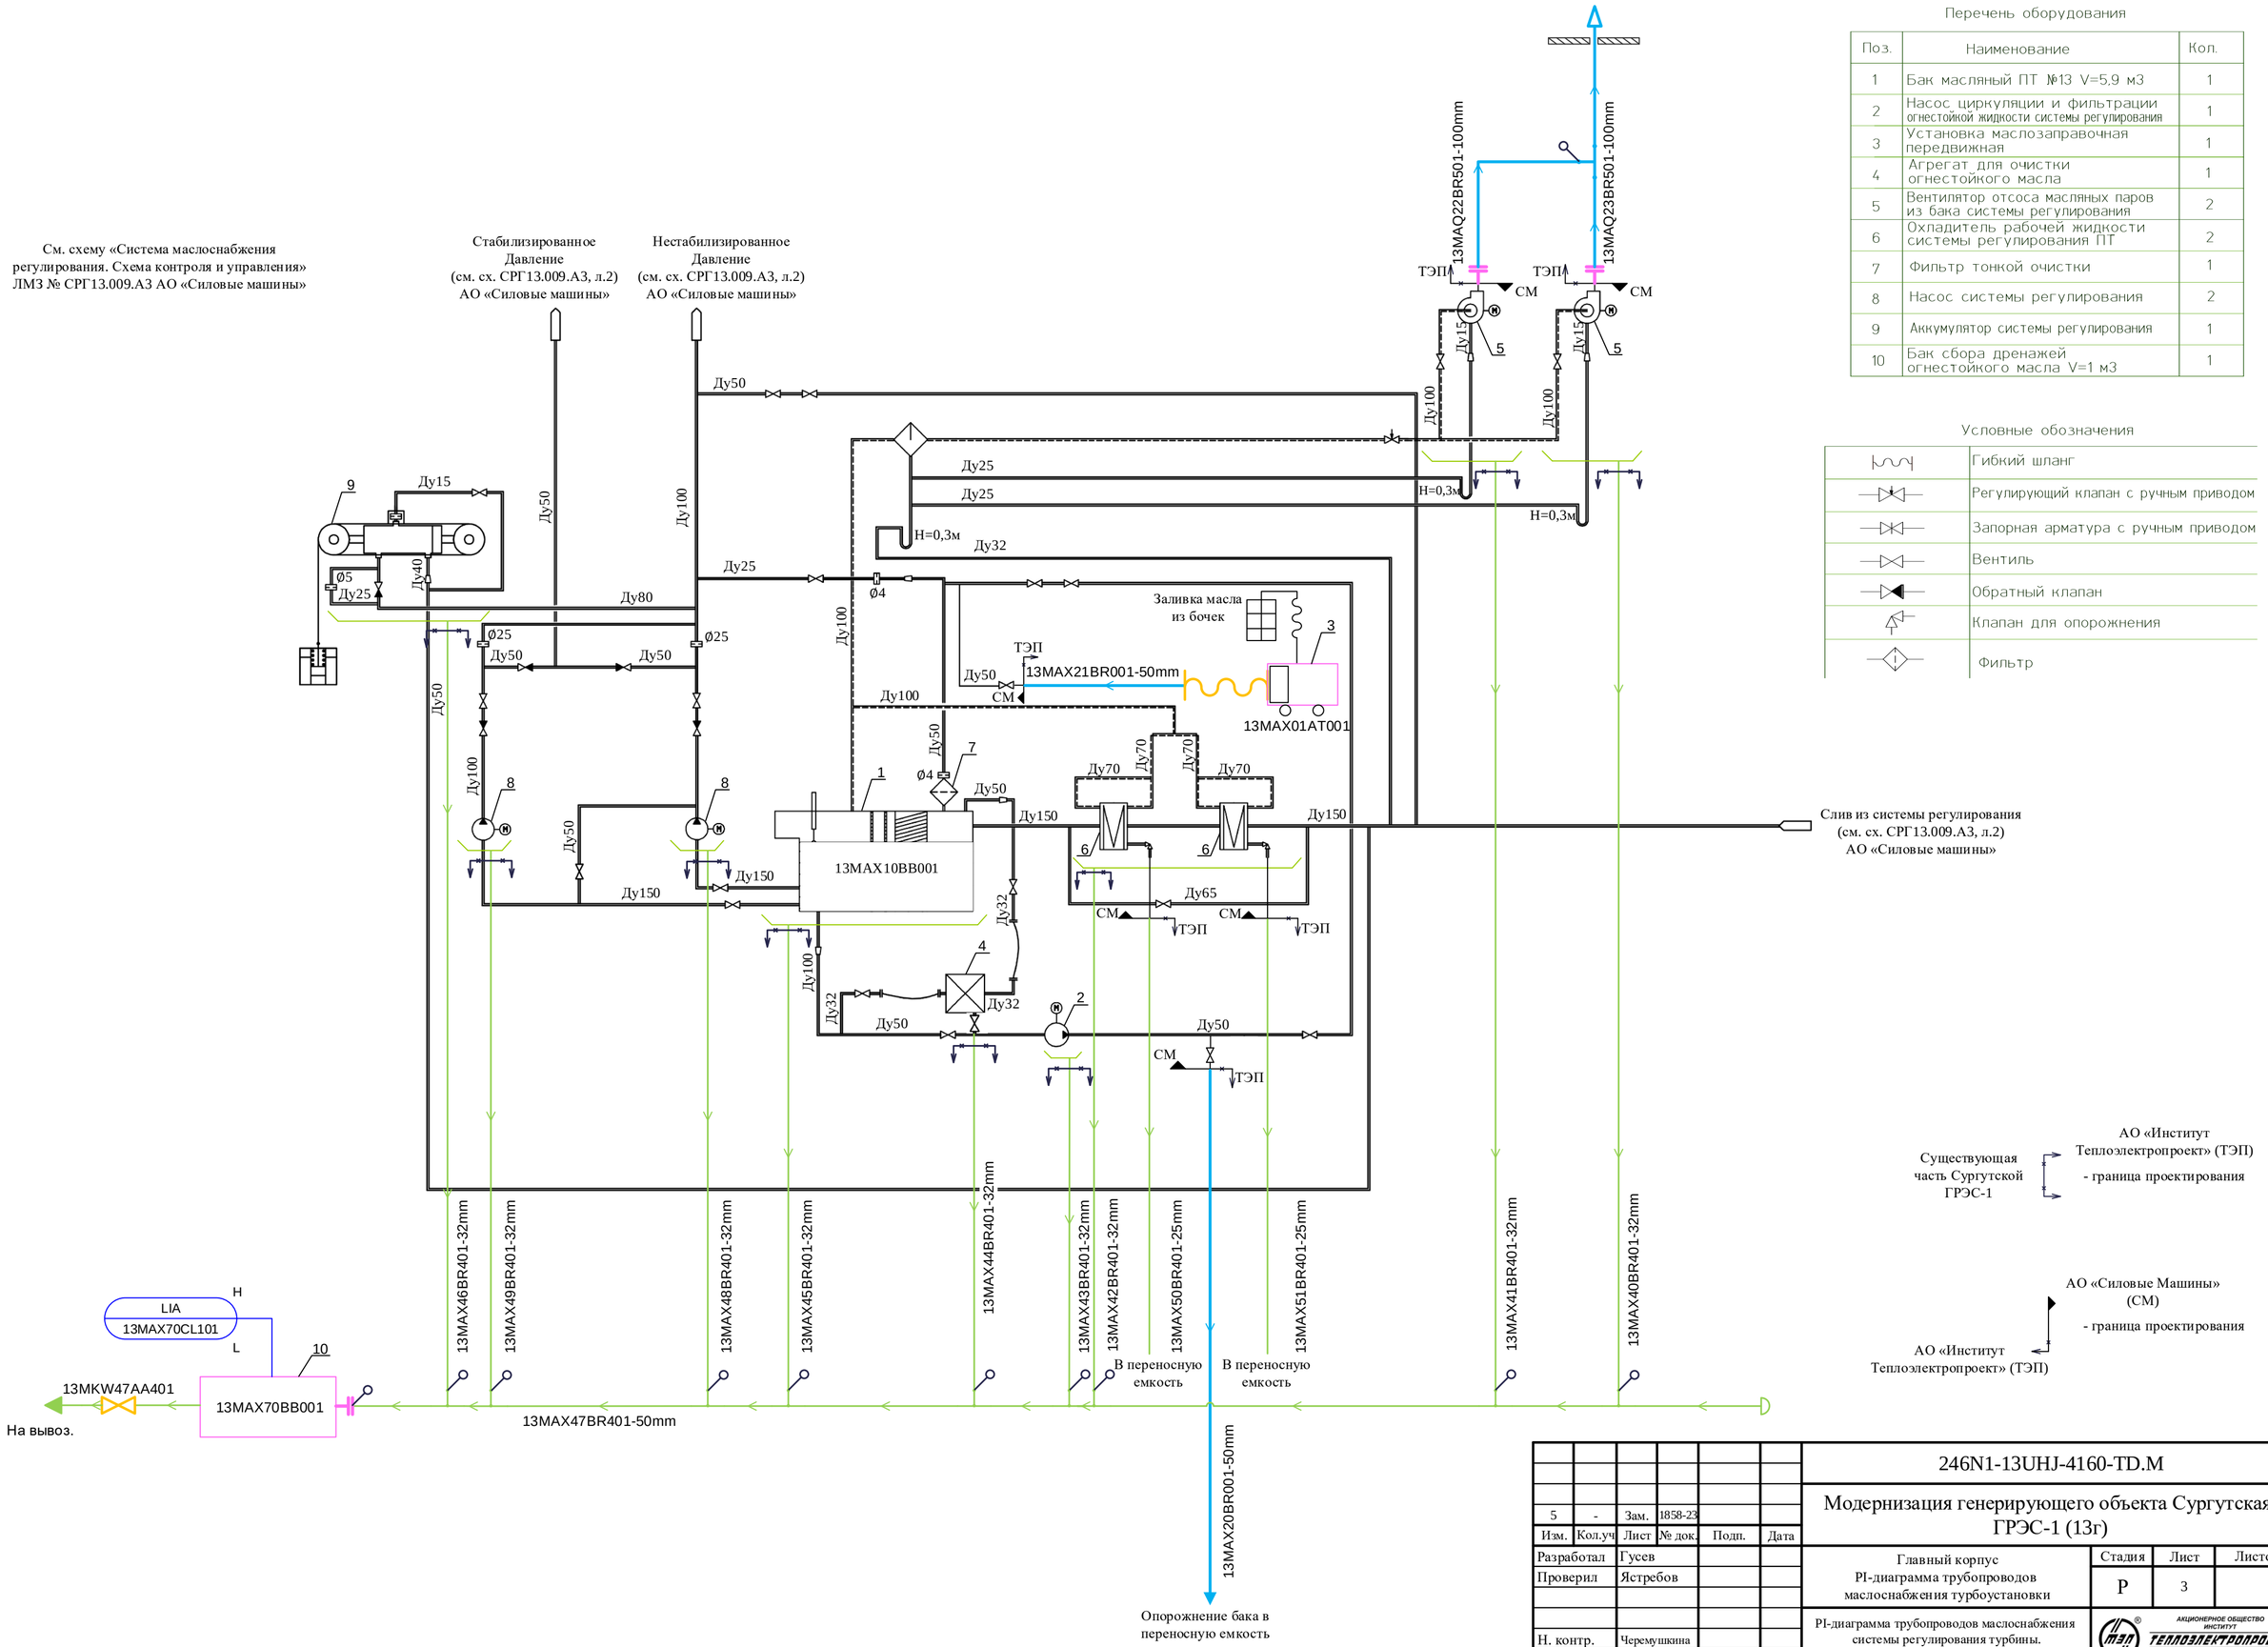

Перечень оборудования

Поз.	Наименование	Кол.
1	Бак масляный ПТ №13 V=5,9 м3	1
2	Насос циркуляции и фильтрации огнестойкой жидкости системы регулирования	1
3	Установка маслозаправочная передвижная	1
4	Агрегат для очистки огнестойкого масла	1
5	Вентилятор отсоса масляных паров из бака системы регулирования	2
6	Охладитель рабочей жидкости системы регулирования ПТ	2
7	Фильтр тонкой очистки	1
8	Насос системы регулирования	2
9	Аккумулятор системы регулирования	1
10	Бак сбора дренажей огнестойкого масла V=1 м3	1

Условные обозначения

	Гибкий шланг
	Регулирующий клапан с ручным приводом
	Запорная арматура с ручным приводом
	Вентиль
	Обратный клапан
	Клапан для опорожнения
	Фильтр

Согласовано
ОАСУ Соболева
Взам. инв. №
Подпись и дата
Инв. № подл.

Изм.	Кол.уч	Лист	№ док.	Подп.	Дата
5	-	Зам.	1858-23		

246N1-13UHJ-4160-TD.M

Модернизация генерирующего объекта Сургутская ГРЭС-1 (13г)

Разработал	Гусев	
Проверил	Ястребов	
Н. контр.	Черемушкина	

Главный корпус
PI-диаграмма трубопроводов маслоснабжения турбоустановки

Стадия	Лист	Листов
Р	3	

PI-диаграмма трубопроводов маслоснабжения системы регулирования турбины. Система МАХ

АКЦИОНЕРНОЕ ОБЩЕСТВО ИНСТИТУТ ТЕПЛОЭЛЕКТРОПРОЕКТ Г. МОСКВА

Формат А2