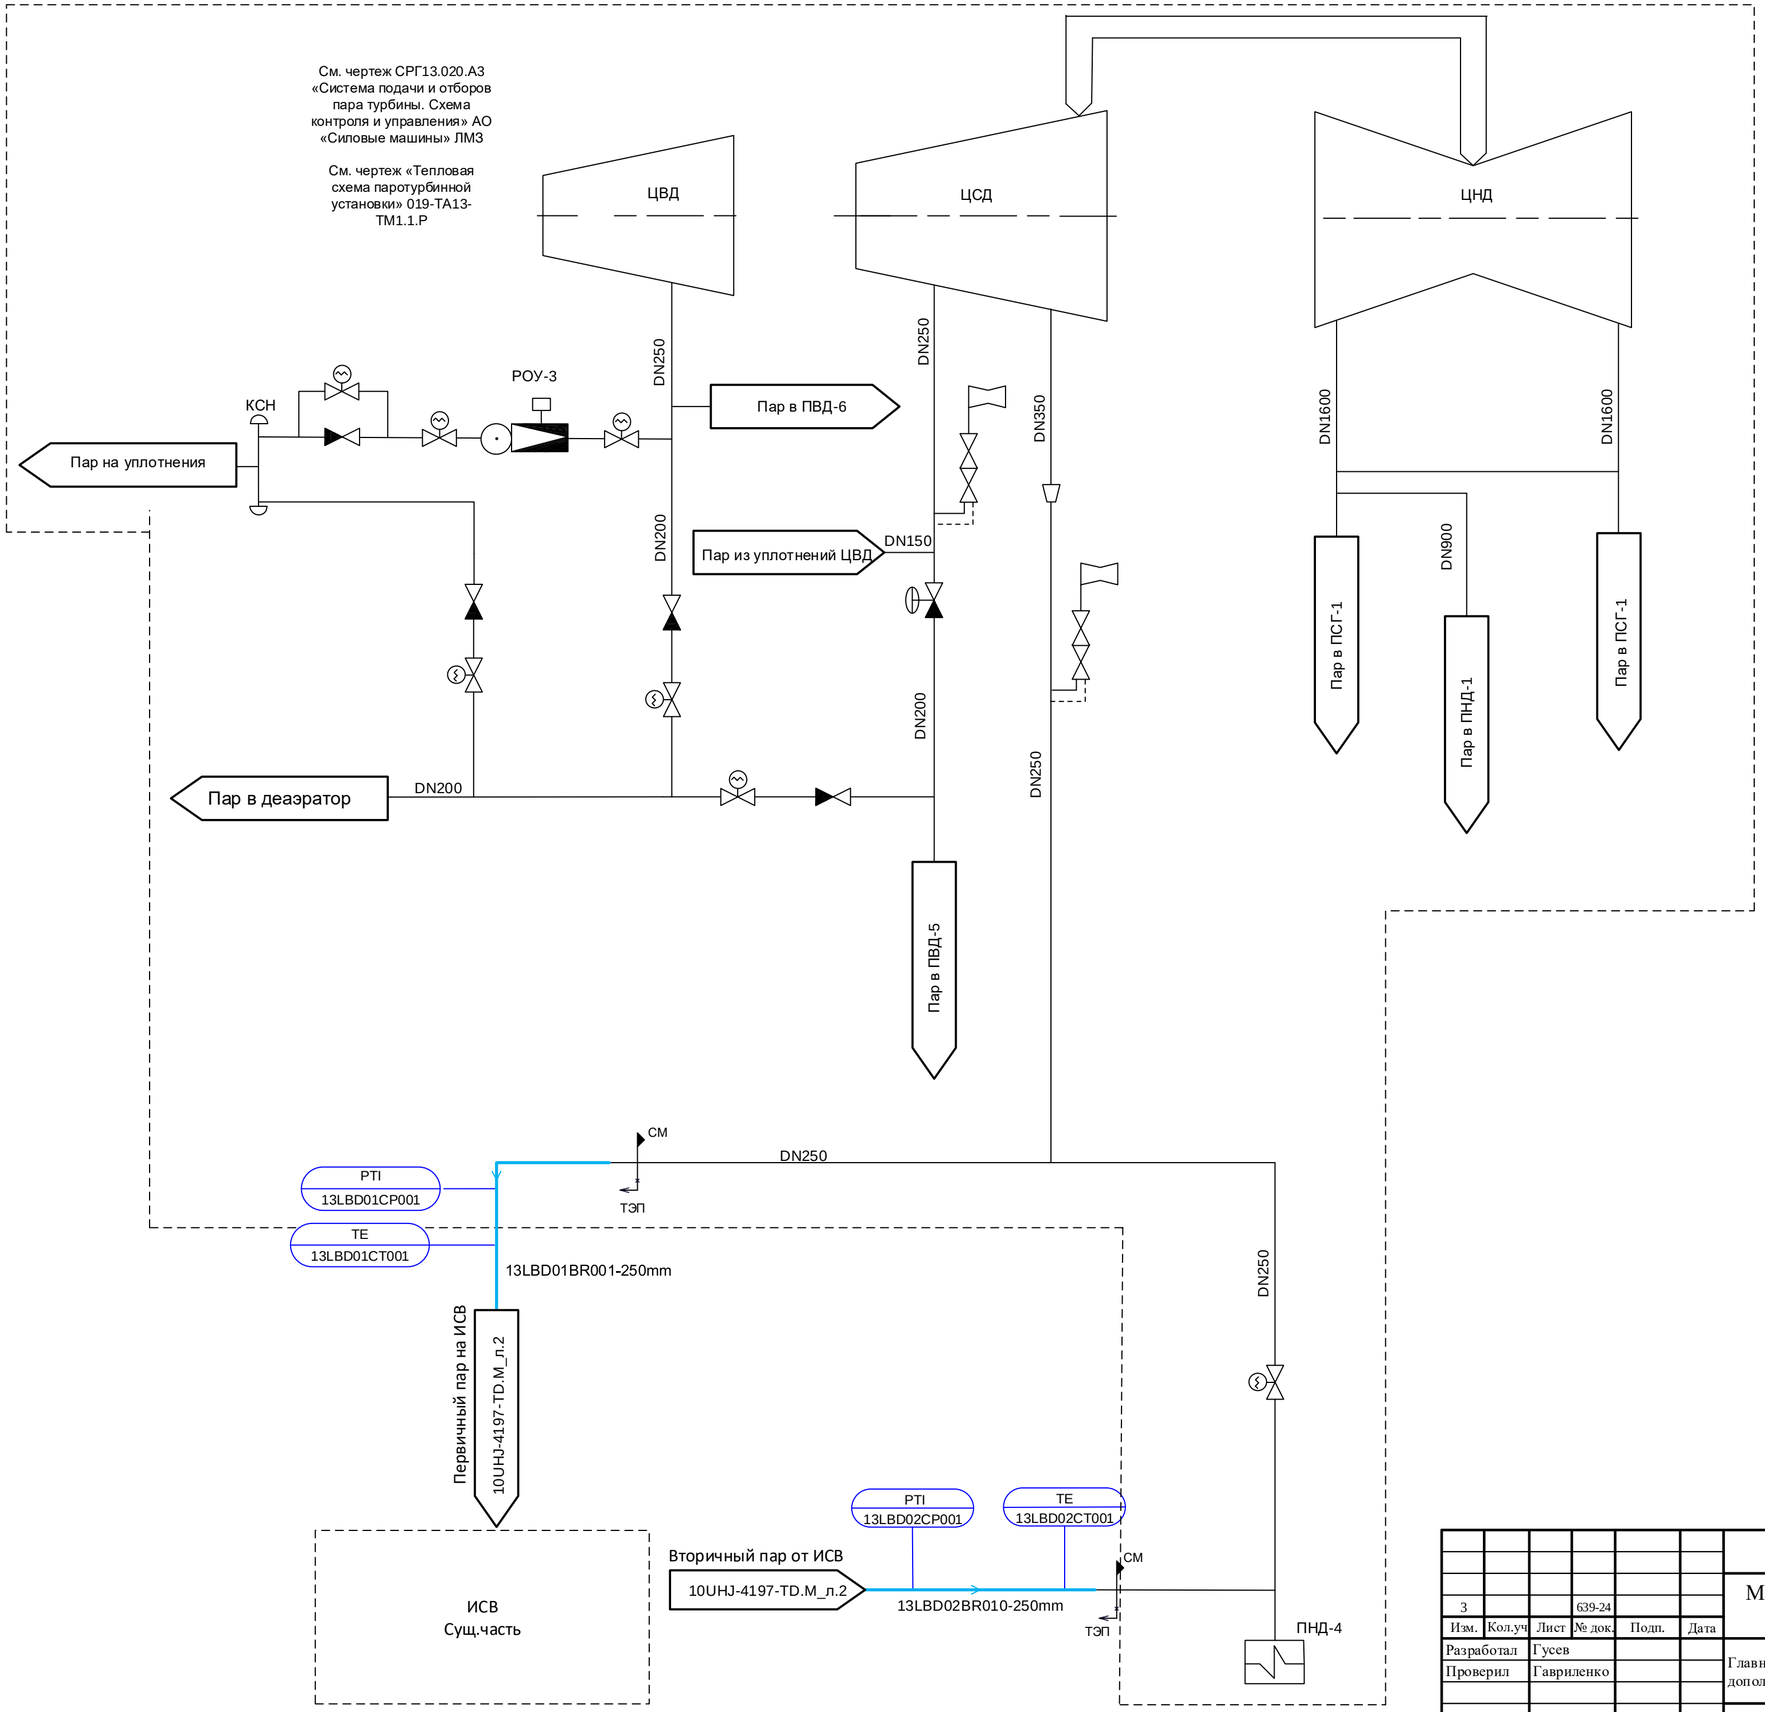

3			639-24			
Изм.	Кол.уч	Лист	№ док.	Подп.	Дата	
Разработал		Гусев				
Проверил		Гавриленко				
Н. контр.		Астраханцев				

246N1 – 13UHJ – 4161 – TD.M

Модернизация генерирующего объекта Сургутской ГРЭС-1 (13Г)

Главный корпус. PI-диаграмма дополнительного отбора собственных нужд.

Стадия	Лист	Листов
Р	2	

PI-диаграмма дополнительного отбора собственных нужд. Система LBD

АКЦИОНЕРНОЕ ОБЩЕСТВО ИНСТИТУТ ТЕПЛОЭЛЕКТРОПРОЕКТ Г. МОСКВА

Согласовано
ОАСУ Соболева
Взам. инв. №
Подпись и дата
Инв. № подл.

Формат А2