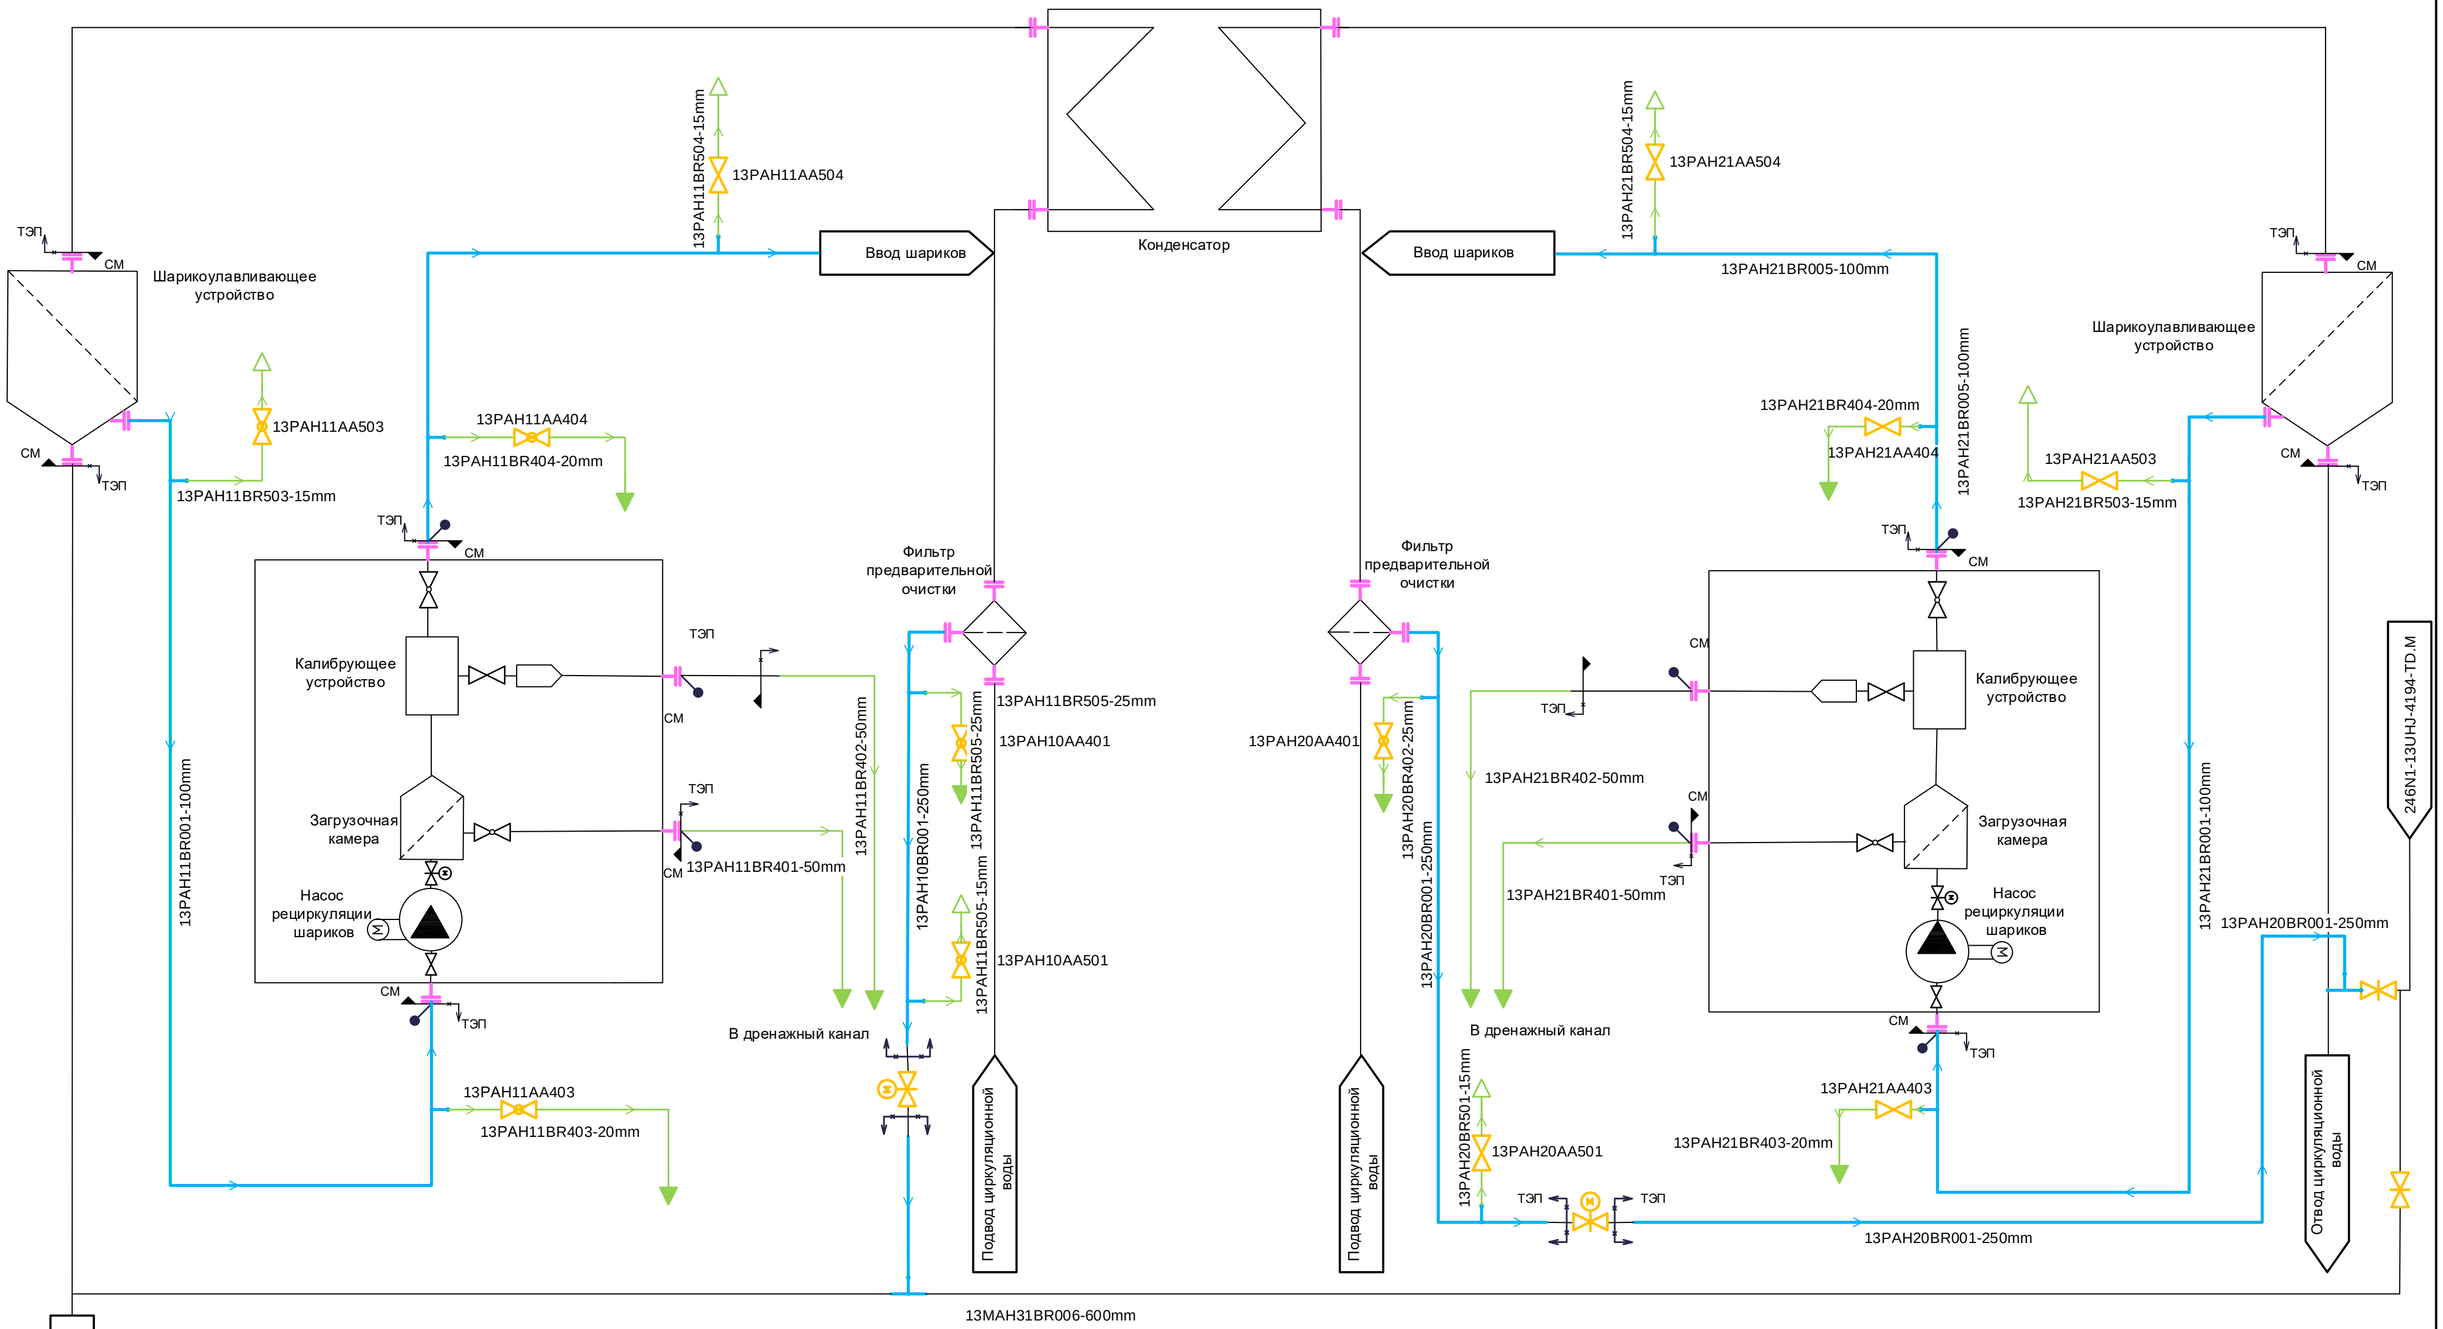

1		1189-23			07.23	
Изм.	Кол.уч	Лист	№ док.	Подп.	Дата	
Разработал		Гусев				
Проверил		Сладков				
Н. контр.		Астраханцев				

246N1 – 16UHJ – 4165 – TD.M

Модернизация генерирующего объекта Сургутская ГРЭС-1 (13г)

Главный корпус. PI-диаграмма трубопроводов системы шариковой очистки конденсатора турбоагрегата.

Стадия	Лист	Листов
Р	2	

PI-диаграмма трубопроводов системы шариковой очистки конденсатора турбоагрегата. Система РАН

АКЦИОНЕРНОЕ ОБЩЕСТВО ИНСТИТУТ ТЕПЛОЭЛЕКТРОПРОЕКТ Г. МОСКВА

Согласовано: ОАСУ Соболева

Взам. инв. №

Подпись и дата

Инв. № подл.

Формат А2