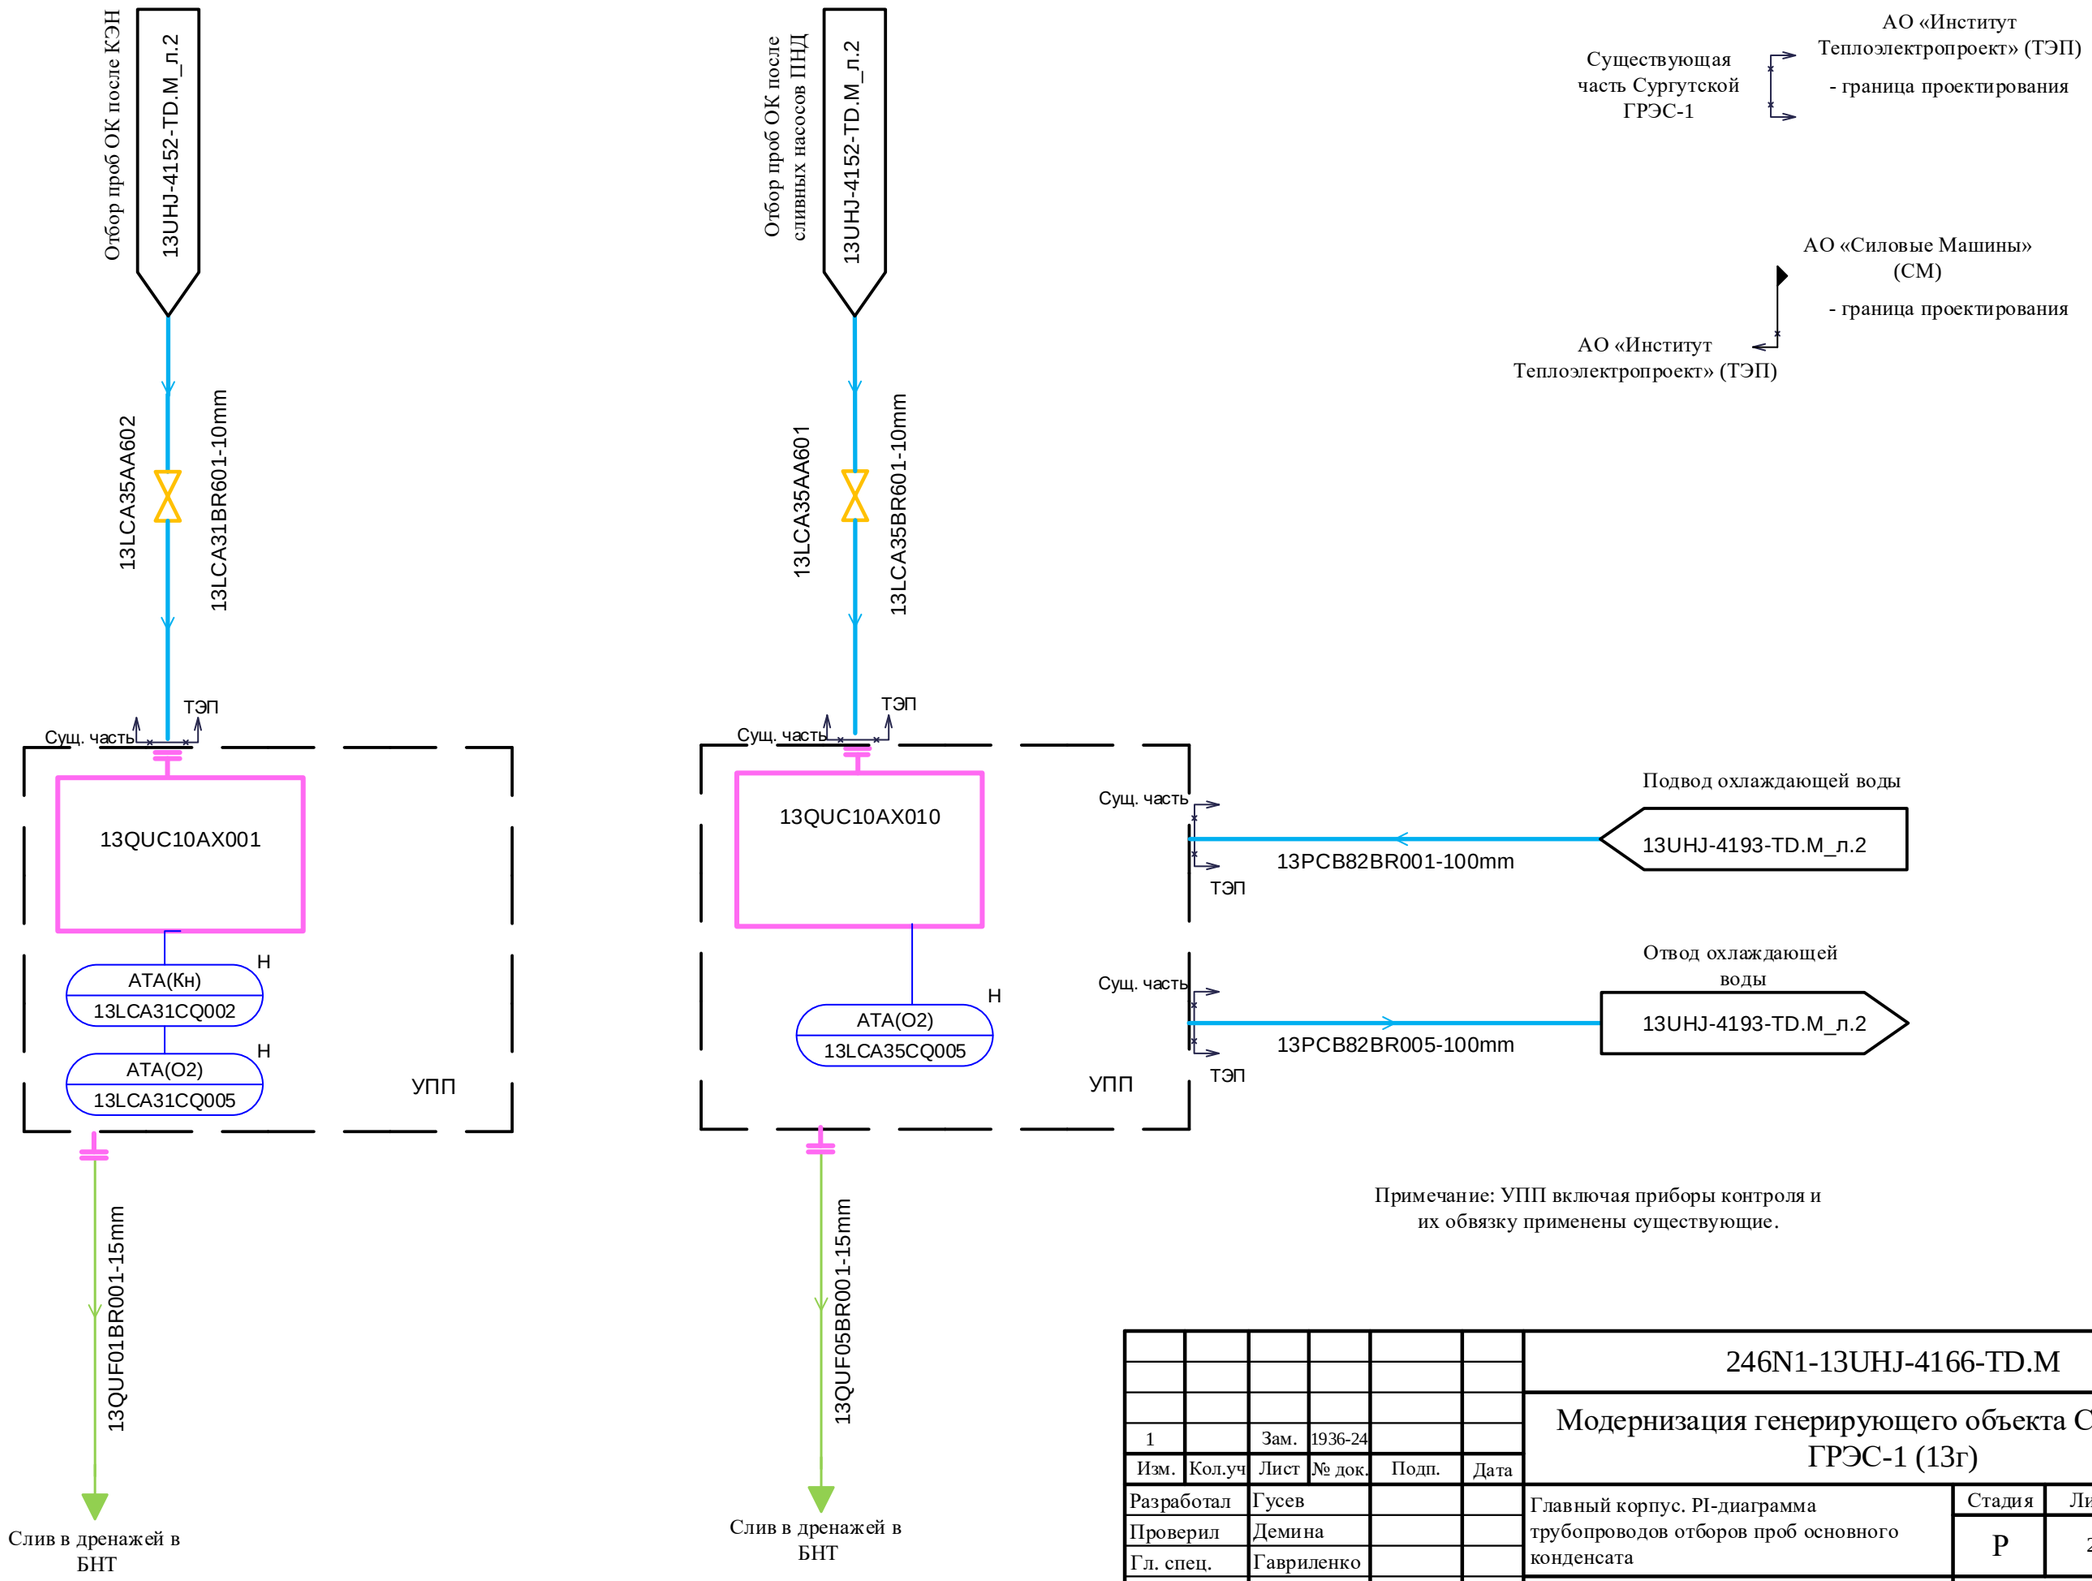

Примечание: УПП включая приборы контроля и их обвязку применены существующие.

Согласовано

ОАСУ

Морозова

Взам. инв. №

Подпись и дата

Инв. № подл.

1		Зам.	1936-24			
Изм.	Кол.уч	Лист	№ док.	Подп.	Дата	
Разработал		Гусев				
Проверил		Демина				
Гл. спец.		Гавриленко				
Н. контр.		Астраханцев				

246N1-13UHJ-4166-TD.M

Модернизация генерирующего объекта Сургутская ГРЭС-1 (13г)

Главный корпус. PI-диаграмма трубопроводов отборов проб основного конденсата

Стадия	Лист	Листов
Р	2	

PI-диаграмма трубопроводов отборов проб основного конденсата. Система QU, PCB

АКЦИОНЕРНОЕ ОБЩЕСТВО ИНСТИТУТ ТЕПЛОЭЛЕКТРОПРОЕКТ Г. МОСКВА

Формат А3