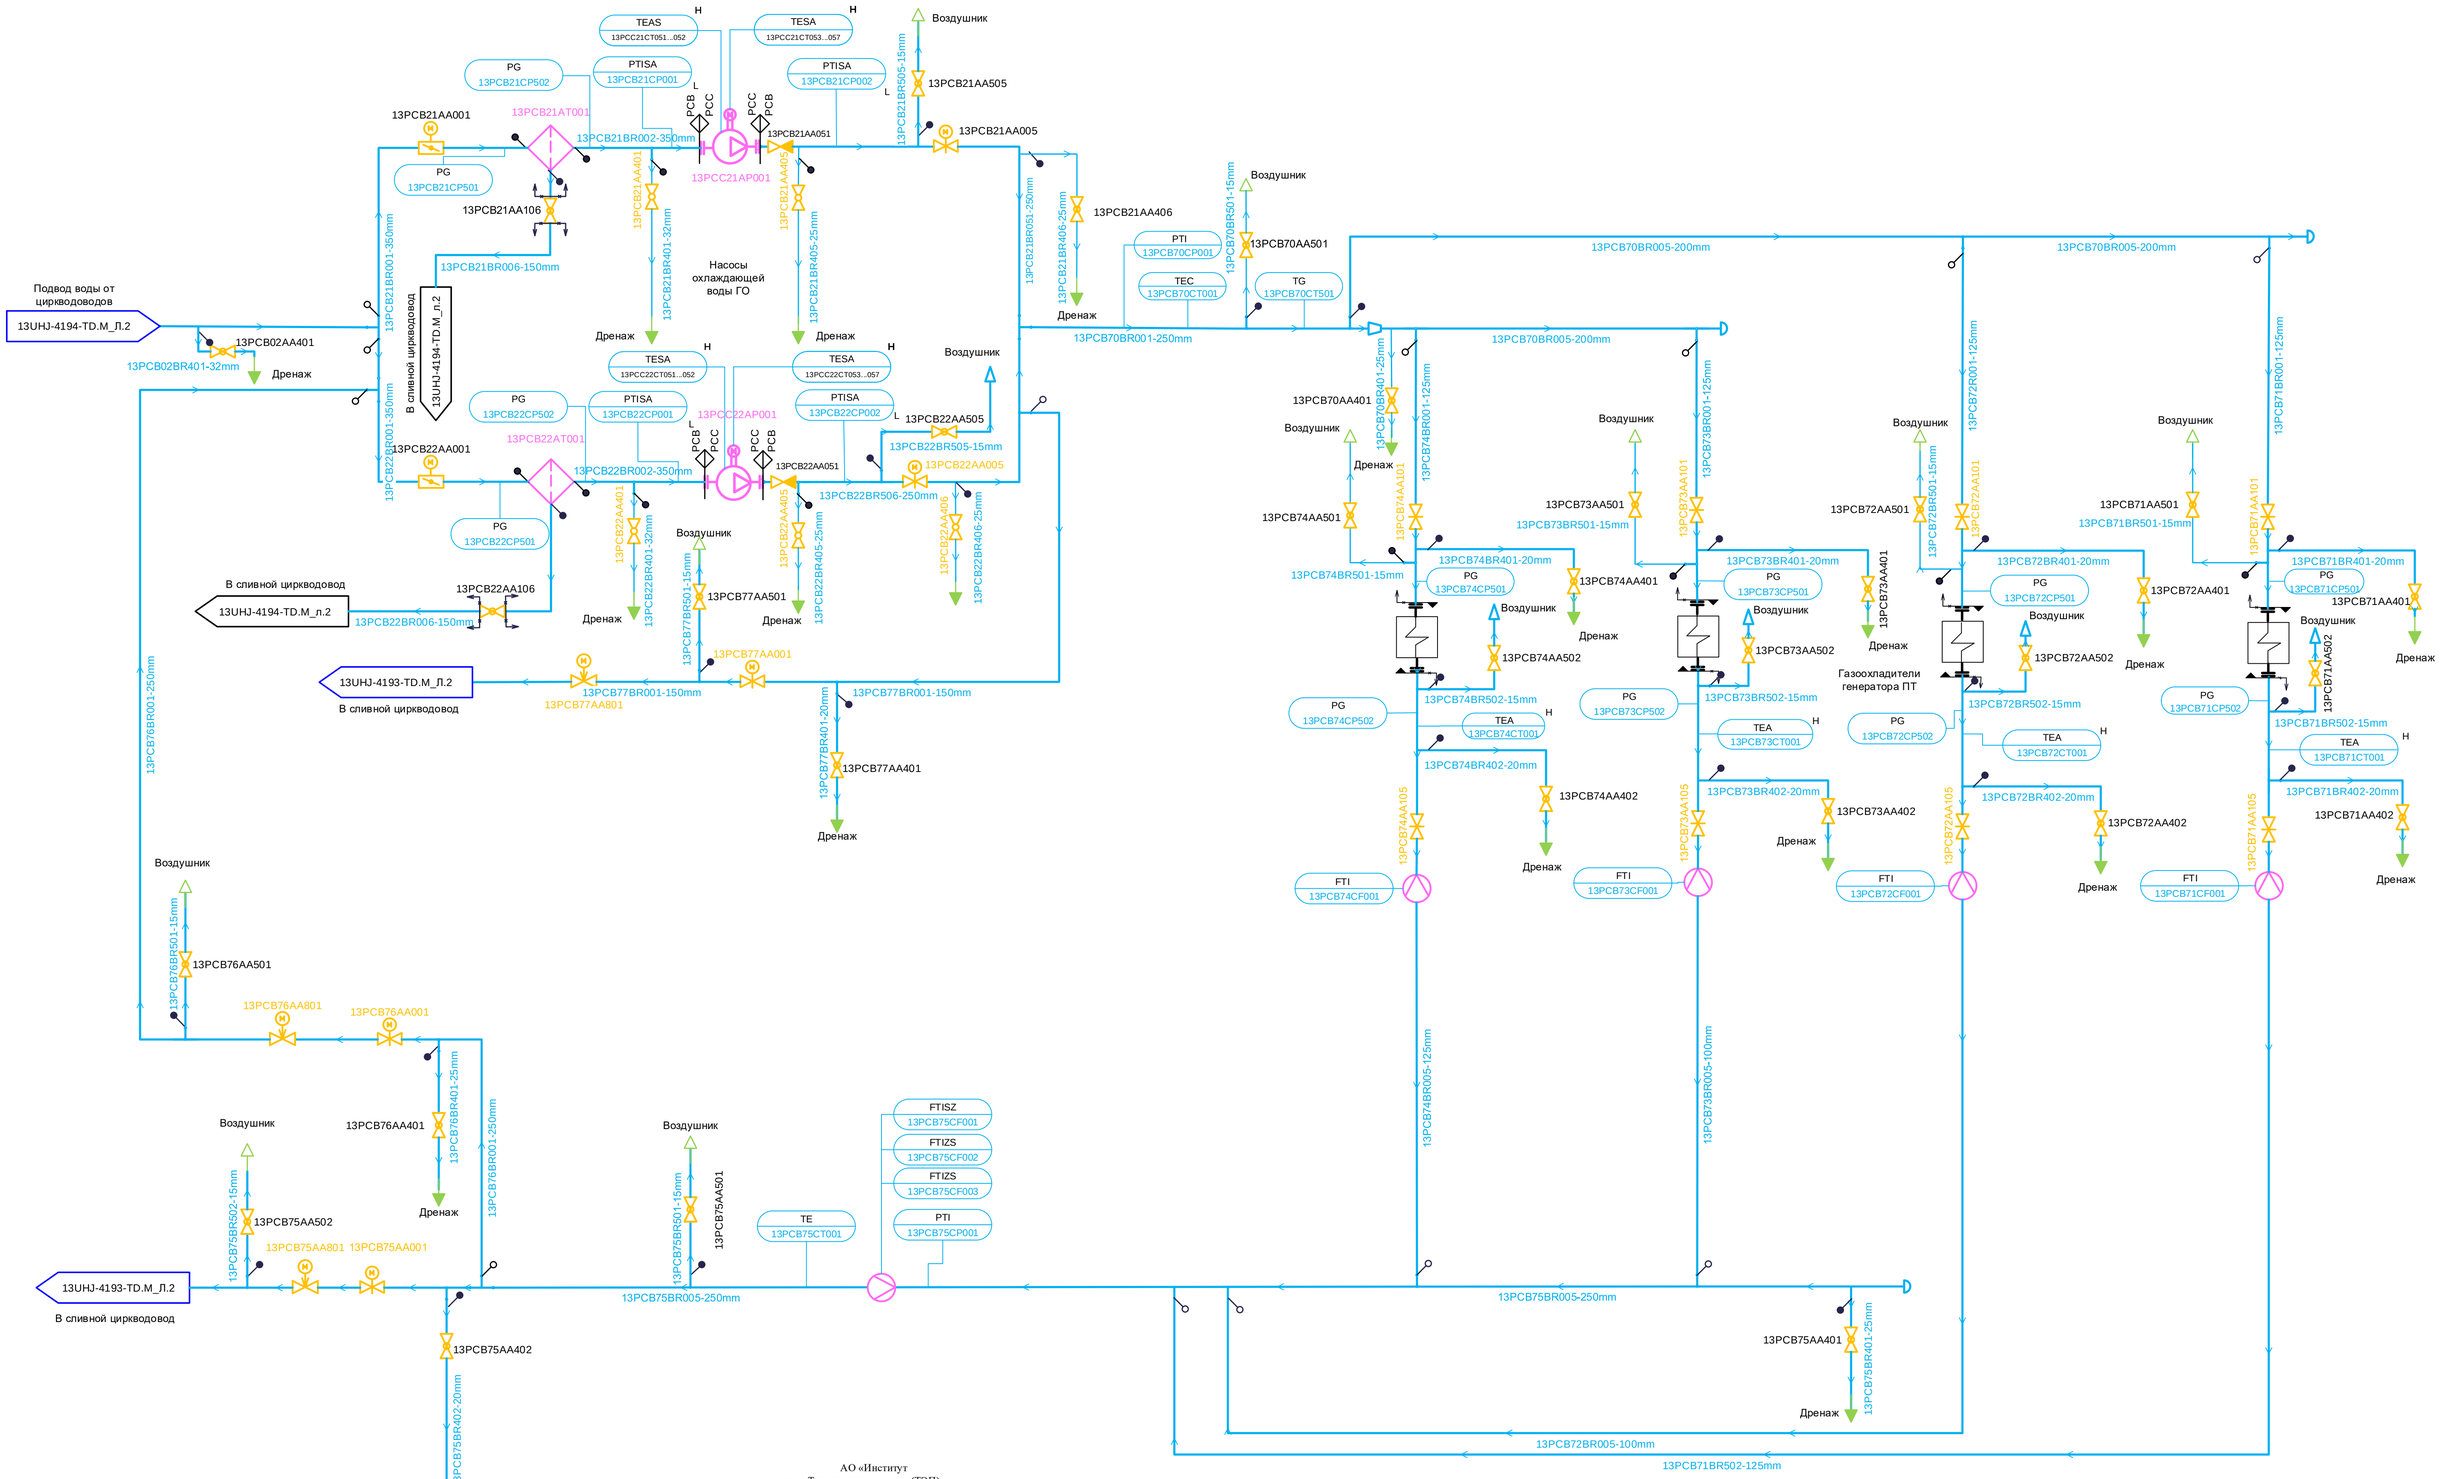

3	-	Зам.	1936-24		07.24	
Изм.	Кол.уч	Лист	№ док.	Подп.	Дата	
Разработал		Гусев. Т.				
Проверил		Демина				
Н. контр.		Астраханцев				

246N1-13UHJ-4193-TD.M

Модернизация генерирующего объекта Сургутская ГРЭС-1 (13Г)

Главный корпус.PI-диаграмма охлаждающей воды вспомогательного оборудования турбоагрегата.

Главный корпус.PI-диаграмма охлаждающей воды вспомогательного оборудования турбоагрегата. Система РСВ

Стадия	Лист	Листов
Р	3	

АКЦИОНЕРНОЕ ОБЩЕСТВО ИНСТИТУТ ТЕПЛОЭЛЕКТРОПРОЕКТ Г. МОСКВА

Формат А1