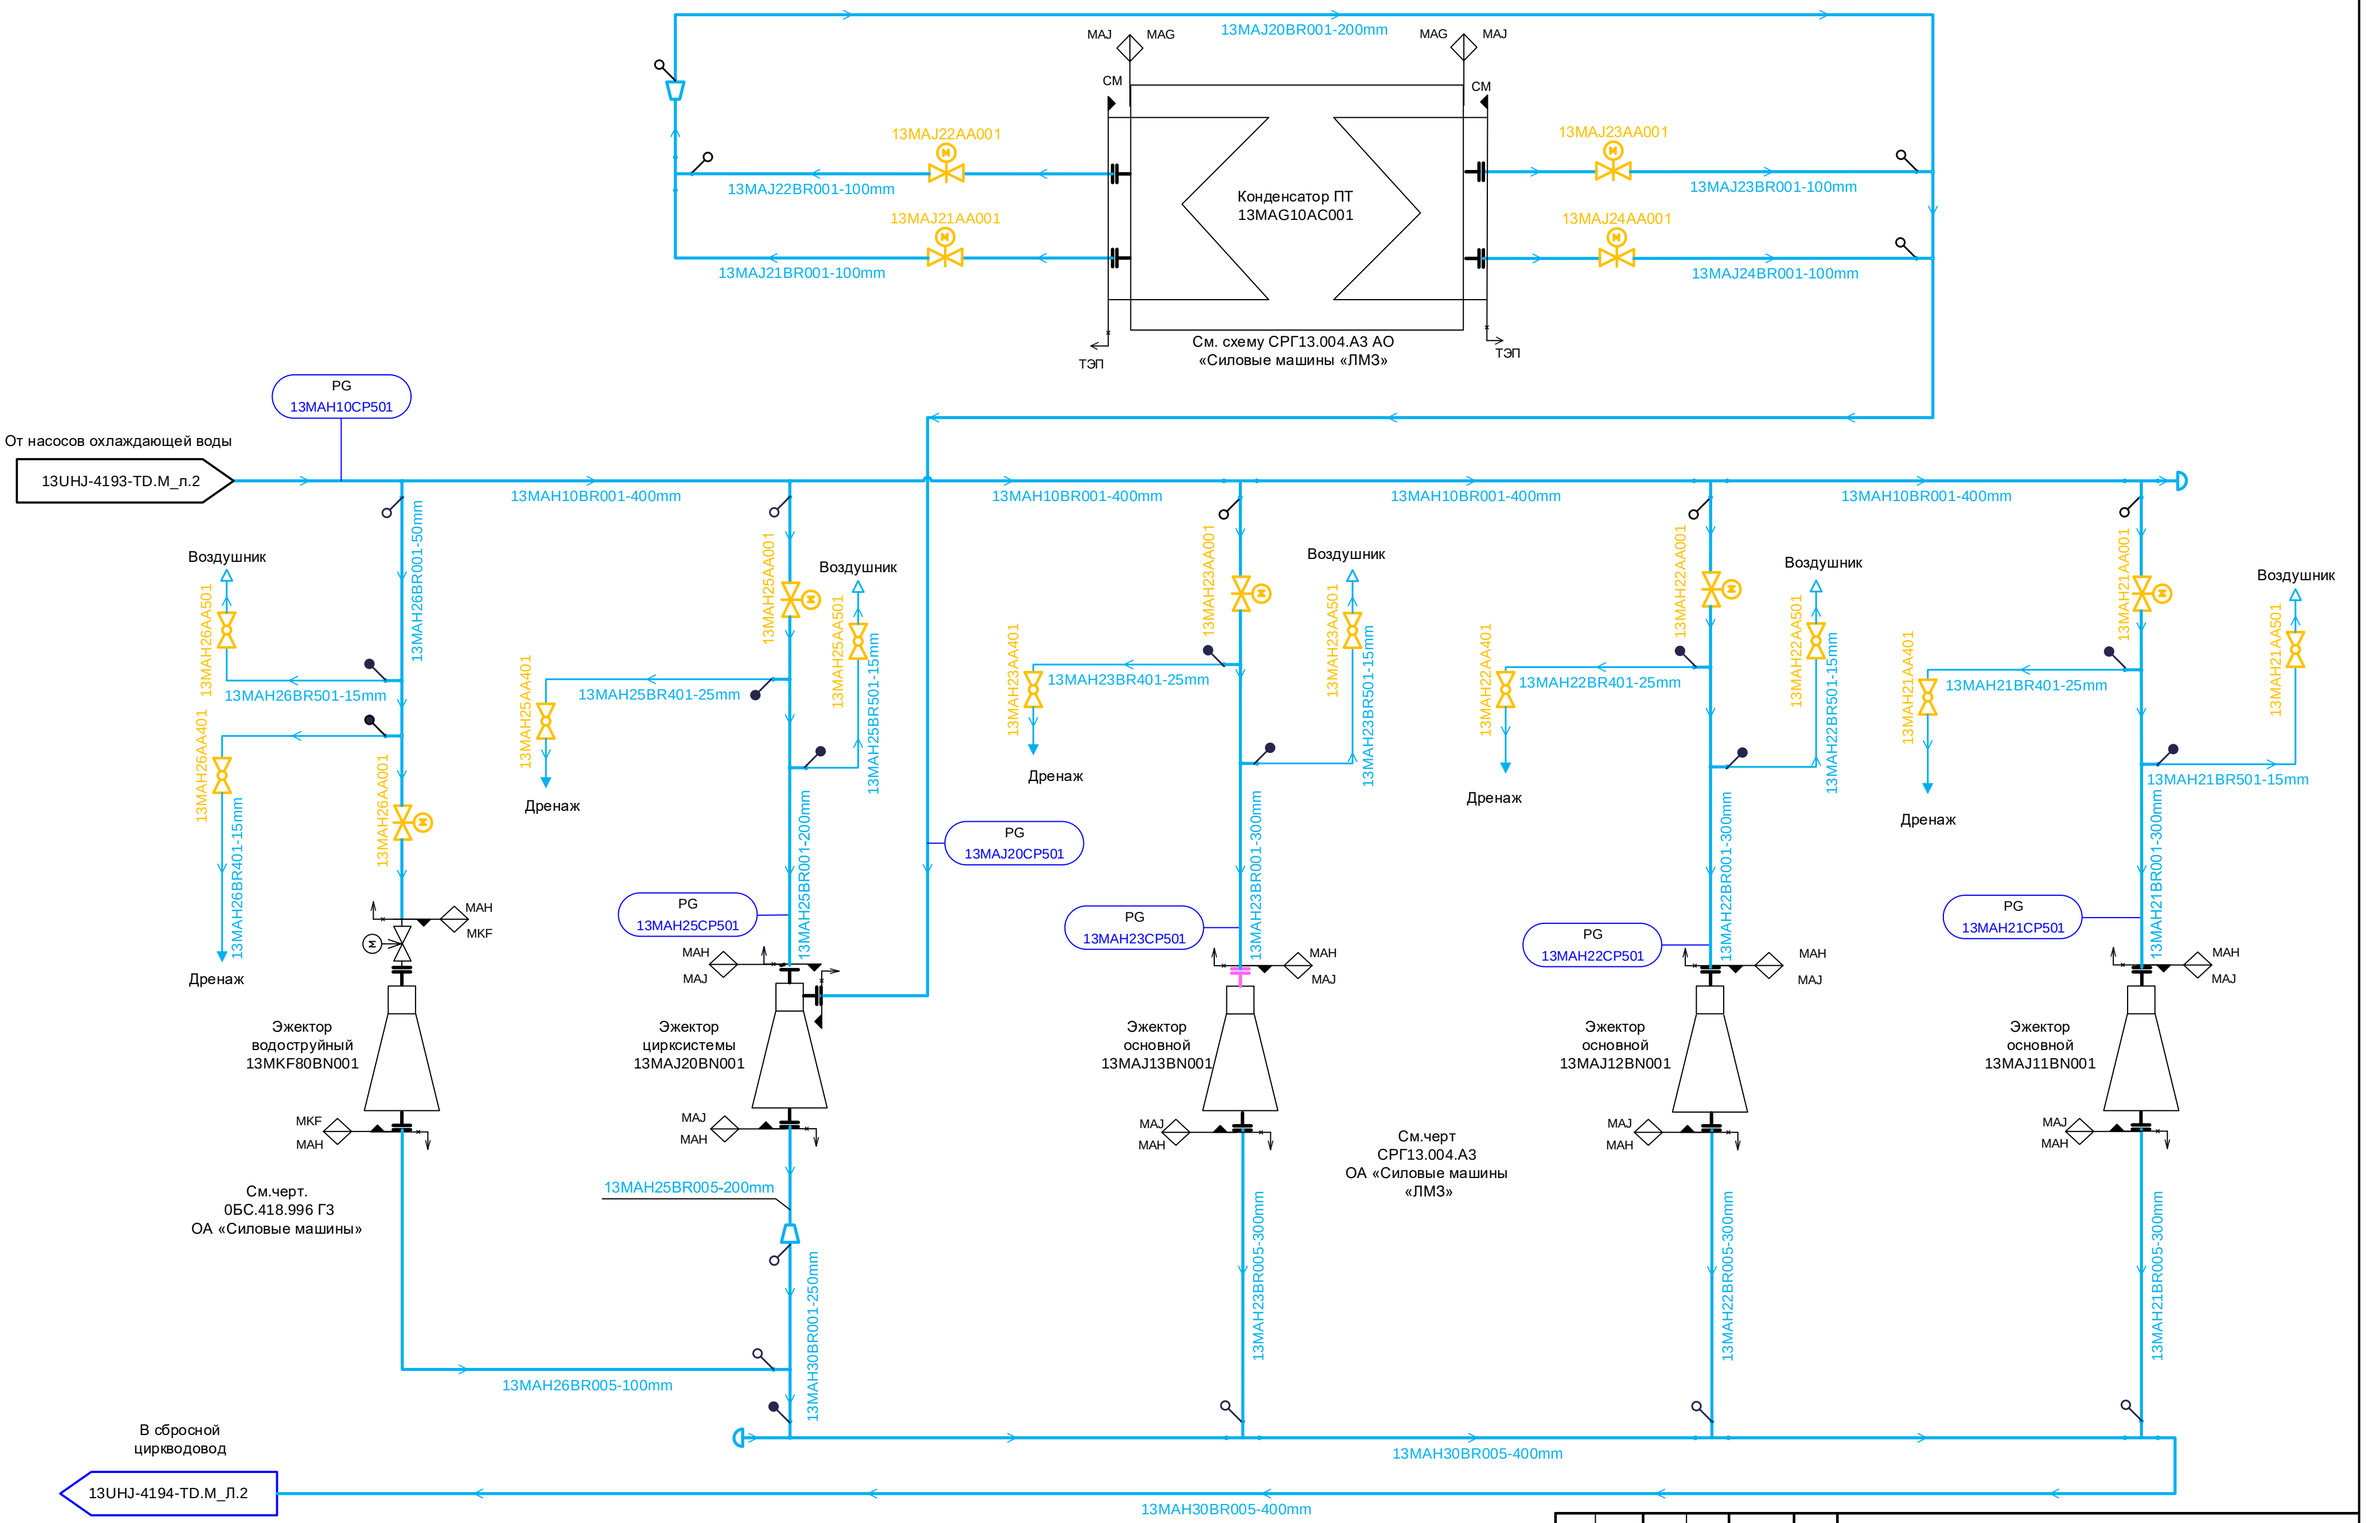

3	-	Зам.	1936-24		07.24	
Изм.	Кол.уч	Лист.	№док.	Подп.	Дата.	
Разработал.		Гусев.Т				
Проверил		Демина				
Н. контр.		Астраханцев				

246N1-13UHJ-4193-TD/M

Модернизация генерирующего объекта Сургутская ГРЭС-1(13Г)

Главный корпус. PI-Диаграмма охлаждающей воды вспомогательного оборудования турбоагрегата.

Стадия	Лист	Листов
Р	4	

PI-Диаграмма охлаждающей воды вспомогательного оборудования турбоагрегата. Система MAH,MAJ

АКЦИОНЕРНОЕ ОБЩЕСТВО ИНСТИТУТ ТЕПЛОЭЛЕКТРОПРОЕКТ г. МОСКВА

Согласовано

Взам. инв. №

Подпись и дата

Инв. № подл.

Формат А2