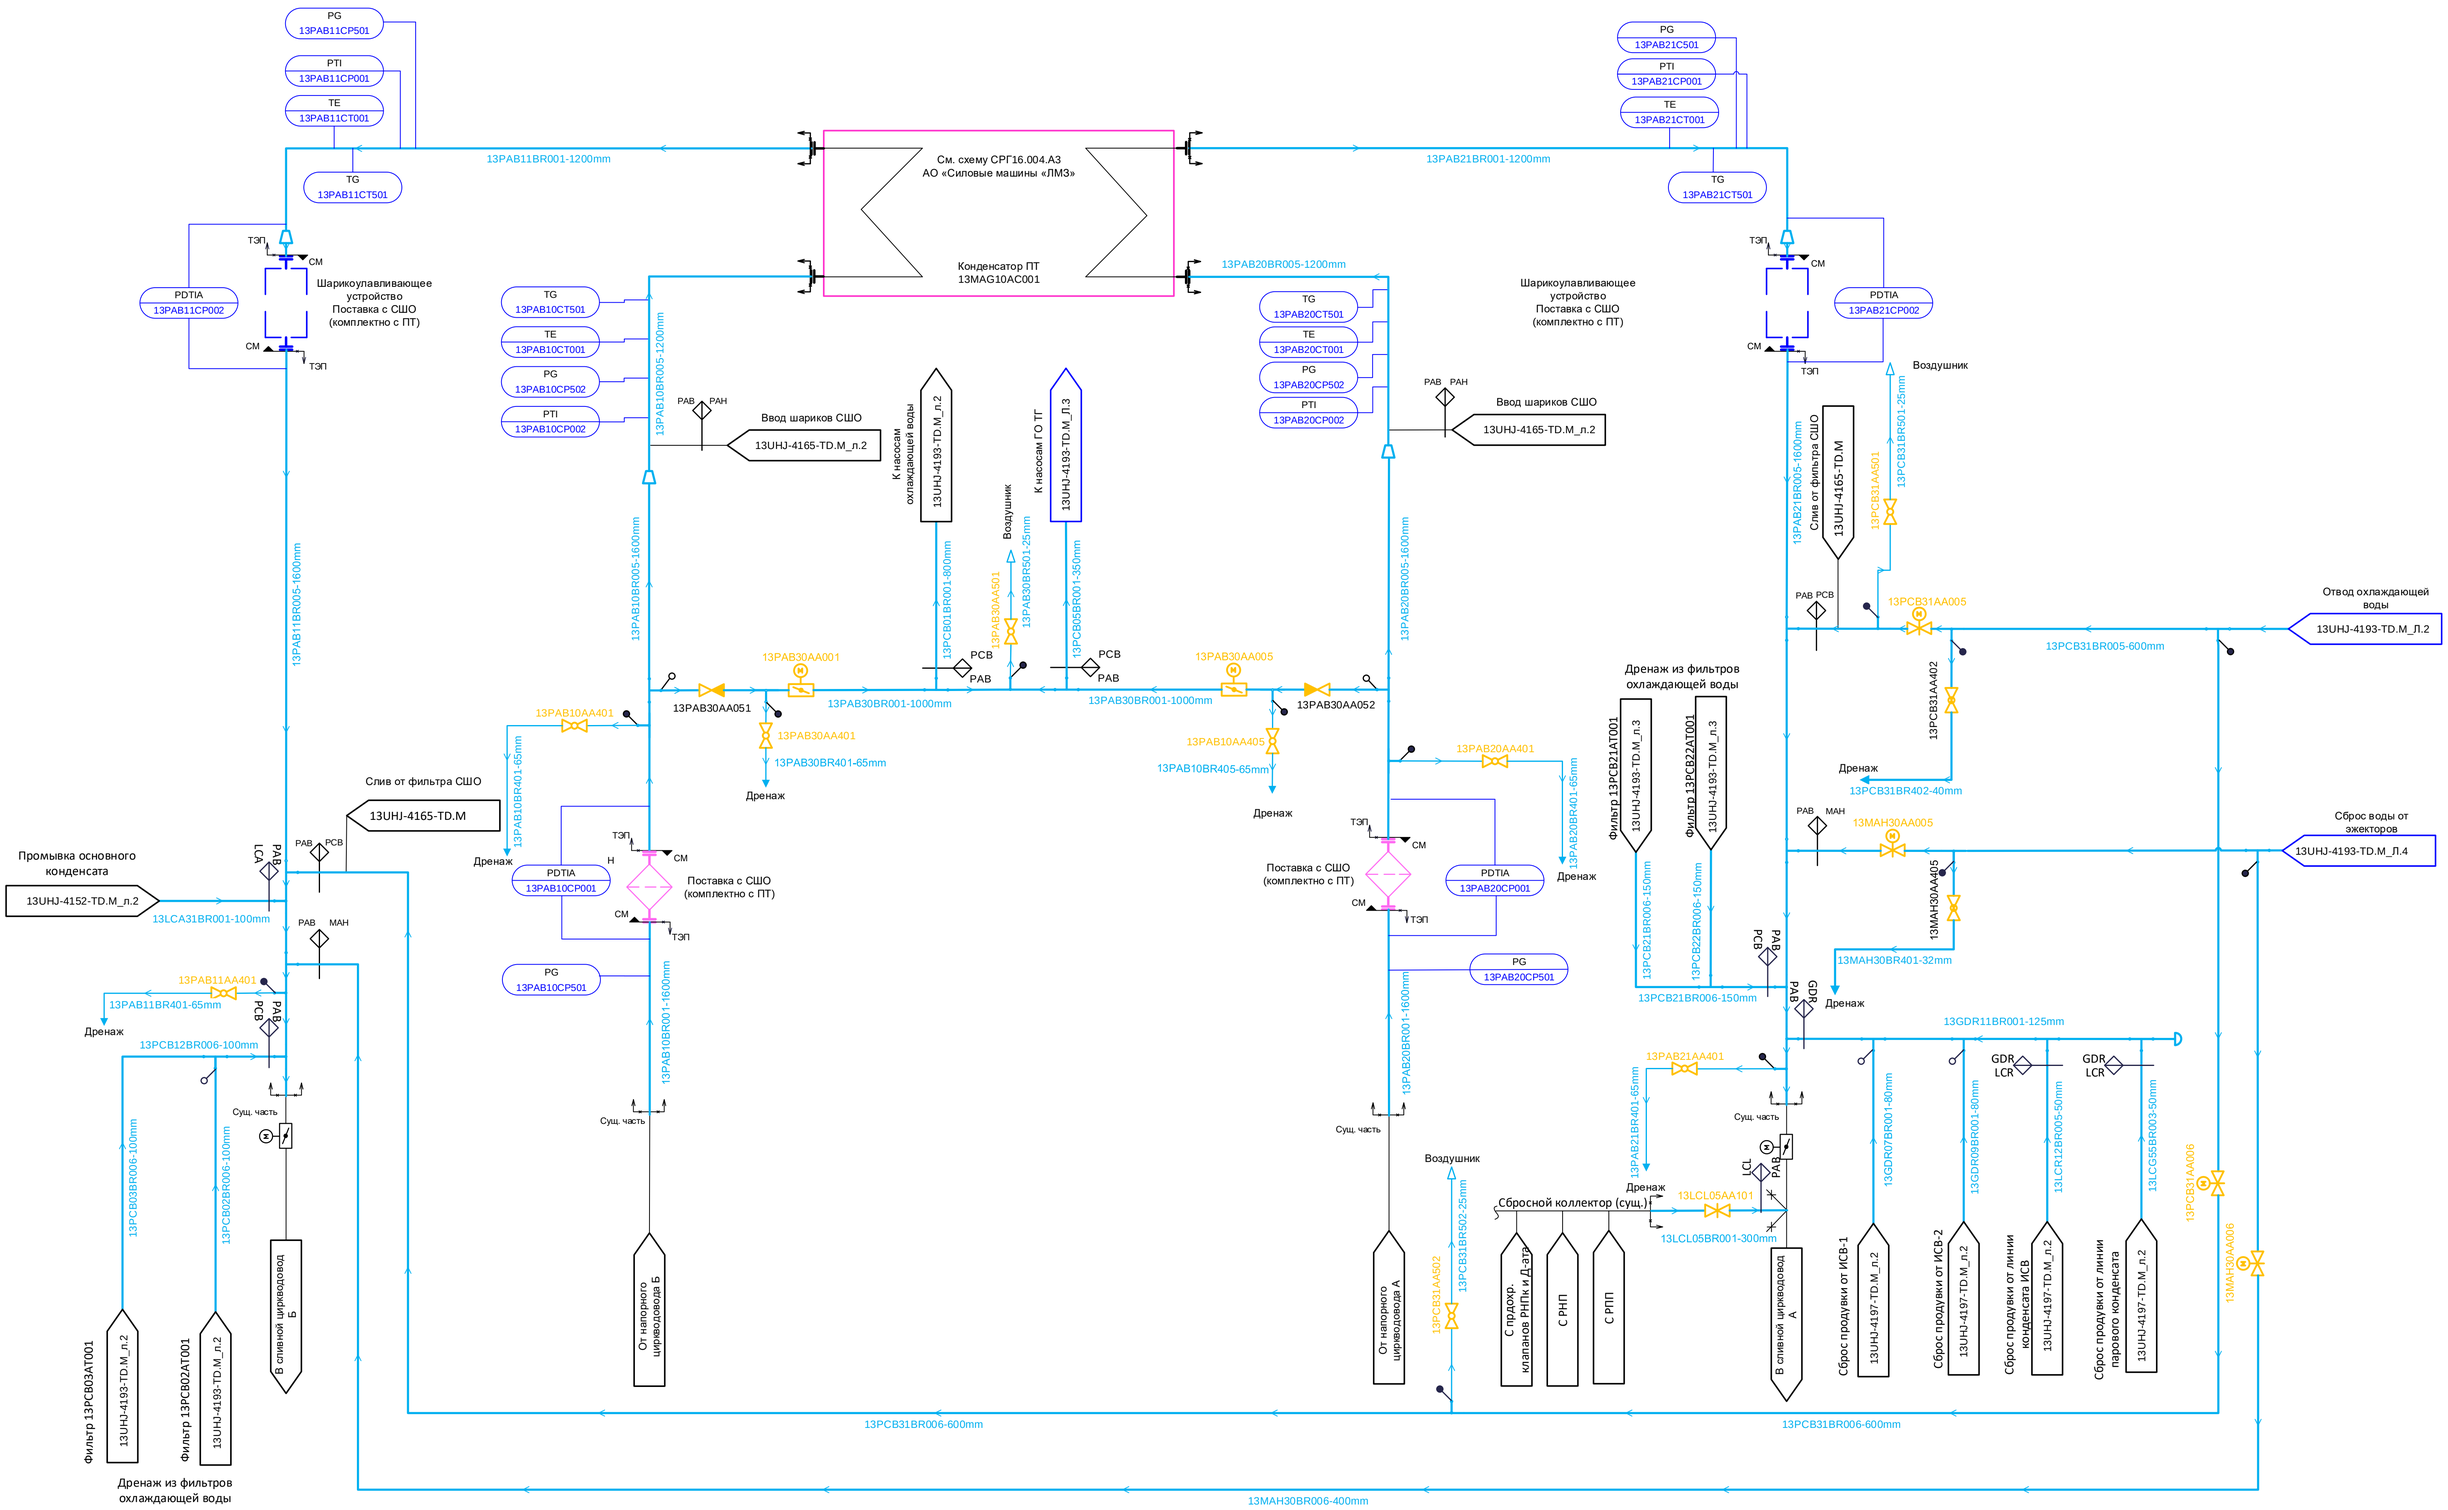

8	-	Зам.	1936-24			
Изм.	Кол.уч	Лист	№ док.	Подп.	Дата	
Разработал		Гусев				
Проверил		Демина				
Н. контр.		Черемушкина				

246N1 – 13UHJ – 4194 – TD.M

Модернизация генерирующего объекта Сургутская ГРЭС-1 (13Г)

PI-диаграмма трубопроводов циркуляционной охлаждающей воды конденсатора турбоагрегата

Стадия	Лист	Листов
Р	2	

PI-диаграмма трубопроводов циркуляционной охлаждающей воды конденсатора турбоагрегата. Система РАВ.

АКЦИОНЕРНОЕ ОБЩЕСТВО ВНИИАМТ ТЕПЛОЭЛЕКТРОПРОЕКТ г. Москва

Согласовано

Согласовано Соболева

Взам. инв. №

Подпись и дата

Инв. № подл.

Формат А1