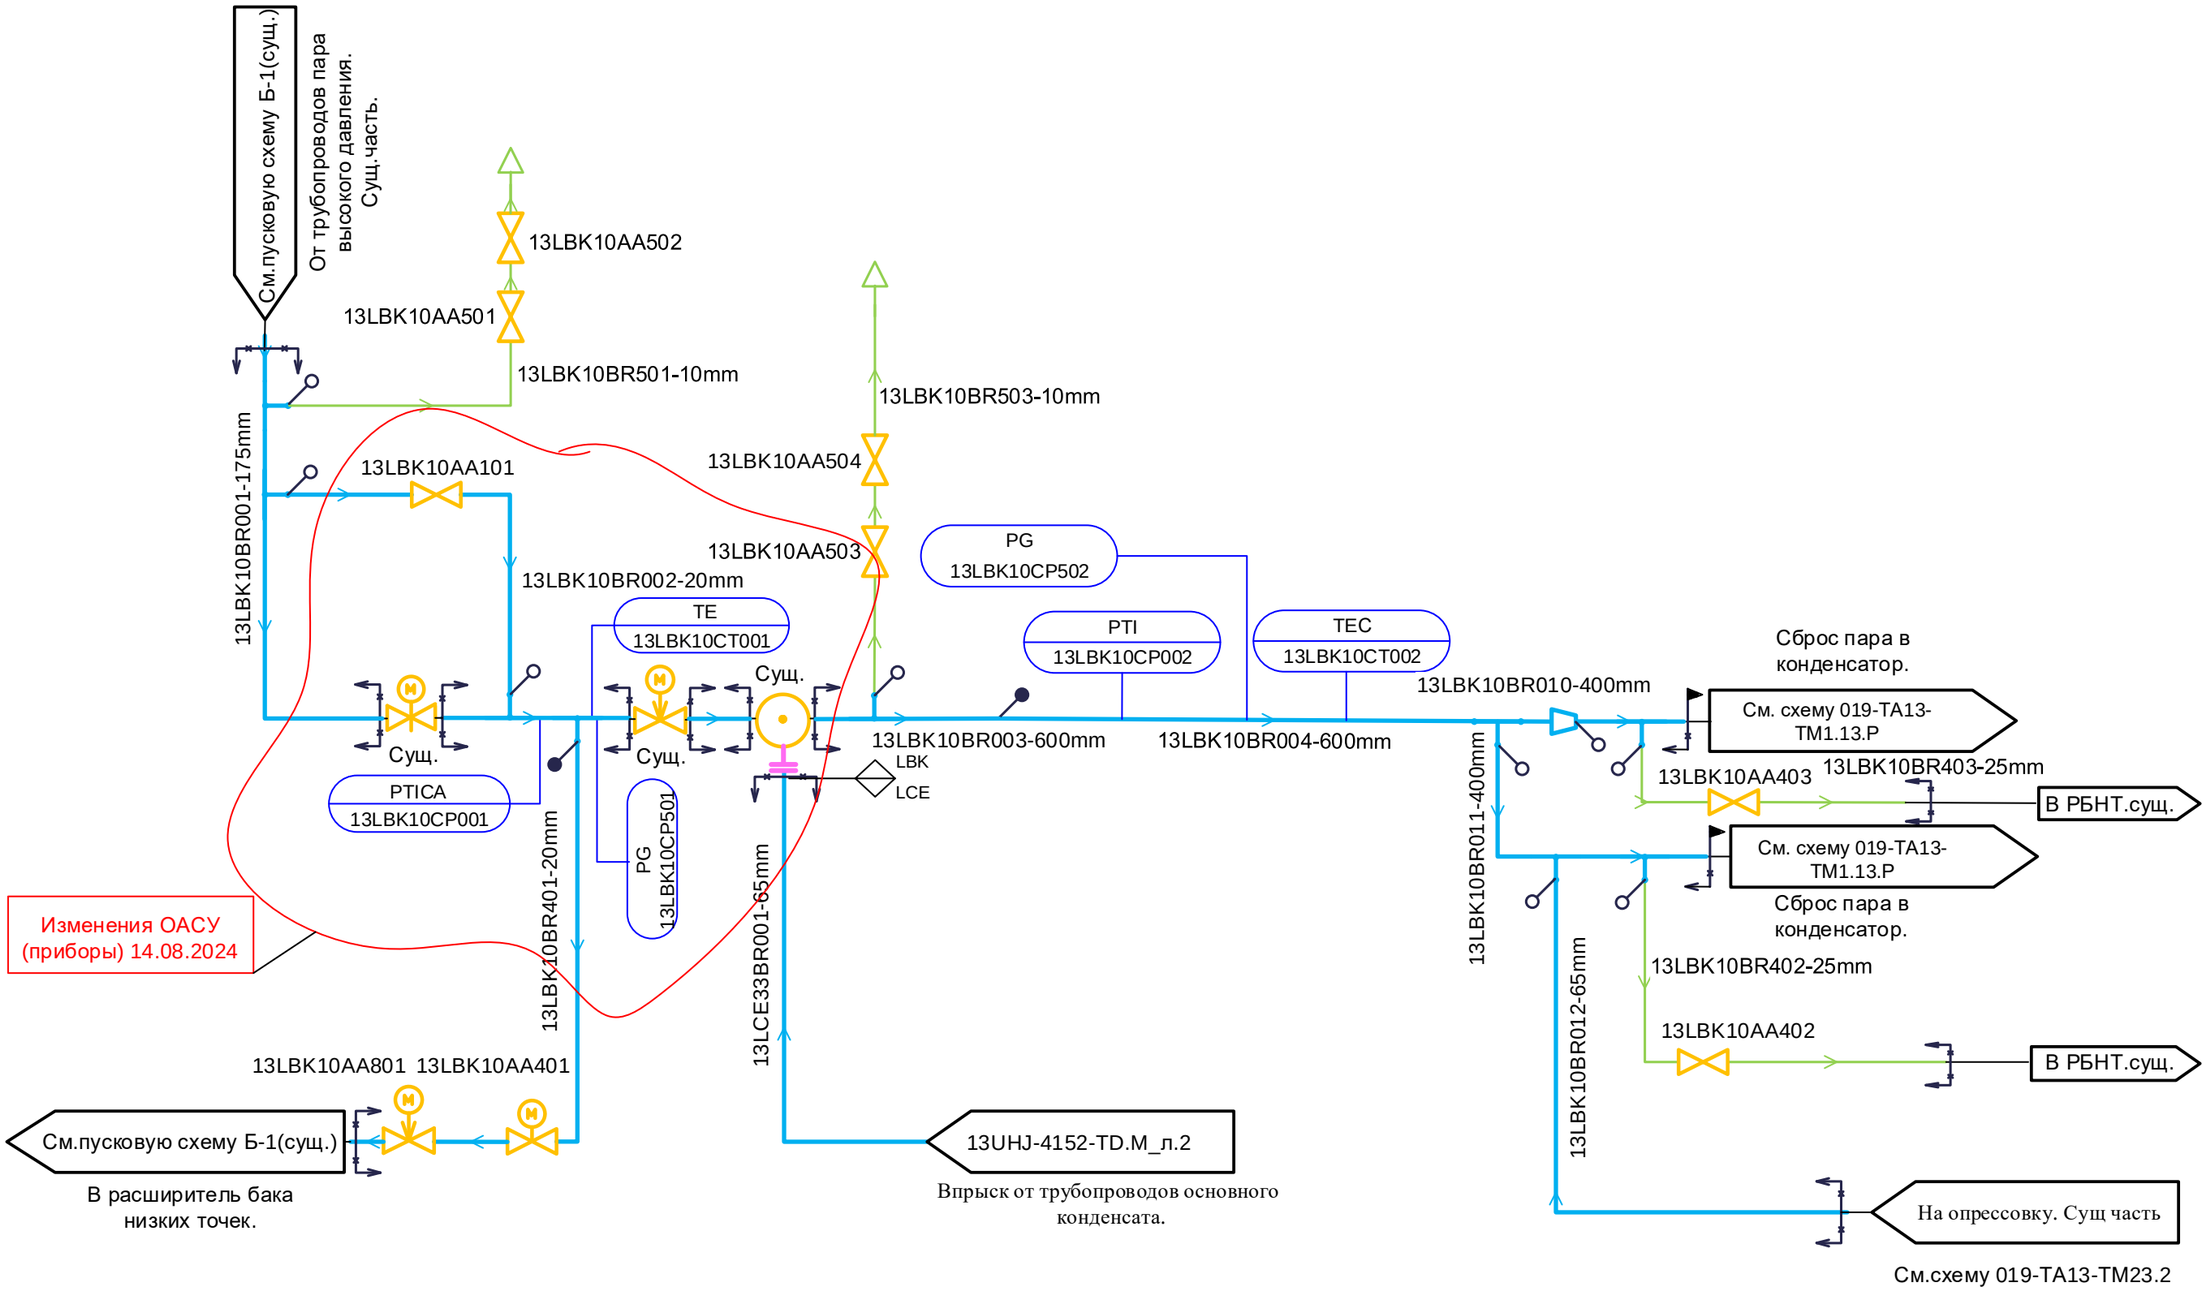

ТЭП

Граница проектирования Сущ./ТЭП

СМ.

Граница проектирования СМ./ТЭП

Примечание: Границы арматуры уточнить по наличию.

1	-	Зам.	564-24			
Изм.	Кол.уч	Лист	№ док.	Подп.	Дата	
Разработал		Гусев.Т				
Проверил		Демина				
Н. контр.		Черемушкина				

246N1-13UHJ-4196-TD.M

Сургутская ГРЭС-1

PI-Диаграмма трубопроводов БРОУ

Стадия	Лист	Листов
Р	2	

PI-Диаграмма трубопроводов БРОУ.Система:LBK,LCE.

АКЦИОНЕРНОЕ ОБЩЕСТВО ИНСТИТУТ ТЕПЛОЭЛЕКТРОПРОЕКТ Г. МОСКВА

Согласовано

Взам. инв. №

Подпись и дата

Инв. № подл.

Формат А3