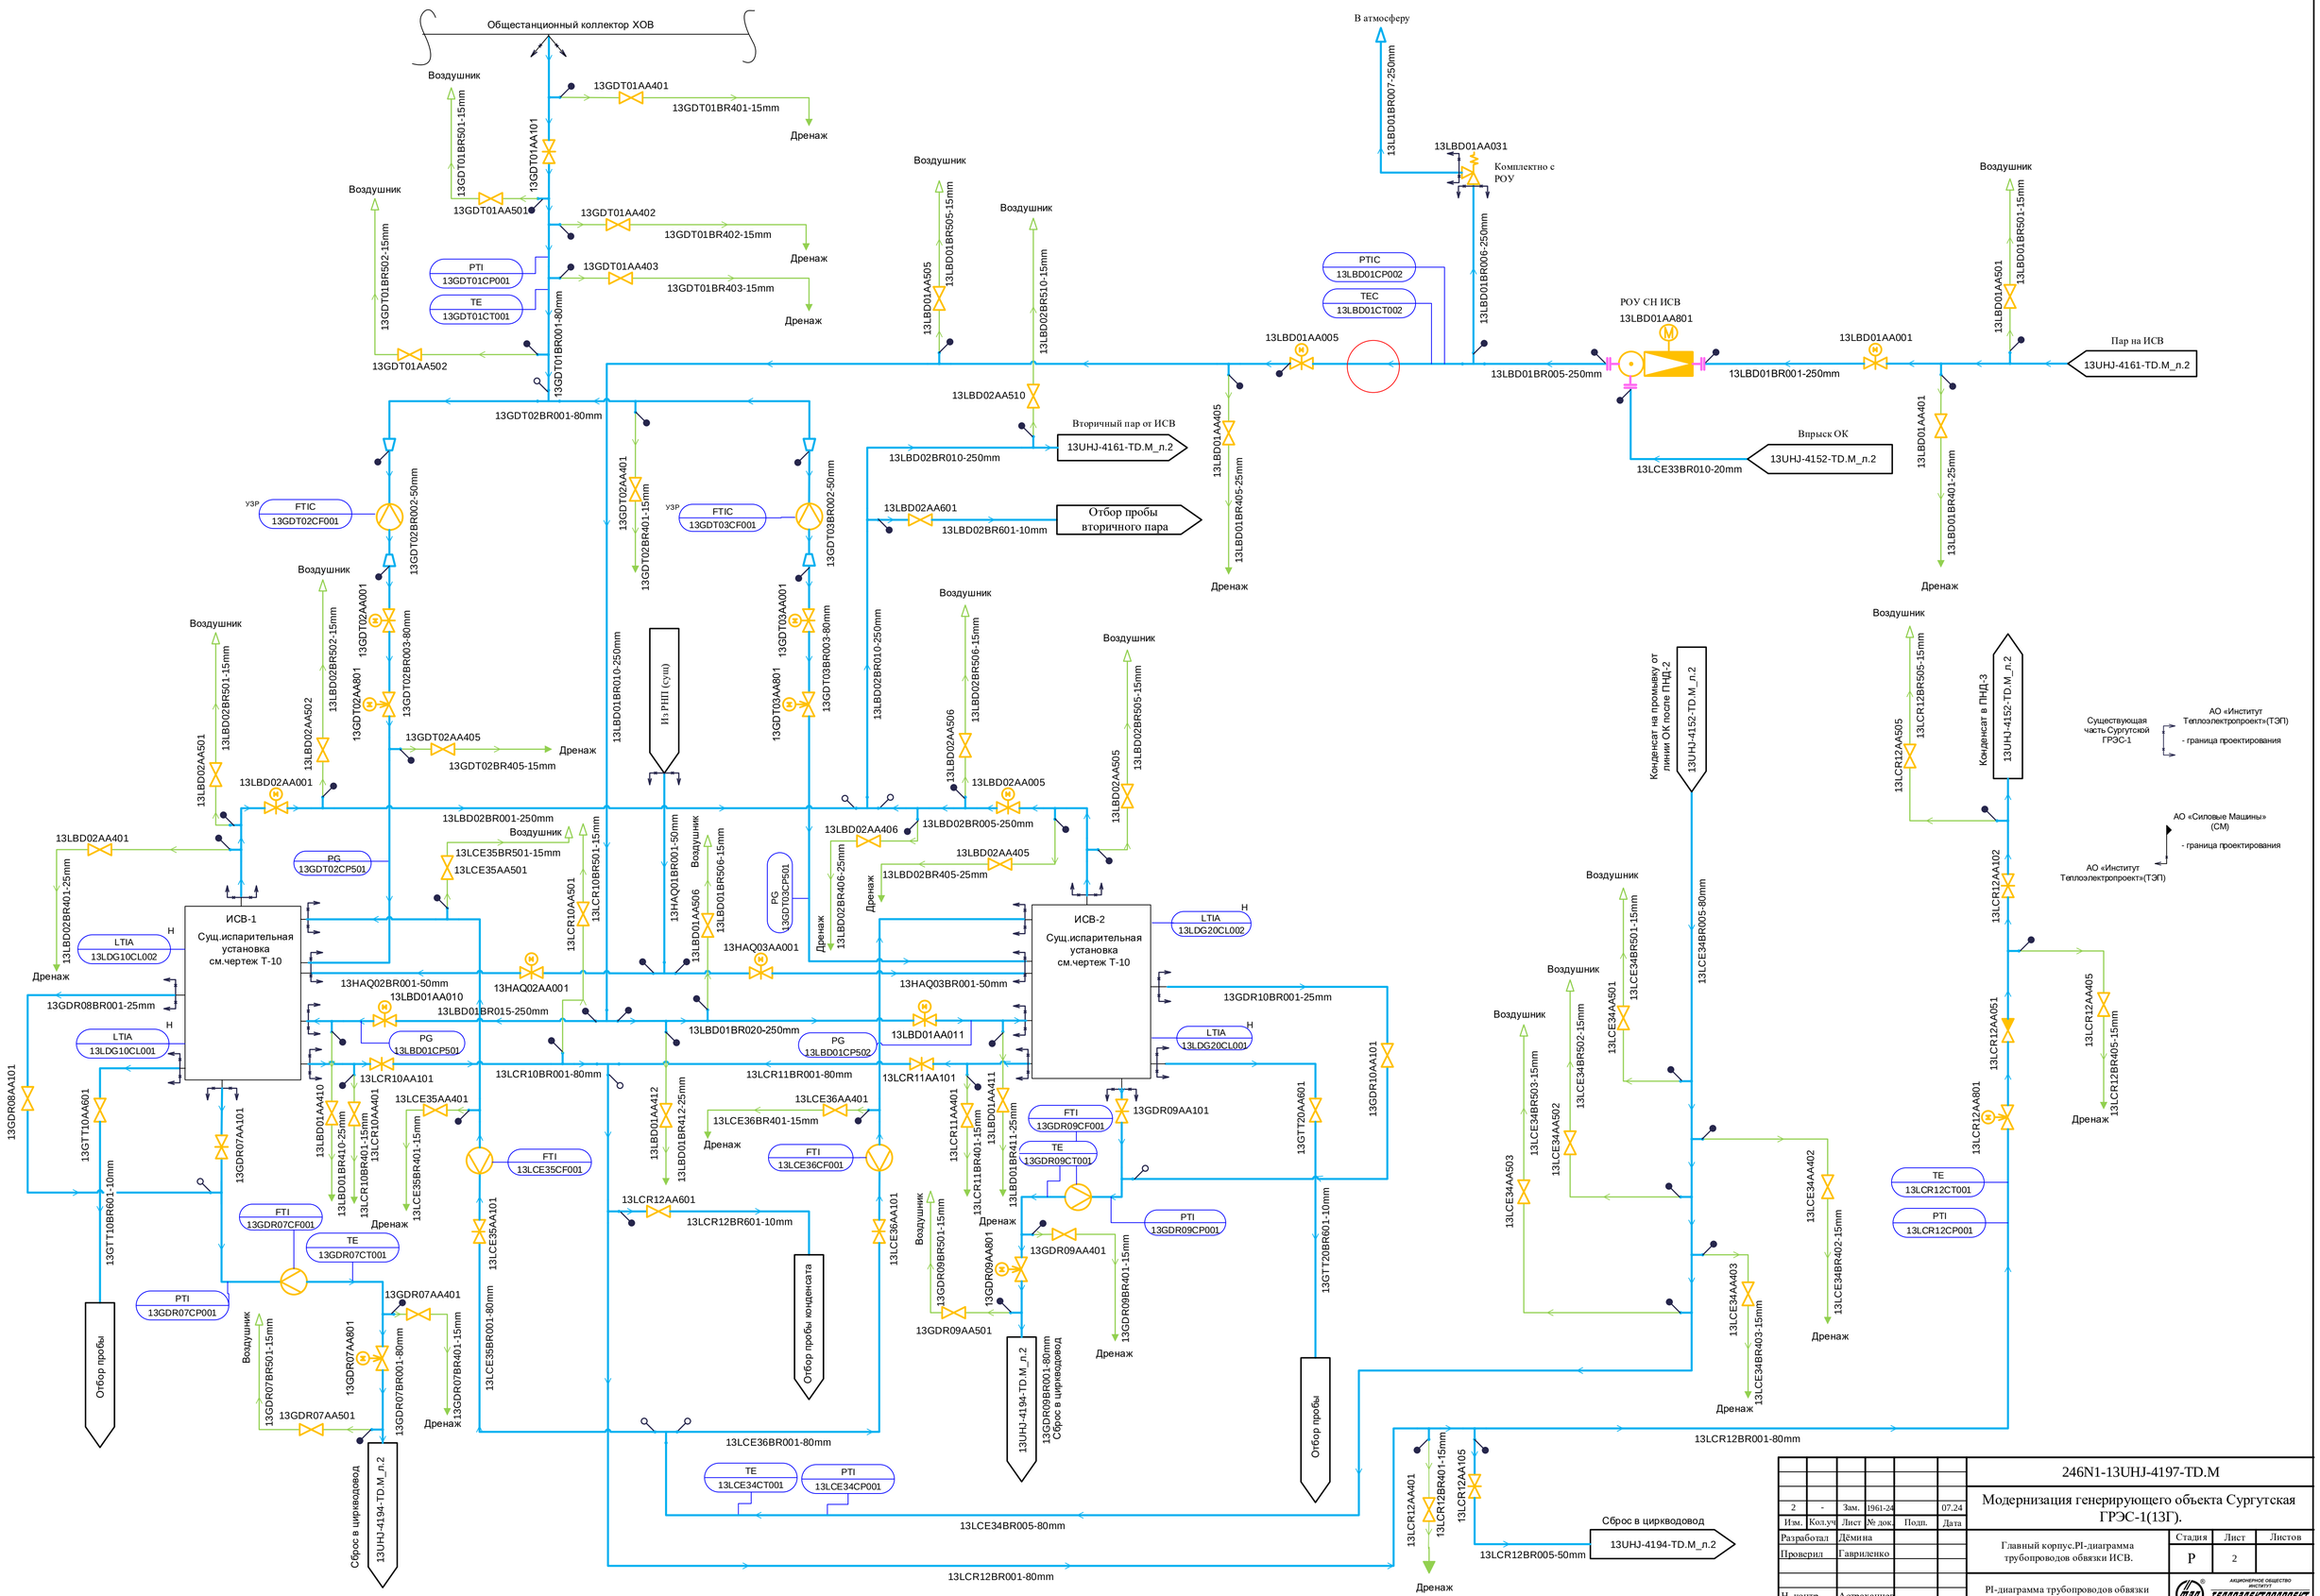

2	-	Зам.	1961-24		07.24	
Изм.	Кол.уч	Лист	№ док.	Подп.	Дата	
Разработал		Дёмина				
Проверил		Гавриленко				
Н. контр.		Астраханцев				

246N1-13UHJ-4197-TD.M

Модернизация генерирующего объекта Сургутская ГРЭС-1(13Г).

Главный корпус.PI-диаграмма трубопроводов обвязки ИСВ.

PI-диаграмма трубопроводов обвязки ИСВ. Система LBD,GDT,LCJ,LCR.

Стадия	Лист	Листов
Р	2	

АКЦИОНЕРНОЕ ОБЩЕСТВО ИНСТИТУТ ТЕПЛОЭЛЕКТРОПРОЕКТ г. МОСКВА

Согласовано

Взам. инв. №

Подпись и дата

Инв. № подл.

Формат А1