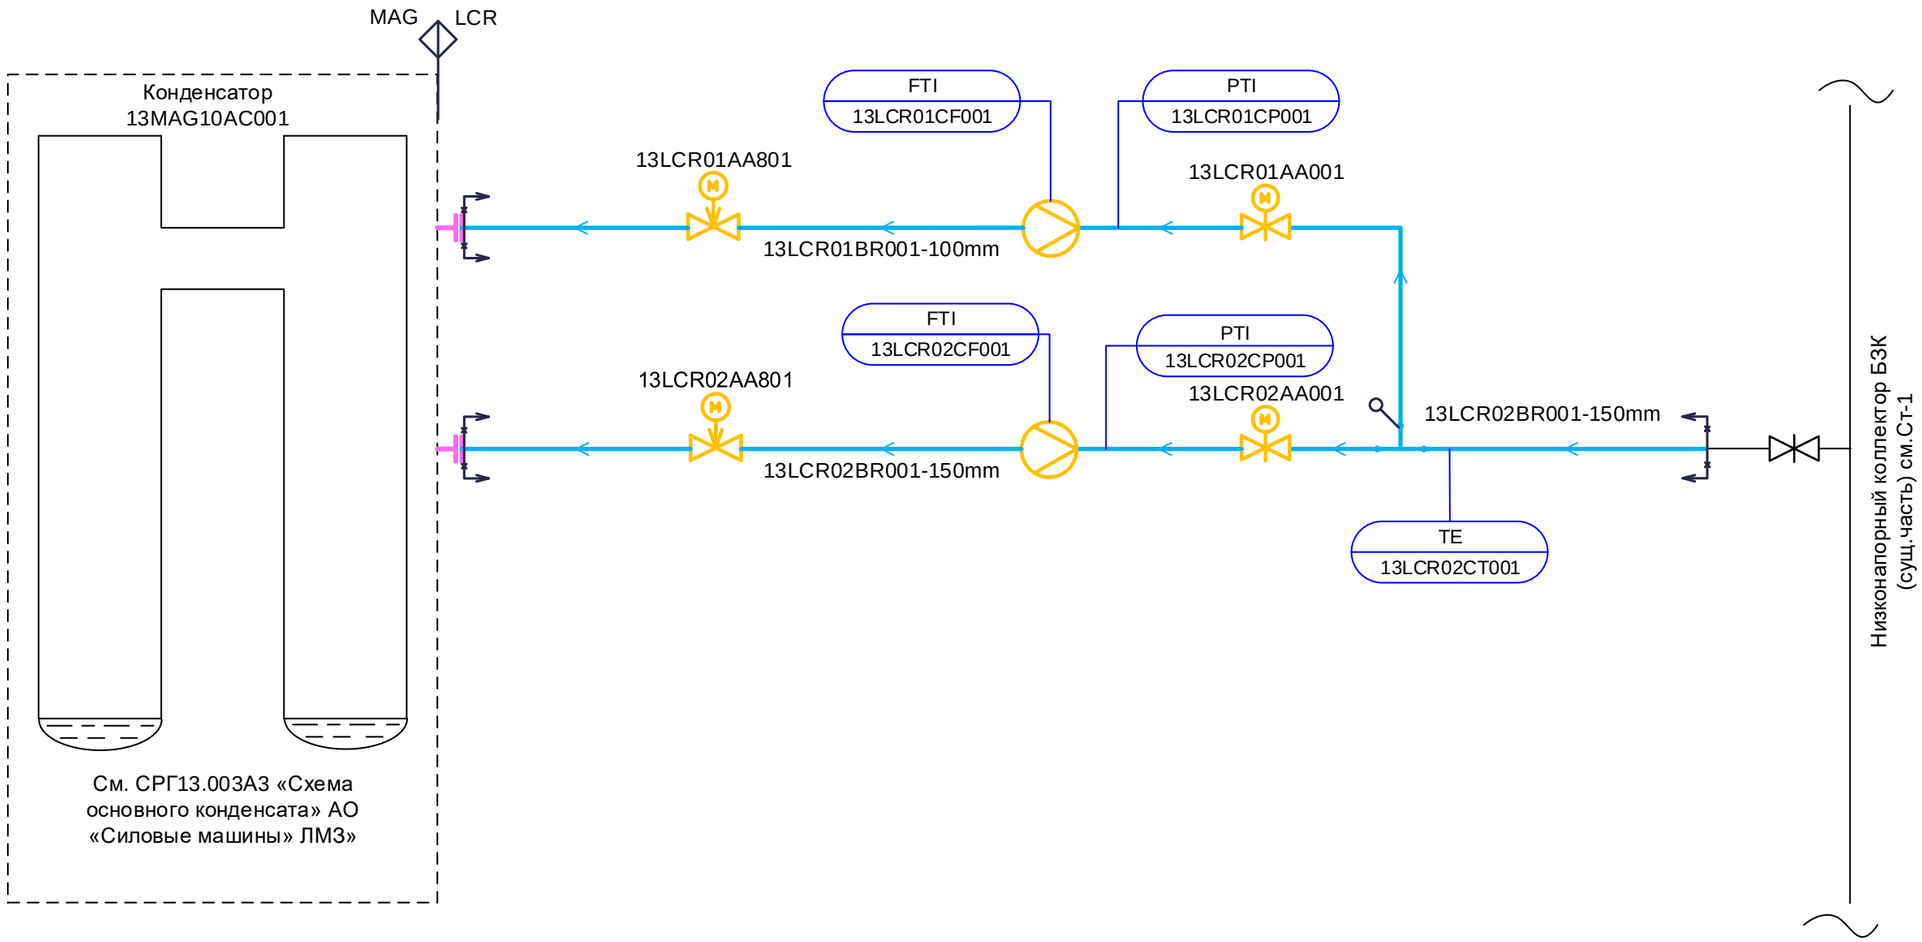

1. Задвижка 13LCR01AA001 на линии постоянного добавка обессоленной воды открывается автоматически при начале открытия РК 13LCR01AA801, закрытие автоматически после полного закрытия РК 13LCR01AA801 с выдержкой времени 20с.
2. Задвижка 13LCR02AA001 на линии аварийного добавка обессоленной воды открывается автоматически при начале открытия РК 13LCR02AA801, закрытие автоматически после полного закрытия РК 13LCR02AA801 с выдержкой времени 20с.
1. Регулирующие клапаны расхода постоянного и аварийного добавка 13LCR01AA801, 13LCR02AA801 управляются оператором дистанционно. Задание устанавливается оператором.

Согласовано

Взам. инв. №

Подпись и дата

Инв. № подл.

Изм.	Кол.уч	Лист	№ док.	Подп.	Дата
1	-	Зам.	639-24		

246N1 – 13UHJ – 4198 – TD.M

Модернизация генерирующего объекта Сургутская ГРЭС-1 (13Г)

Разработал	Гусев	
Проверил	Демина	
Н. контр.	Черемушкина	

Главный корпус. PI-диаграмма трубопроводов аварийной и постоянной подпитки конденсатора

Стадия	Лист	Листов
Р	2	

PI-диаграмма трубопроводов аварийной и постоянной подпитки конденсатора. Система LCR

АКЦИОНЕРНОЕ ОБЩЕСТВО ИНСТИТУТ ТЕПЛОЭЛЕКТРОПРОЕКТ Г. МОСКВА

Формат А3