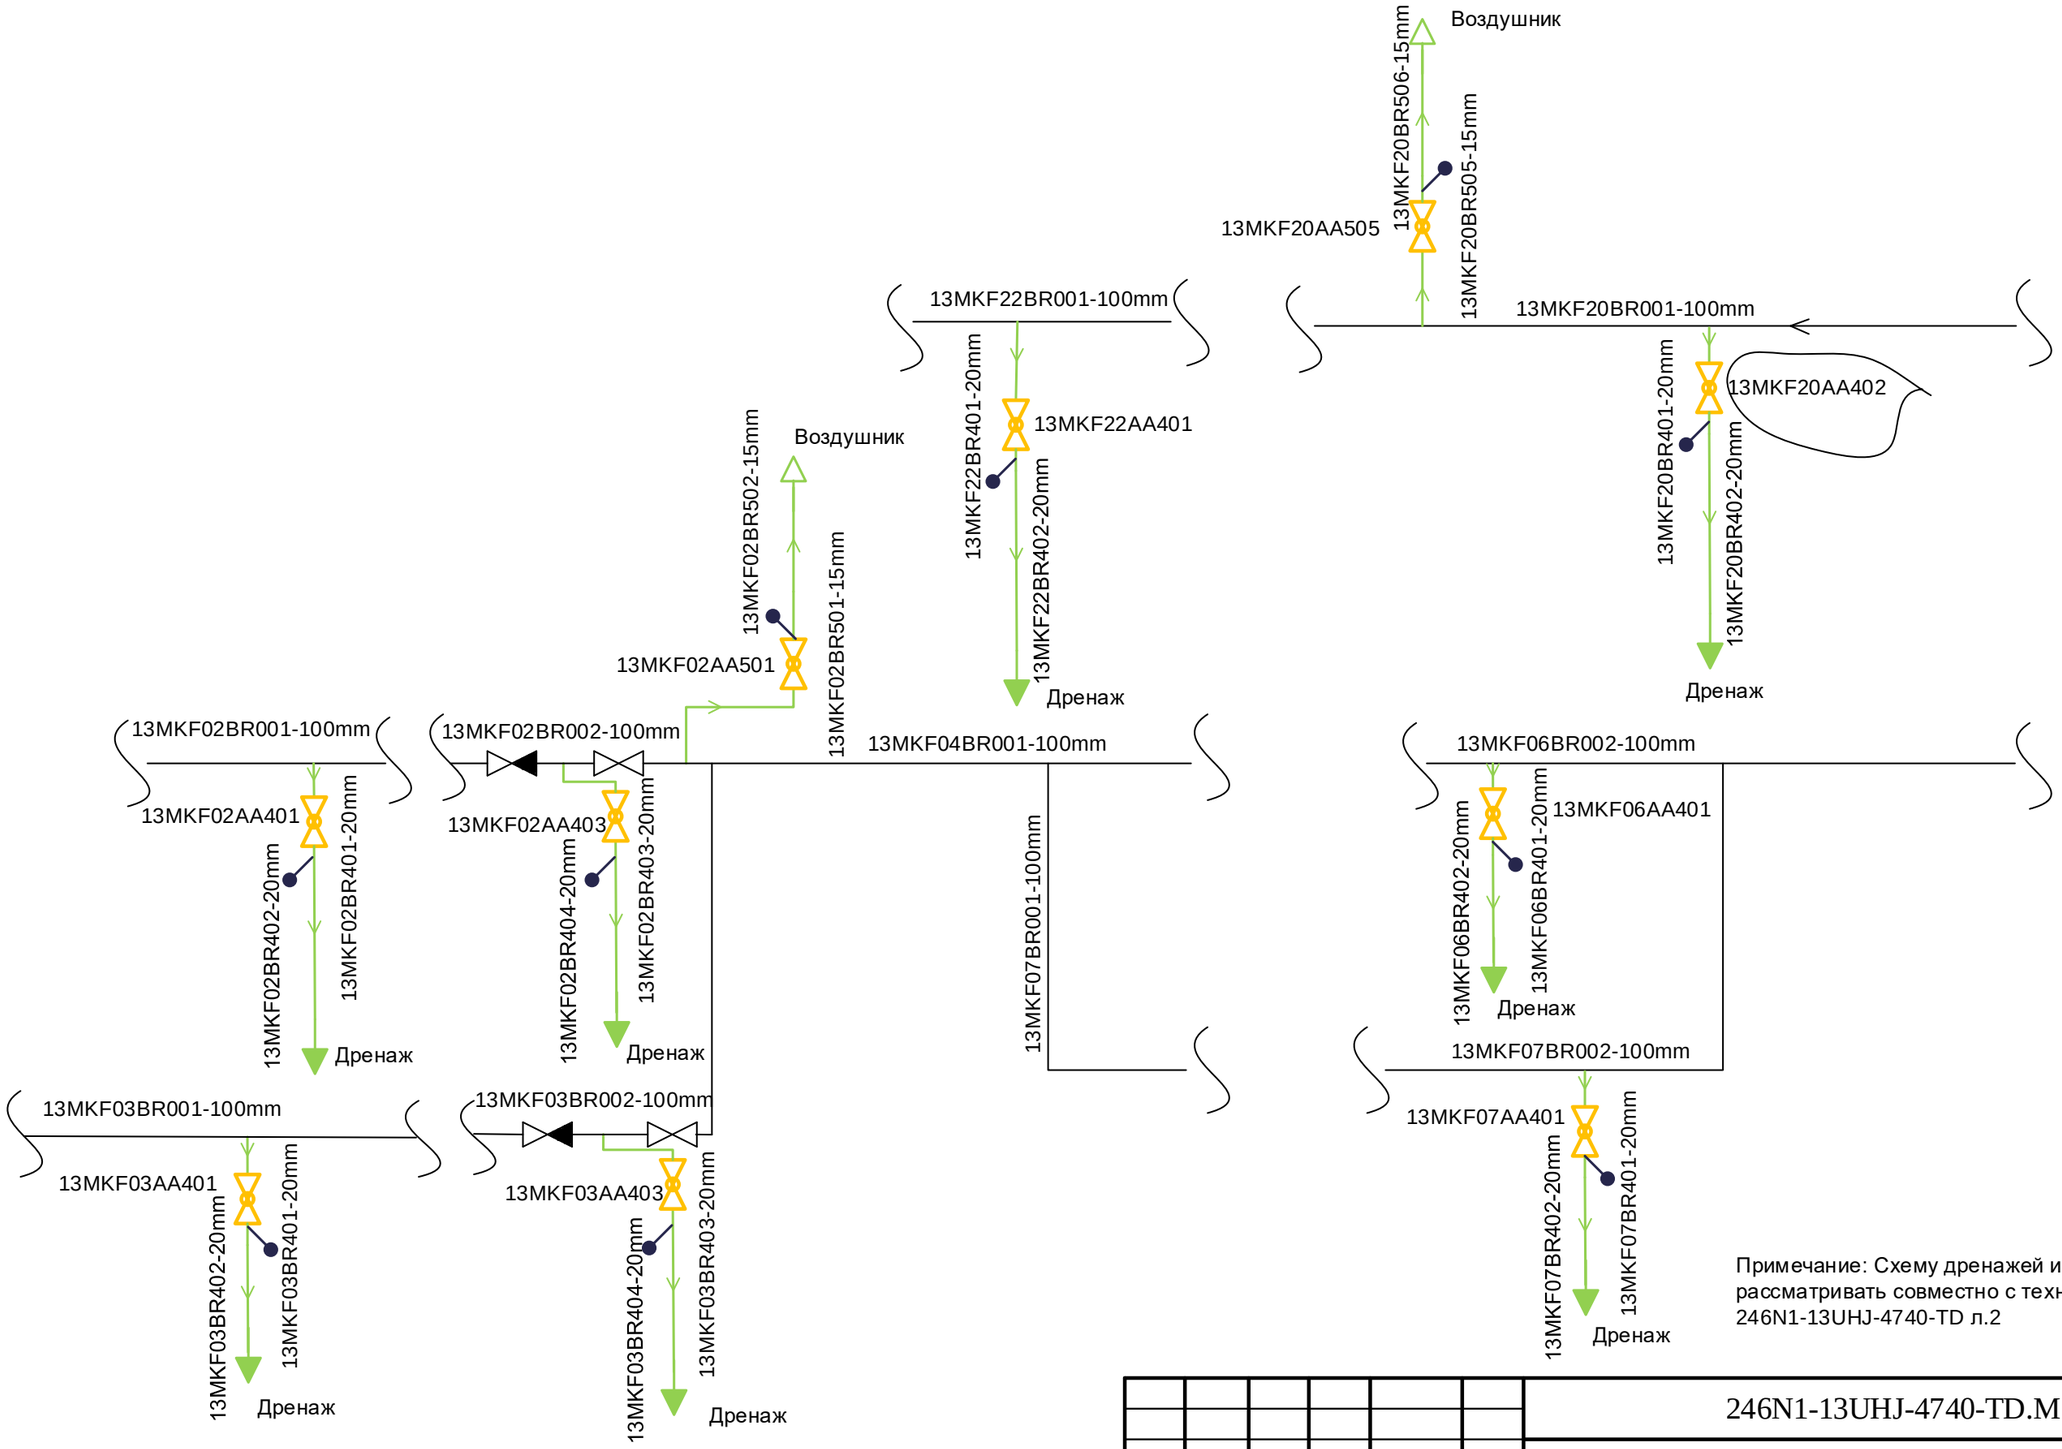

Примечание: Схему дренажей и воздушников рассматривать совместно с технол.схемой 246N1-13UHJ-4740-TD л.2

Согласовано

Взам. инв. №

Подпись и дата

Инв. № подл.

Изм.	Кол.уч	Лист	№ док.	Подп.	Дата
Разработал		Гусев			
Проверил		Ястребов			
Н. контр.		Черемушкина			

246N1-13UHJ-4740-TD.M

Модернизация генерирующего объекта Сургутская ГРЭС-1(13г).

PI-Диаграмма дренажей и воздушников системы охлаждения турбогенератора.

Стадия	Лист	Листов
Р	2	

PI-Диаграмма дренажей и воздушников.

АКЦИОНЕРНОЕ ОБЩЕСТВО ИНСТИТУТ ТЕПЛОЭЛЕКТРОПРОЕКТ Г. МОСКВА

Формат А3