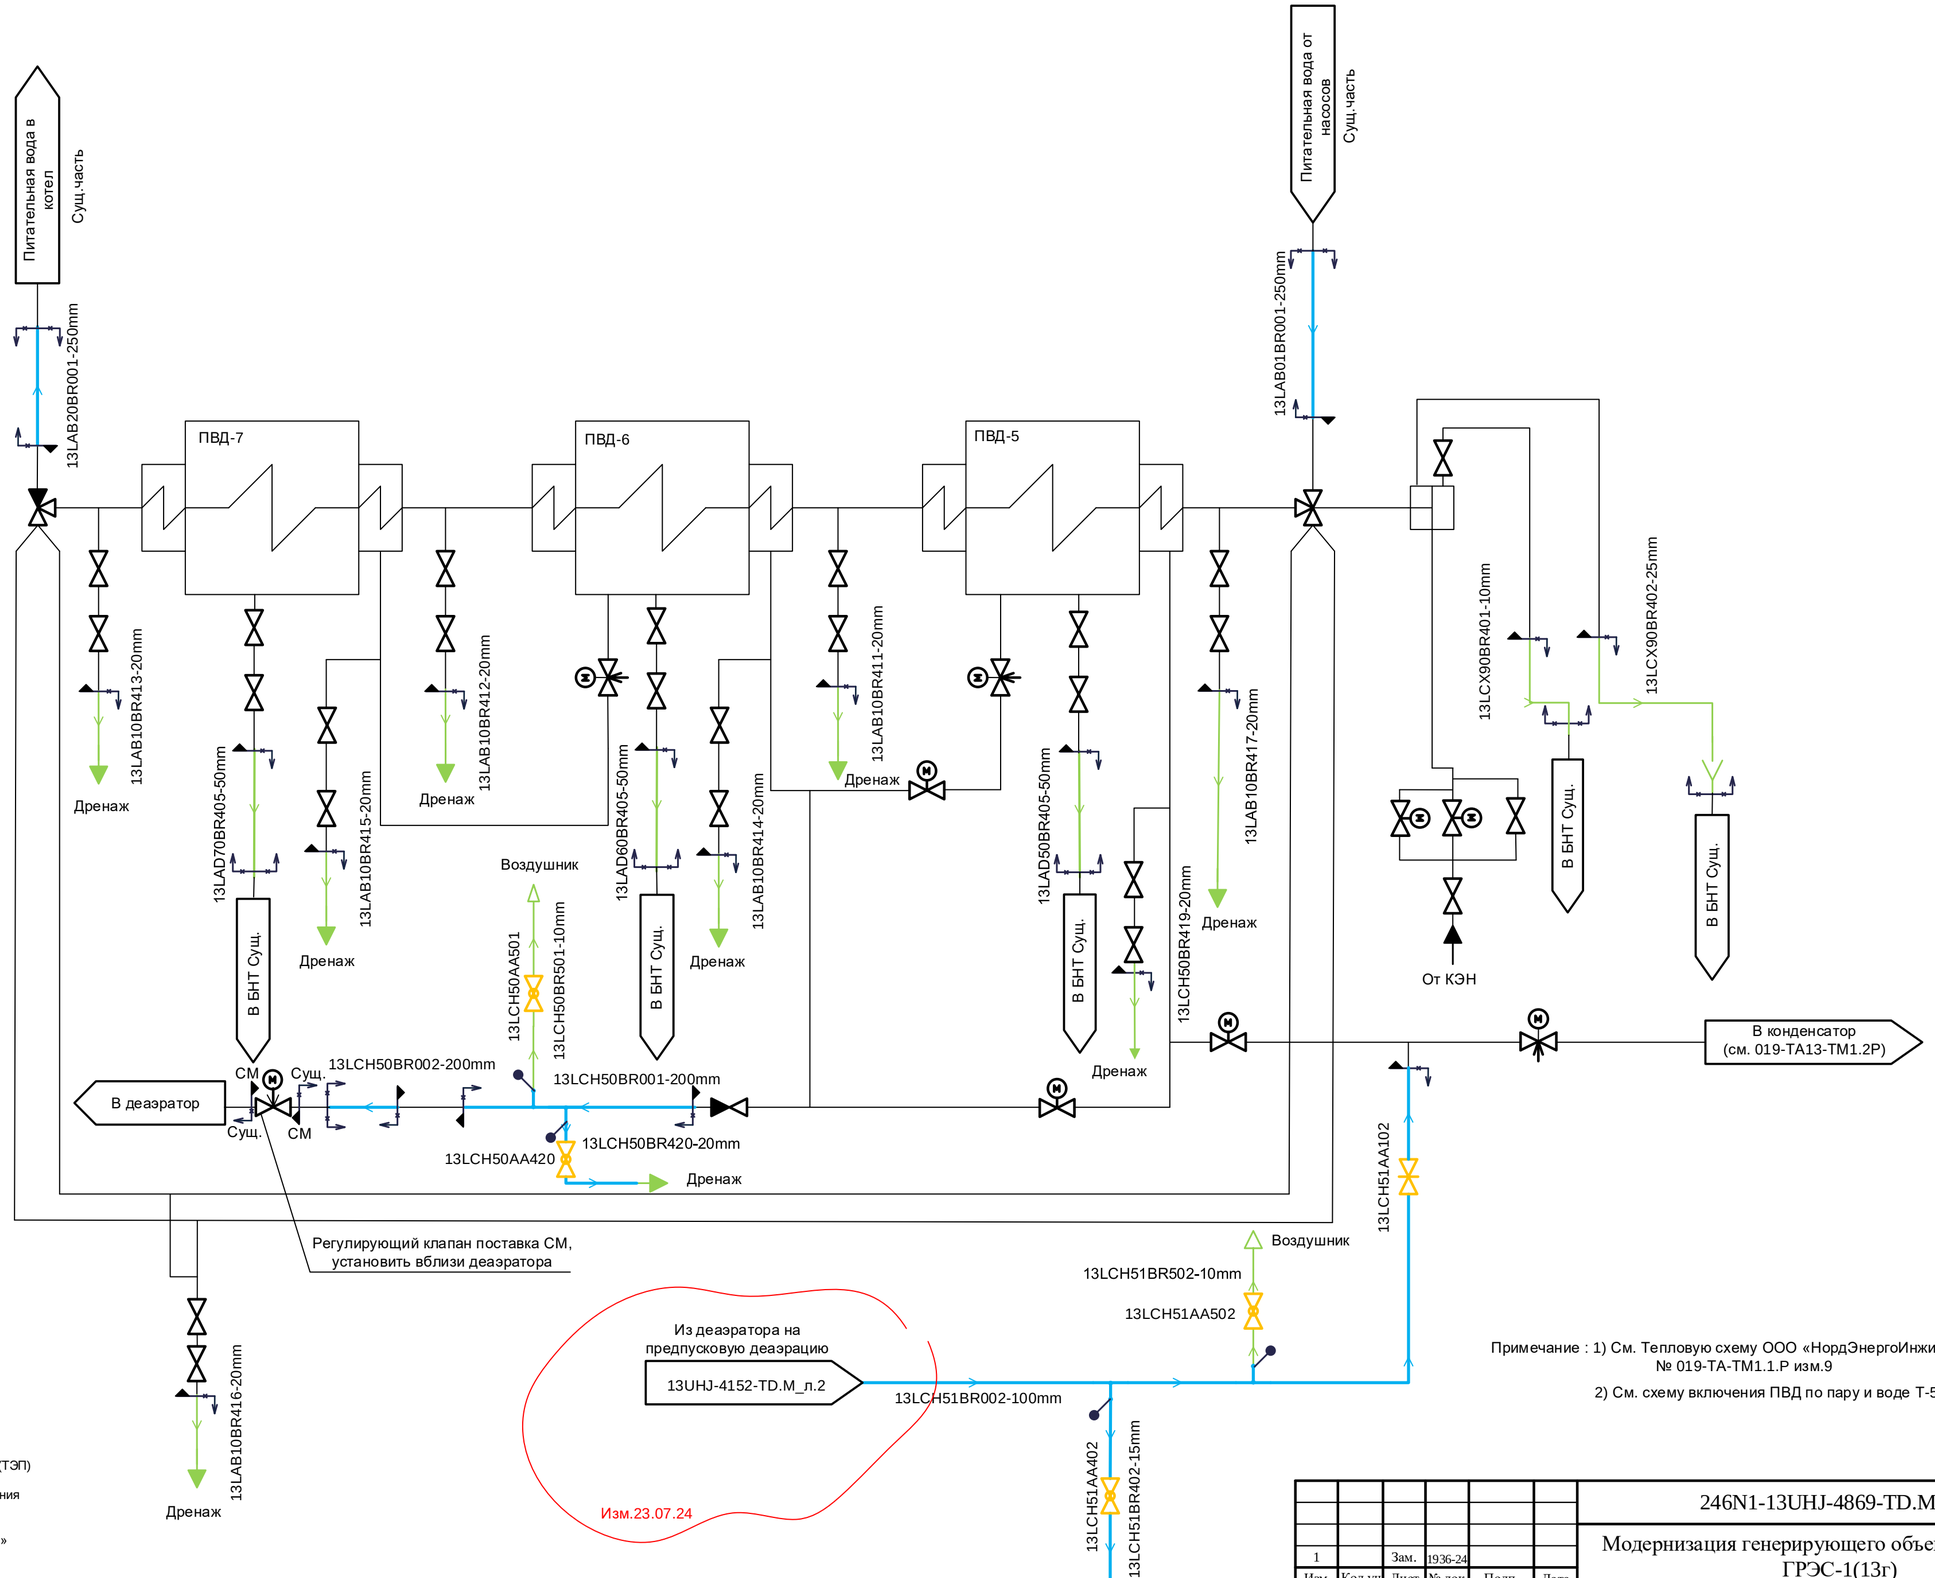

Примечание : 1) См. Тепловую схему ООО «НордЭнергоИнжиниринг» № 019-ТА-ТМ1.1.Р изм.9

2) См. схему включения ПВД по пару и воде Т-5

1		Зам.	1936-24			
Изм.	Кол.уч	Лист	№ док.	Подп.	Дата	
Разработал		Гусев.Т				
Проверил		Демина				
Гл.спец		Гавриленко				
Н. контр.		Черемушкина				

246N1-13UHJ-4869-TD.M

Модернизация генерирующего объекта Сургутская ГРЭС-1(13г)

Главный корпус.
Трубопроводы питательной воды.

Стадия	Лист	Листов
Р	2	

PI-диаграмма
трубопроводов питательной воды.
Система LBH,LAB,LAD,LCX.

АКЦИОНЕРНОЕ ОБЩЕСТВО ИНСТИТУТ ТЕПЛОЭЛЕКТРОПРОЕКТ Г. МОСКВА

Согласовано

Взам. инв. №

Подпись и дата

Инв. № подл.

Формат А2