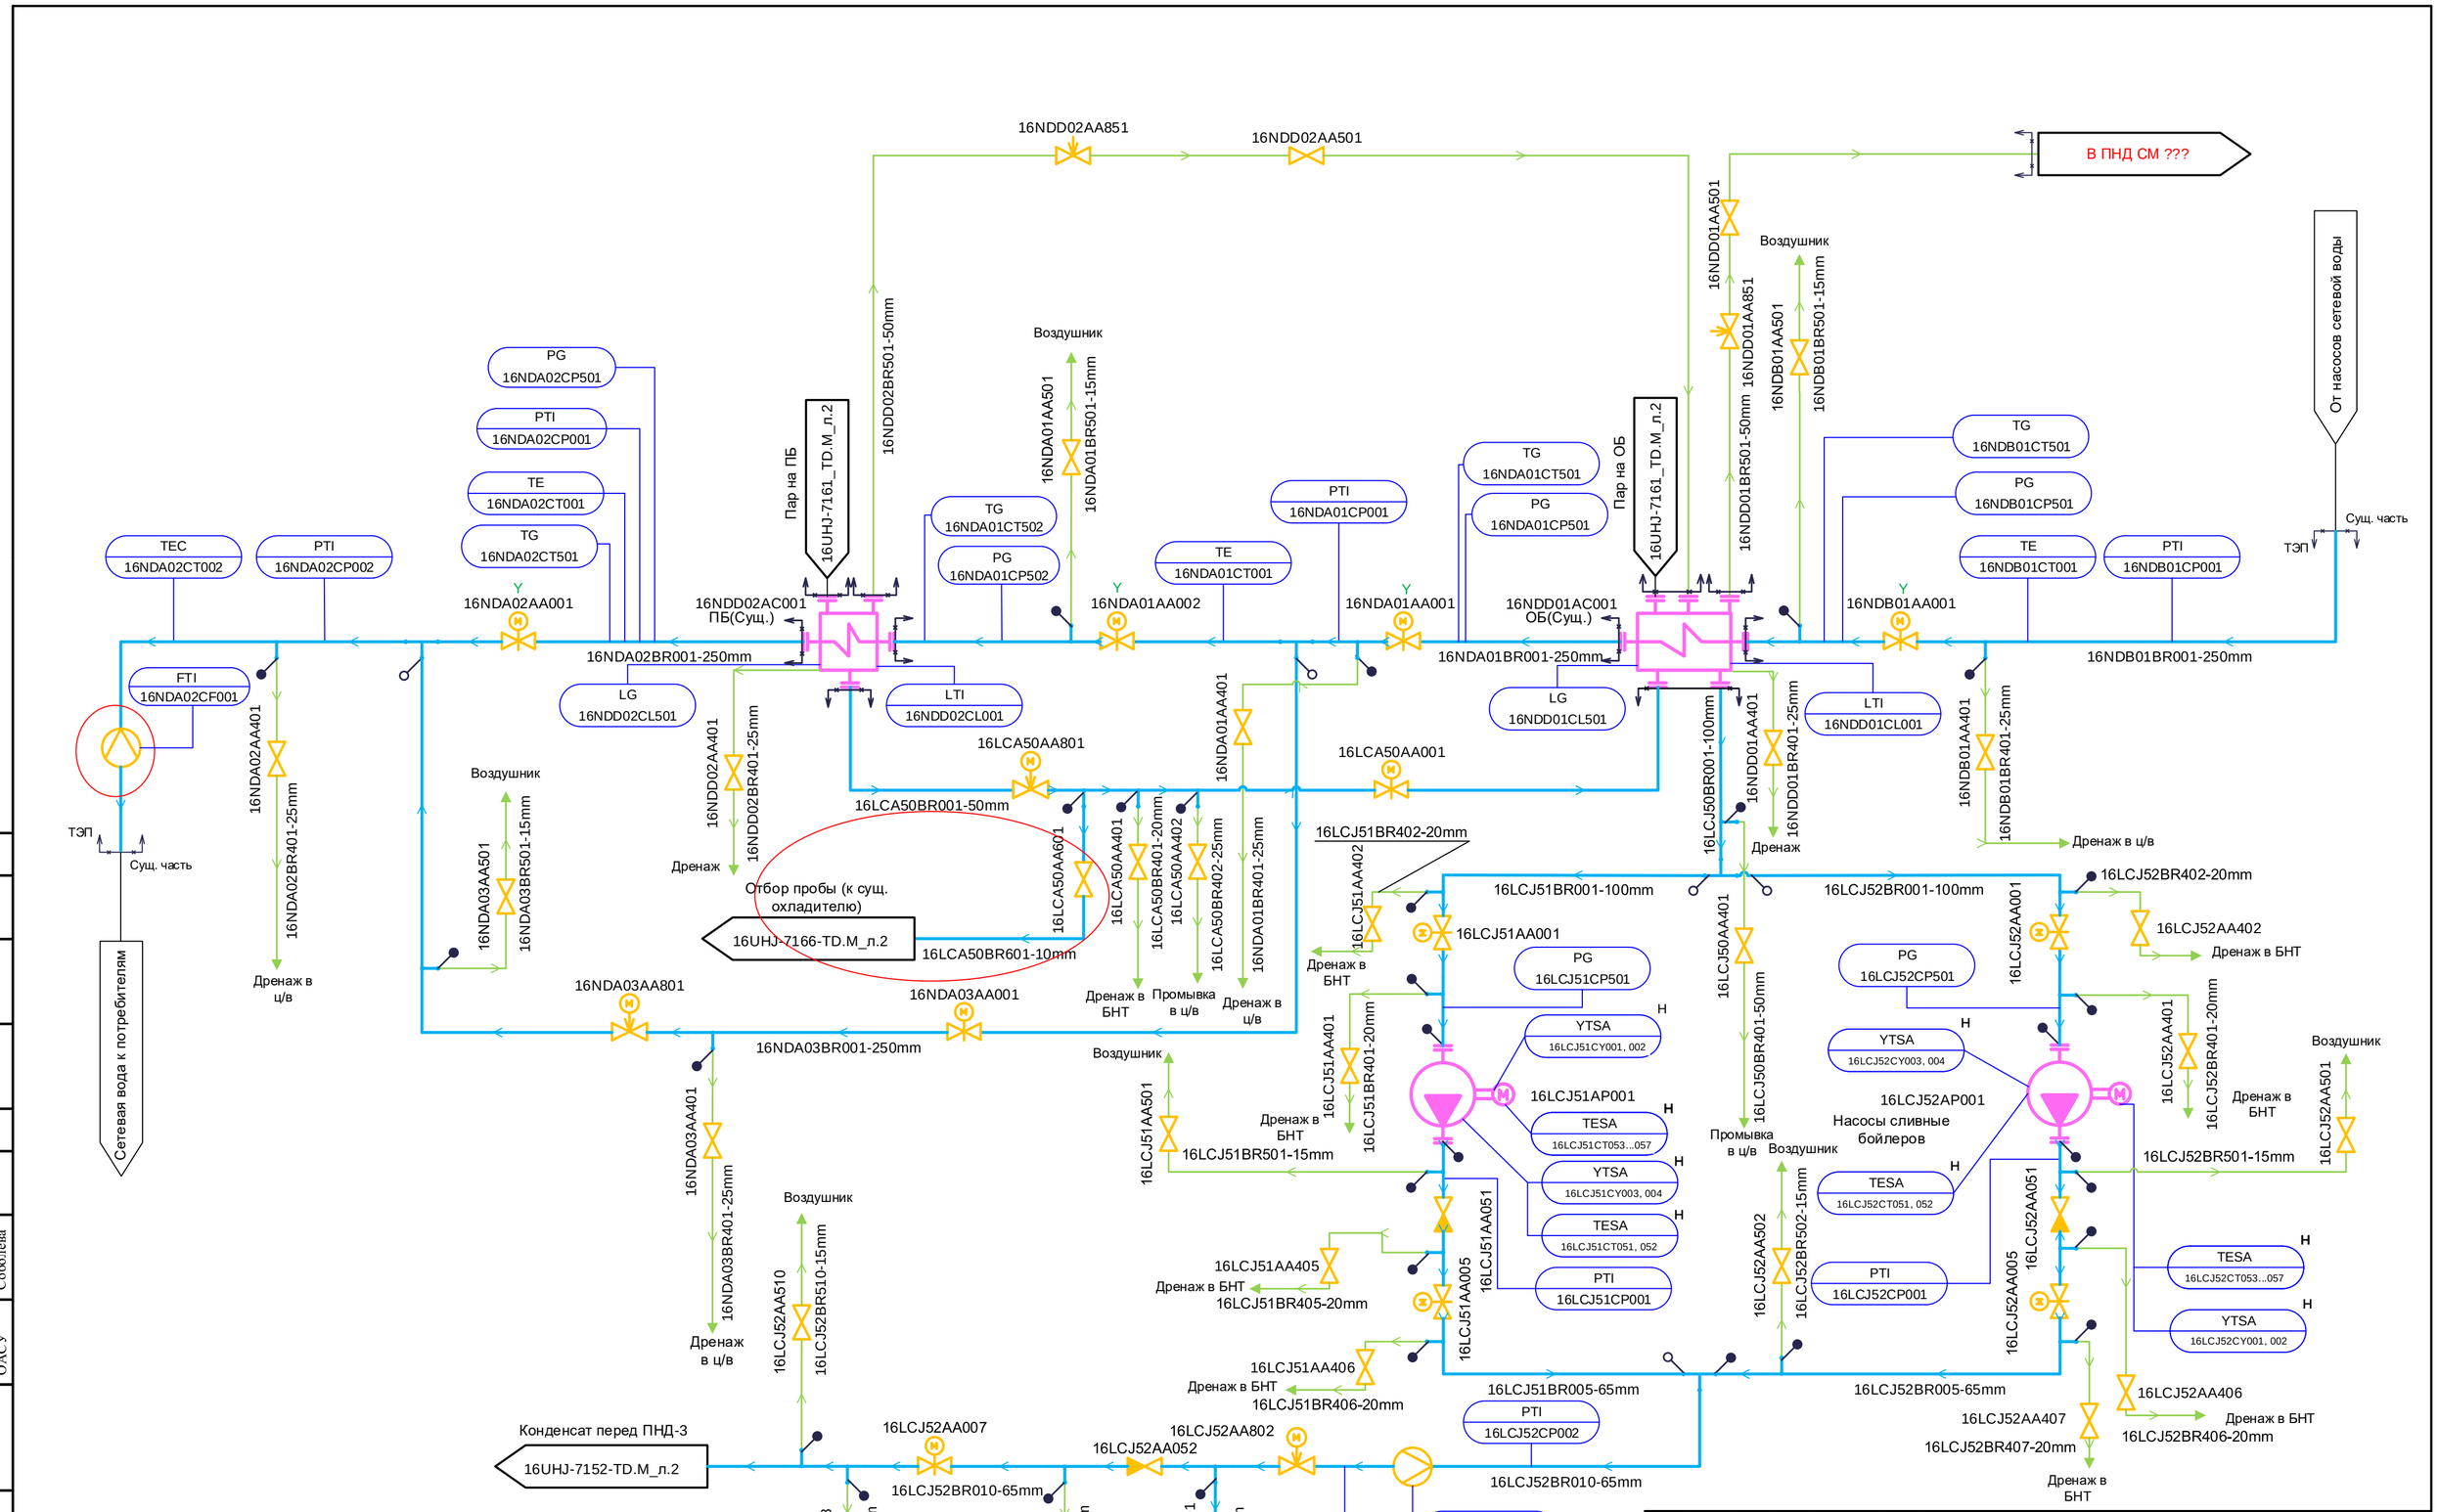

1	-	Зам.	1199-24		05.24	
Изм.	Кол.уч	Лист	№ док.	Подп.	Дата	
Разработал		Дёмина				
Проверил		Гавриленко				
Н. контр.		Астраханцев				

246N1 – 16UHJ – 7143 – TD.M

Модернизация генерирующего объекта Сургутская ГРЭС-1 (16Г)

Главный корпус. PI-диаграмма трубопроводов сетевой воды

Стадия	Лист	Листов
Р	2	

PI-диаграмма трубопроводов сетевой воды. Системы NDA, NDB, LCJ

АКЦИОНЕРНОЕ ОБЩЕСТВО ИНСТИТУТ ТЕПЛОЭЛЕКТРОПРОЕКТ Г. МОСКВА

Согласовано

ОАСУ Соболева

Взам. инв. №

Подпись и дата

Инв. № подл.

Формат А2