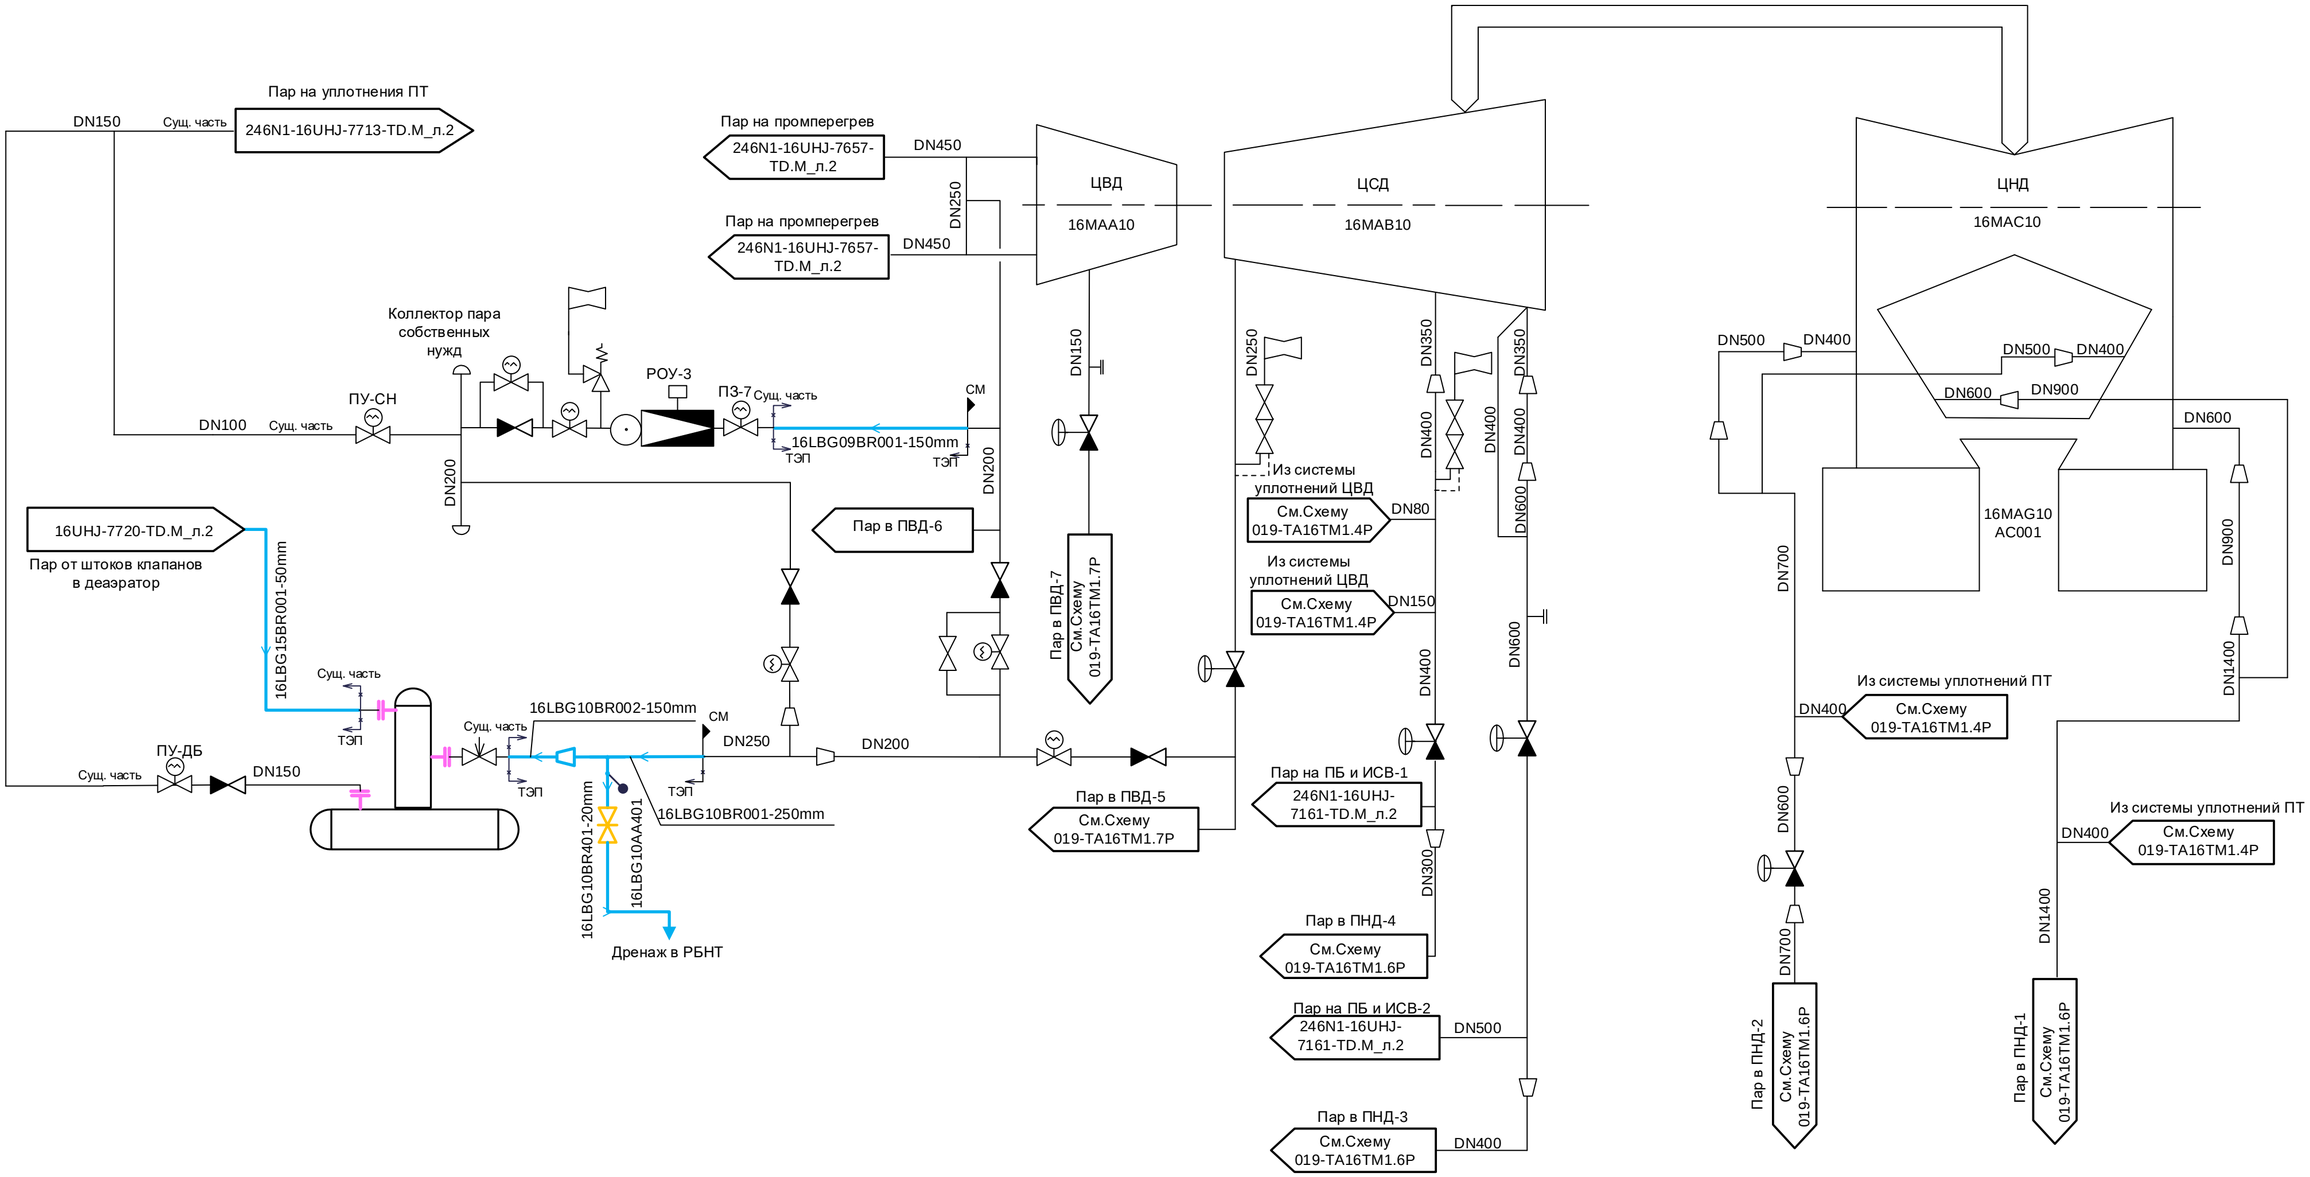

См. Схему ООО «НордЭнергоИнжиниринг» №019-TA-16-TM1.13.P изм.7

См. Тепловую схему ООО «НордЭнергоИнжиниринг» №019-TA16-TM1.1.P изм.8

Существующая часть Сургутской ГРЭС-1

АО «Институт Теплоэлектропроект» (ТЭП)

- граница проектирования

АО «Силовые Машины» (СМ)

- граница проектирования

АО «Институт Теплоэлектропроект» (ТЭП)

2	-	Зам.	3438-24			
Изм.	Кол.уч	Лист	№ док.	Подп.	Дата	
Разработал		Гусев				
Проверил		Демина				
Н. контр.		Астраханцев				

246N1–16UHJ–7148–TD.M

Модернизация генерирующего объекта Сургутская ГРЭС-1 (16г)

Главный корпус. PI-диаграмма трубопроводов пара собственных нужд

Стадия	Лист	Листов
Р	2	

PI-диаграмма трубопроводов пара собственных нужд. Система LBG.

АКЦИОНЕРНОЕ ОБЩЕСТВО ИНСТИТУТ ТЕПЛОЭЛЕКТРОПРОЕКТ Г. МОСКВА

Согласовано

ОДСУ Соболева

Взам. инв. №

Подпись и дата

Инв. № подл.

Формат А2