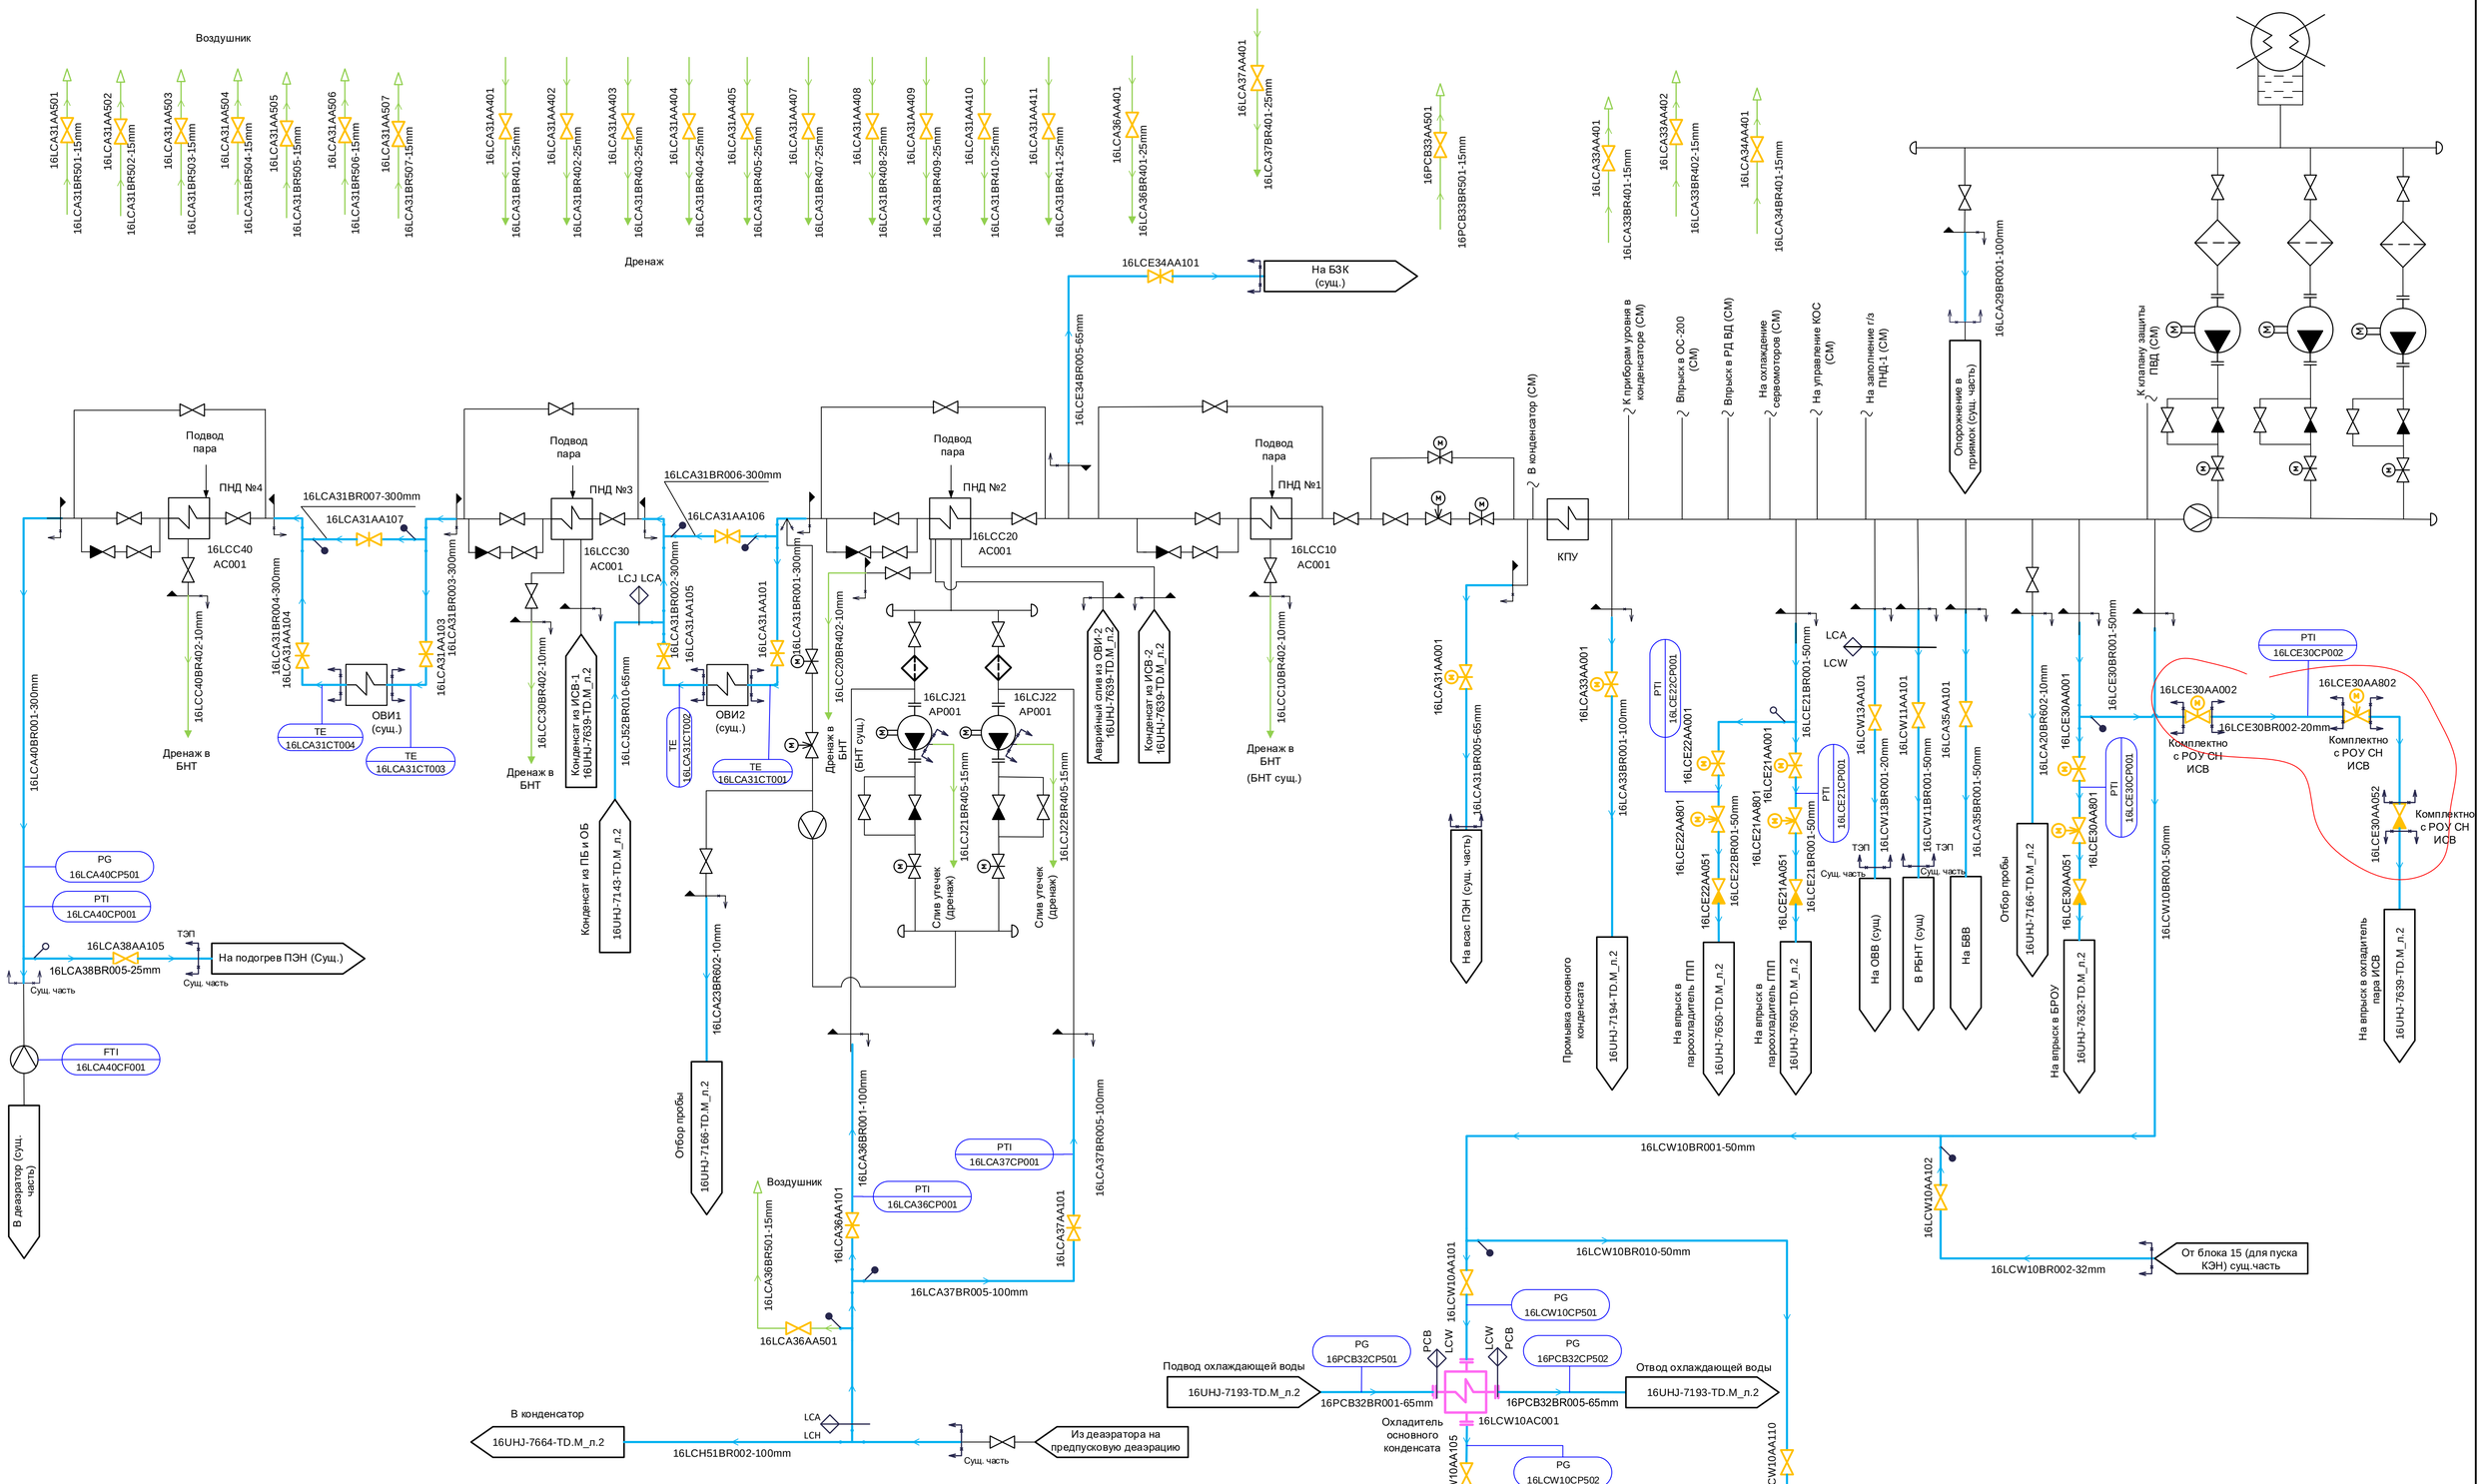

Примечание:
1. Трубопроводы основного конденсата в границах паротурбинной установки см. схемы 019-ТА16-ТМ1.1.Р, 019-ТА16-ТМ1.2.Р, 019-ТА16-ТМ1.6.Р ООО «НордЭнергоИнжиниринг».
2. Трубопроводы обвязки испарительных установок (сущ.) см. PI-Диаграмму 16UHJ-7639-TD.M_п.2.

						246N1–16UHJ–7152–TD.M			
2	-	Зам.	2213-24		08.24	Модернизация генерирующего объекта Сургутская ГРЭС-1 (16г)			
Изм.	Кол.уч	Лист	№ док.	Подп.	Дата				
Разработал		Гусев				Главный корпус. PI-диаграмма трубопроводов основного конденсата	Стадия	Лист	Листов
Проверил		Демина					Р	2	
Н. контр.		Астраханцев				PI-диаграмма трубопроводов основного конденсата. Система LCA.	АКЦИОНЕРНОЕ ОБЩЕСТВО ИНСТИТУТ ТЕПЛОЭЛЕКТРОПРОЕКТ Г. МОСКВА		

Согласовано
ОАСУ Собчева
Взам. инв. №
Подпись и дата
Инв. № подл.

Формат А1