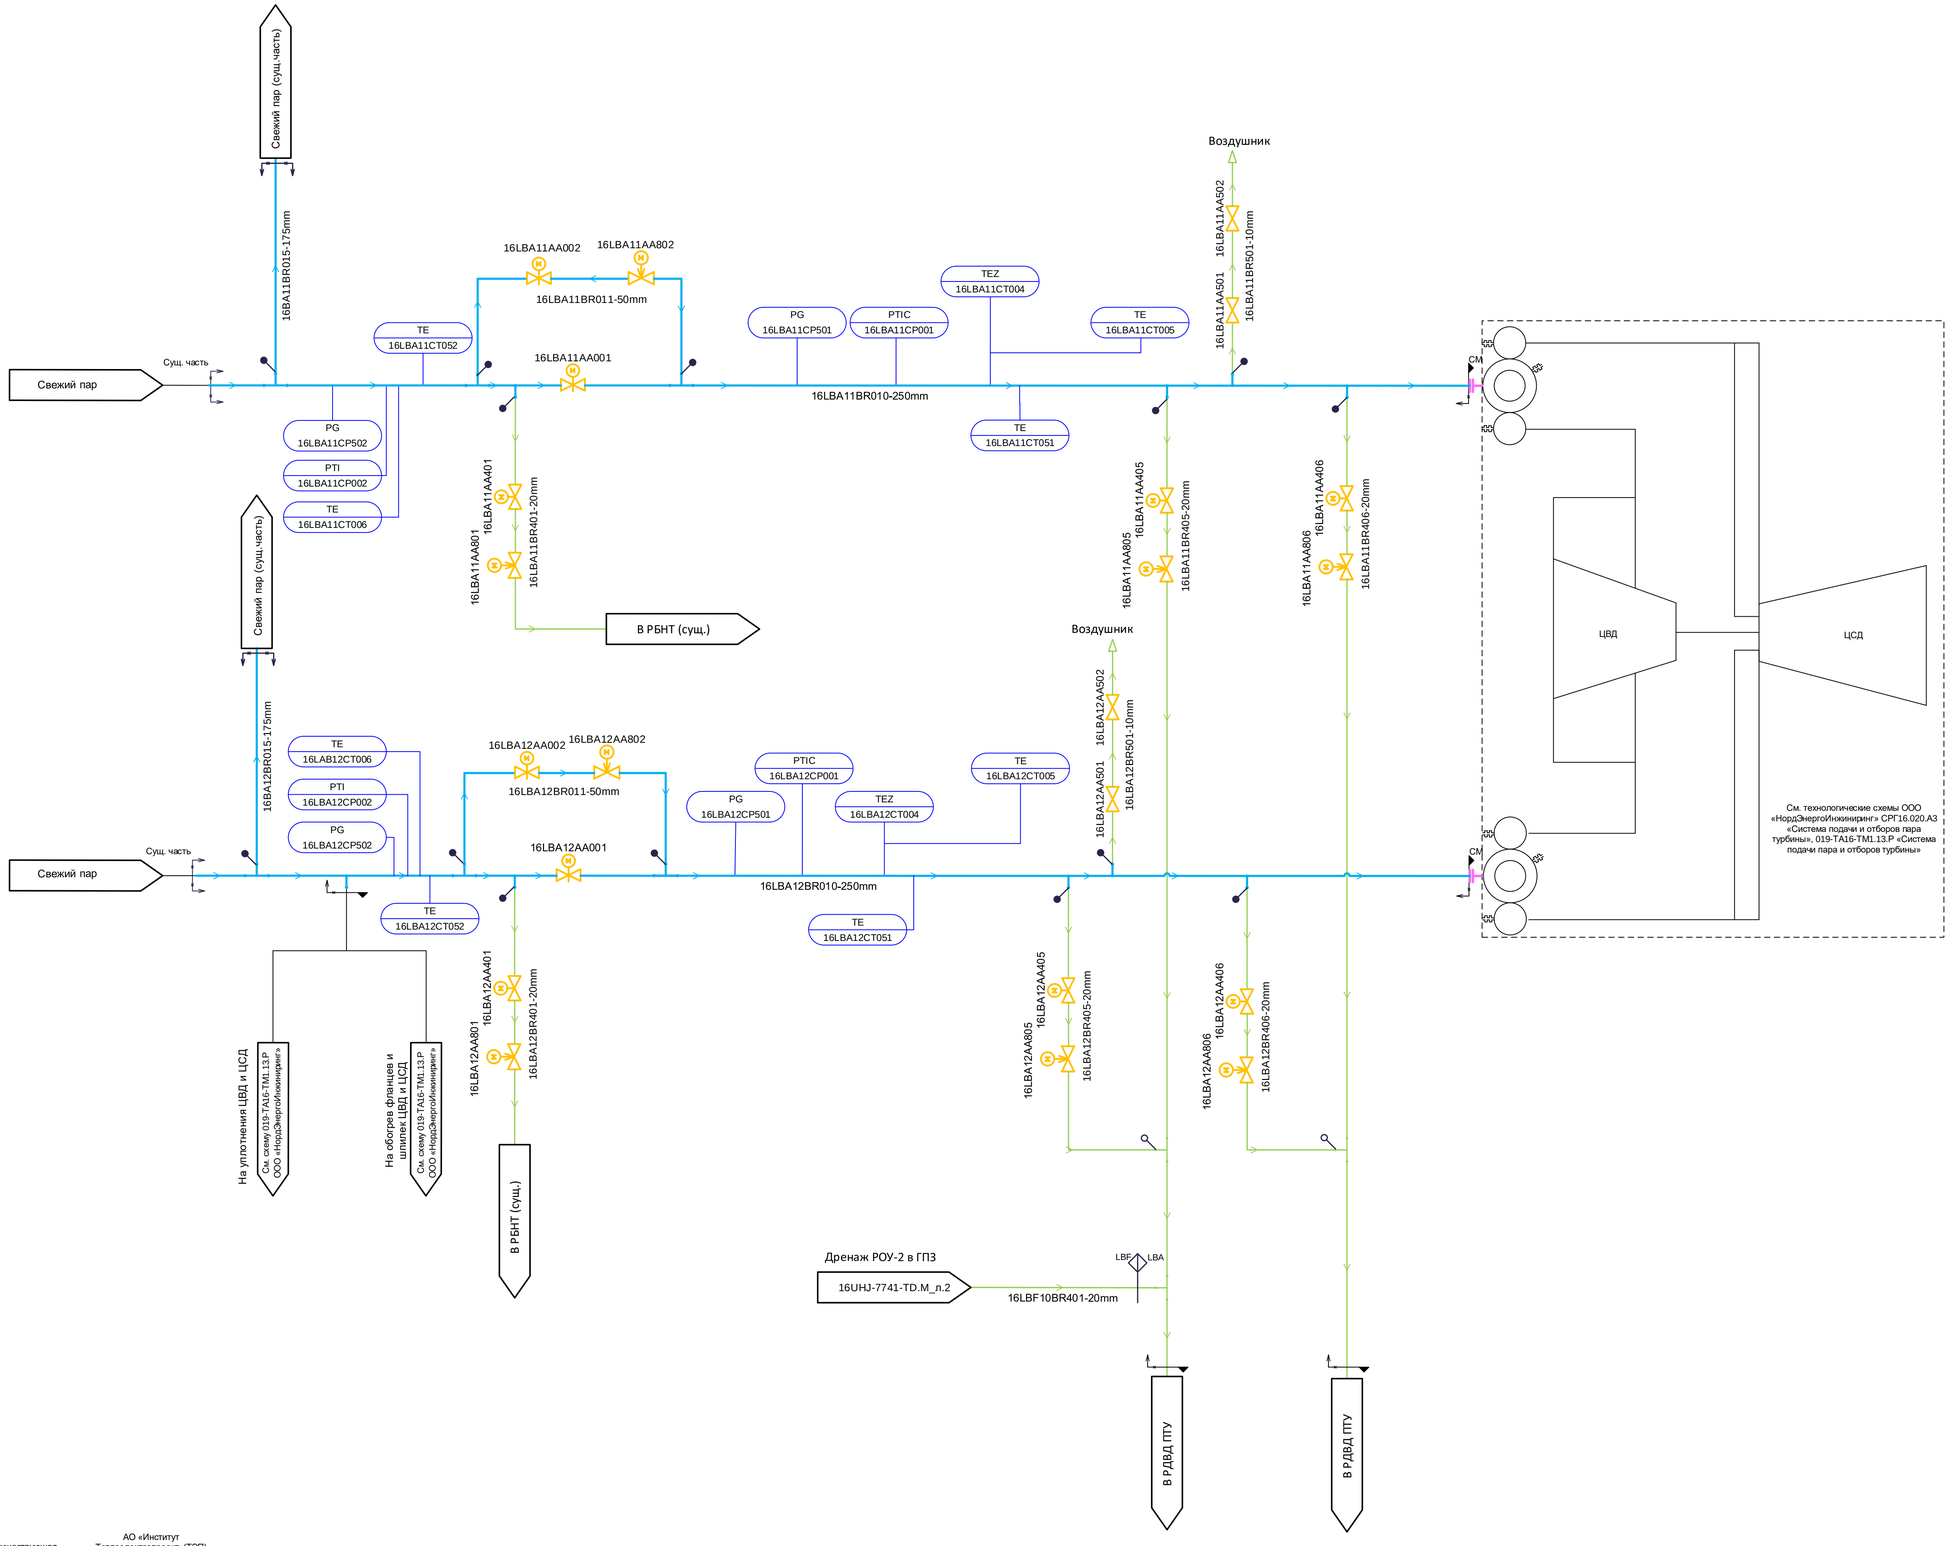

Существующая часть Сургутской ГРЭС-1

АО «Институт Теплоэлектропроект»(ТЭП)

- граница проектирования

АО «Силовые Машины» (СМ)

- граница проектирования

АО «Институт Теплоэлектропроект»(ТЭП)

Согласовано

ОАСУ Соболева

Взам. инв. №

Подпись и дата

Инв. № подл.

						246N1 – 16UHJ – 7159 – TD.M
2	-	Зам.	2407-24		09.24	Модернизация генерирующего объекта Сургутская ГРЭС-1 (16Г)
Изм.	Кол.уч	Лист	№ док.	Подп.	Дата	
Разработал		Дёмина				Главный корпус. PI-диаграмма свежего пара
Проверил		Гавриленко				
Н. контр.		Черемушкина				PI-диаграмма свежего пара. Система LBA.

Стадия	Лист	Листов
Р	2	

АКЦИОНЕРНОЕ ОБЩЕСТВО ИНСТИТУТ ТЕПЛОЭЛЕКТРОПРОЕКТ Г. МОСКВА

Формат А1