См. схему «Система маслоснабжения смазки. Схема контроля и управления» ЛМЗ № СРГ16.001.А3 АО «Силовые машины»

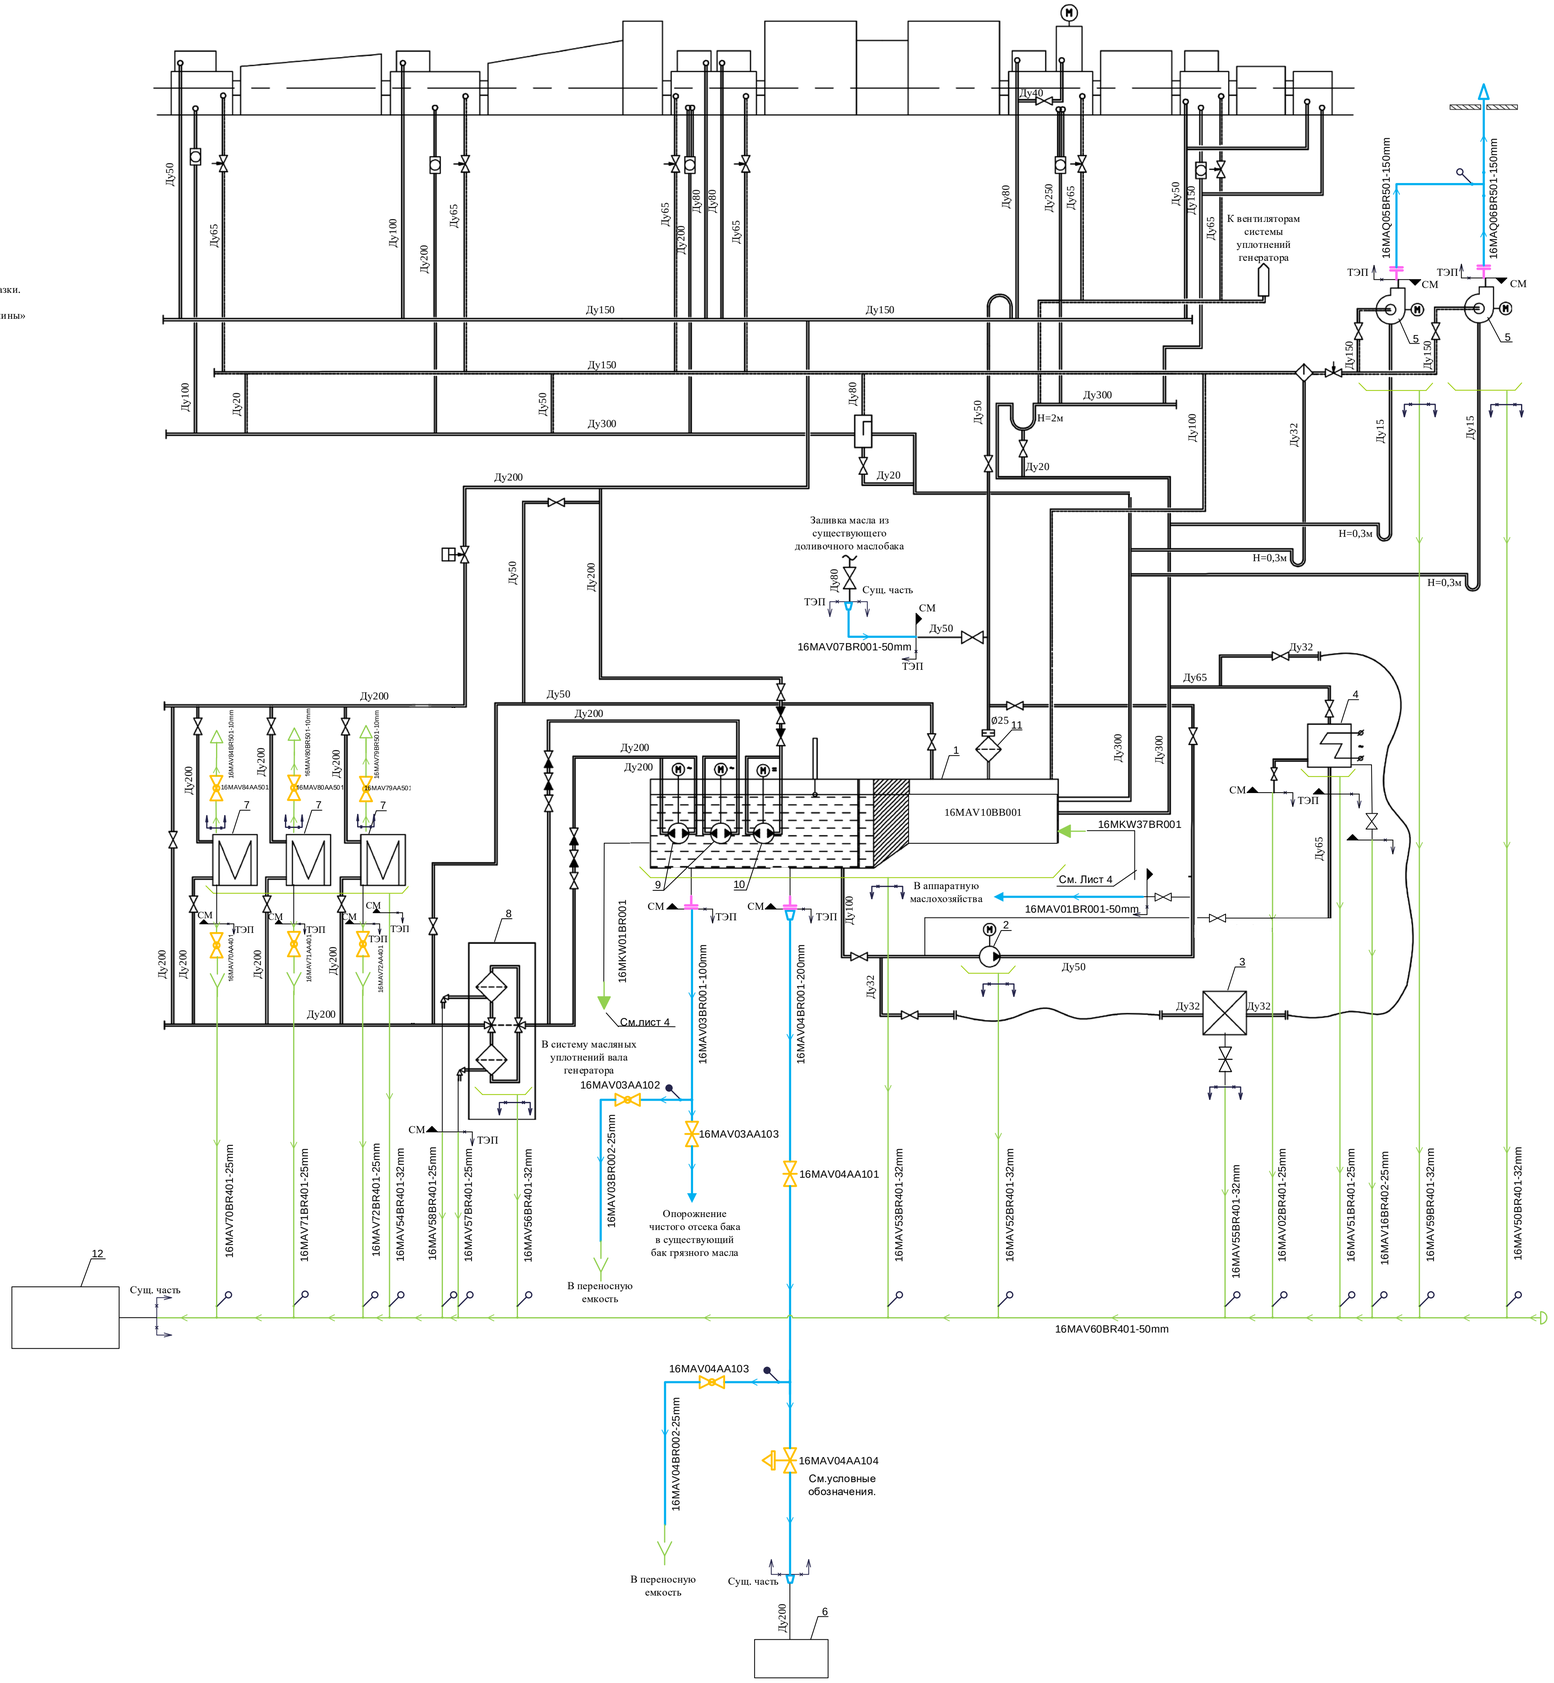

Перечень оборудования

Поз.	Наименование	Кол.
1	Бак масляный ПТ №16	1
2	Насос циркуляции и фильтрации масла	1
3	Агрегат для очистки масла	1
4	Электронагреватель масла	1
5	Вентилятор отсоса масляных паров из бака системы смазки	2
6	Подземный бак аварийного слива масла	1
7	Маслоохладитель системы смазки ПТ	3
8	Дуплексный фильтр	1
9	Насос системы смазки	2
10	Насос аварийный системы смазки	1
11	Фильтр тонкой очистки	1
12	Бак сбора грязного масла V=4 м3	1

Условные обозначения

	Задвижка с ручным колонковым приводом
	Запорная арматура с ручным приводом
	Вентиль
	Обратный клапан
	Клапан для опорожнения
	Фильтр

Примечание:
1)Задвижка 16MAV04AA101
С ручным приводом открыта и опломбирована при эксплуатации.
2)Задвижка 16MAV04AA104 оснащена колонковым приводом.

Существующая часть Сургутской ГРЭС-1 — АО «Институт Теплоэлектропроект» (ТЭП) - граница проектирования

АО «Силовые Машины» (СМ) - граница проектирования — АО «Институт Теплоэлектропроект» (ТЭП)

2	-	Зам.	2815-24			246N1-16UHJ-7160-TD.M			
Изм.	Кол.уч	Лист	№ док.	Подп.	Дата	Модернизация генерирующего объекта Сургутская ГРЭС-1 (16г)			
Разработал		Гусев				Главный корпус PI-диаграмма трубопроводов маслоснабжения турбоустановки	Стадия	Лист	Листов
Проверил		Демина					Р	2	
Гл.спец		Гавриленко							
Н. контр.		Черемушкина				PI-диаграмма трубопроводов маслоснабжения системы смазки турбины. Система MAV	АКЦИОНЕРНОЕ ОБЩЕСТВО ИНСТИТУТ ТЕПЛОЭЛЕКТРОПРОЕКТ Г. МОСКВА		

Согласовано ОАСУ Соболева

Взам. инв. № | Подпись и дата | Инв. № подл.

Формат А1