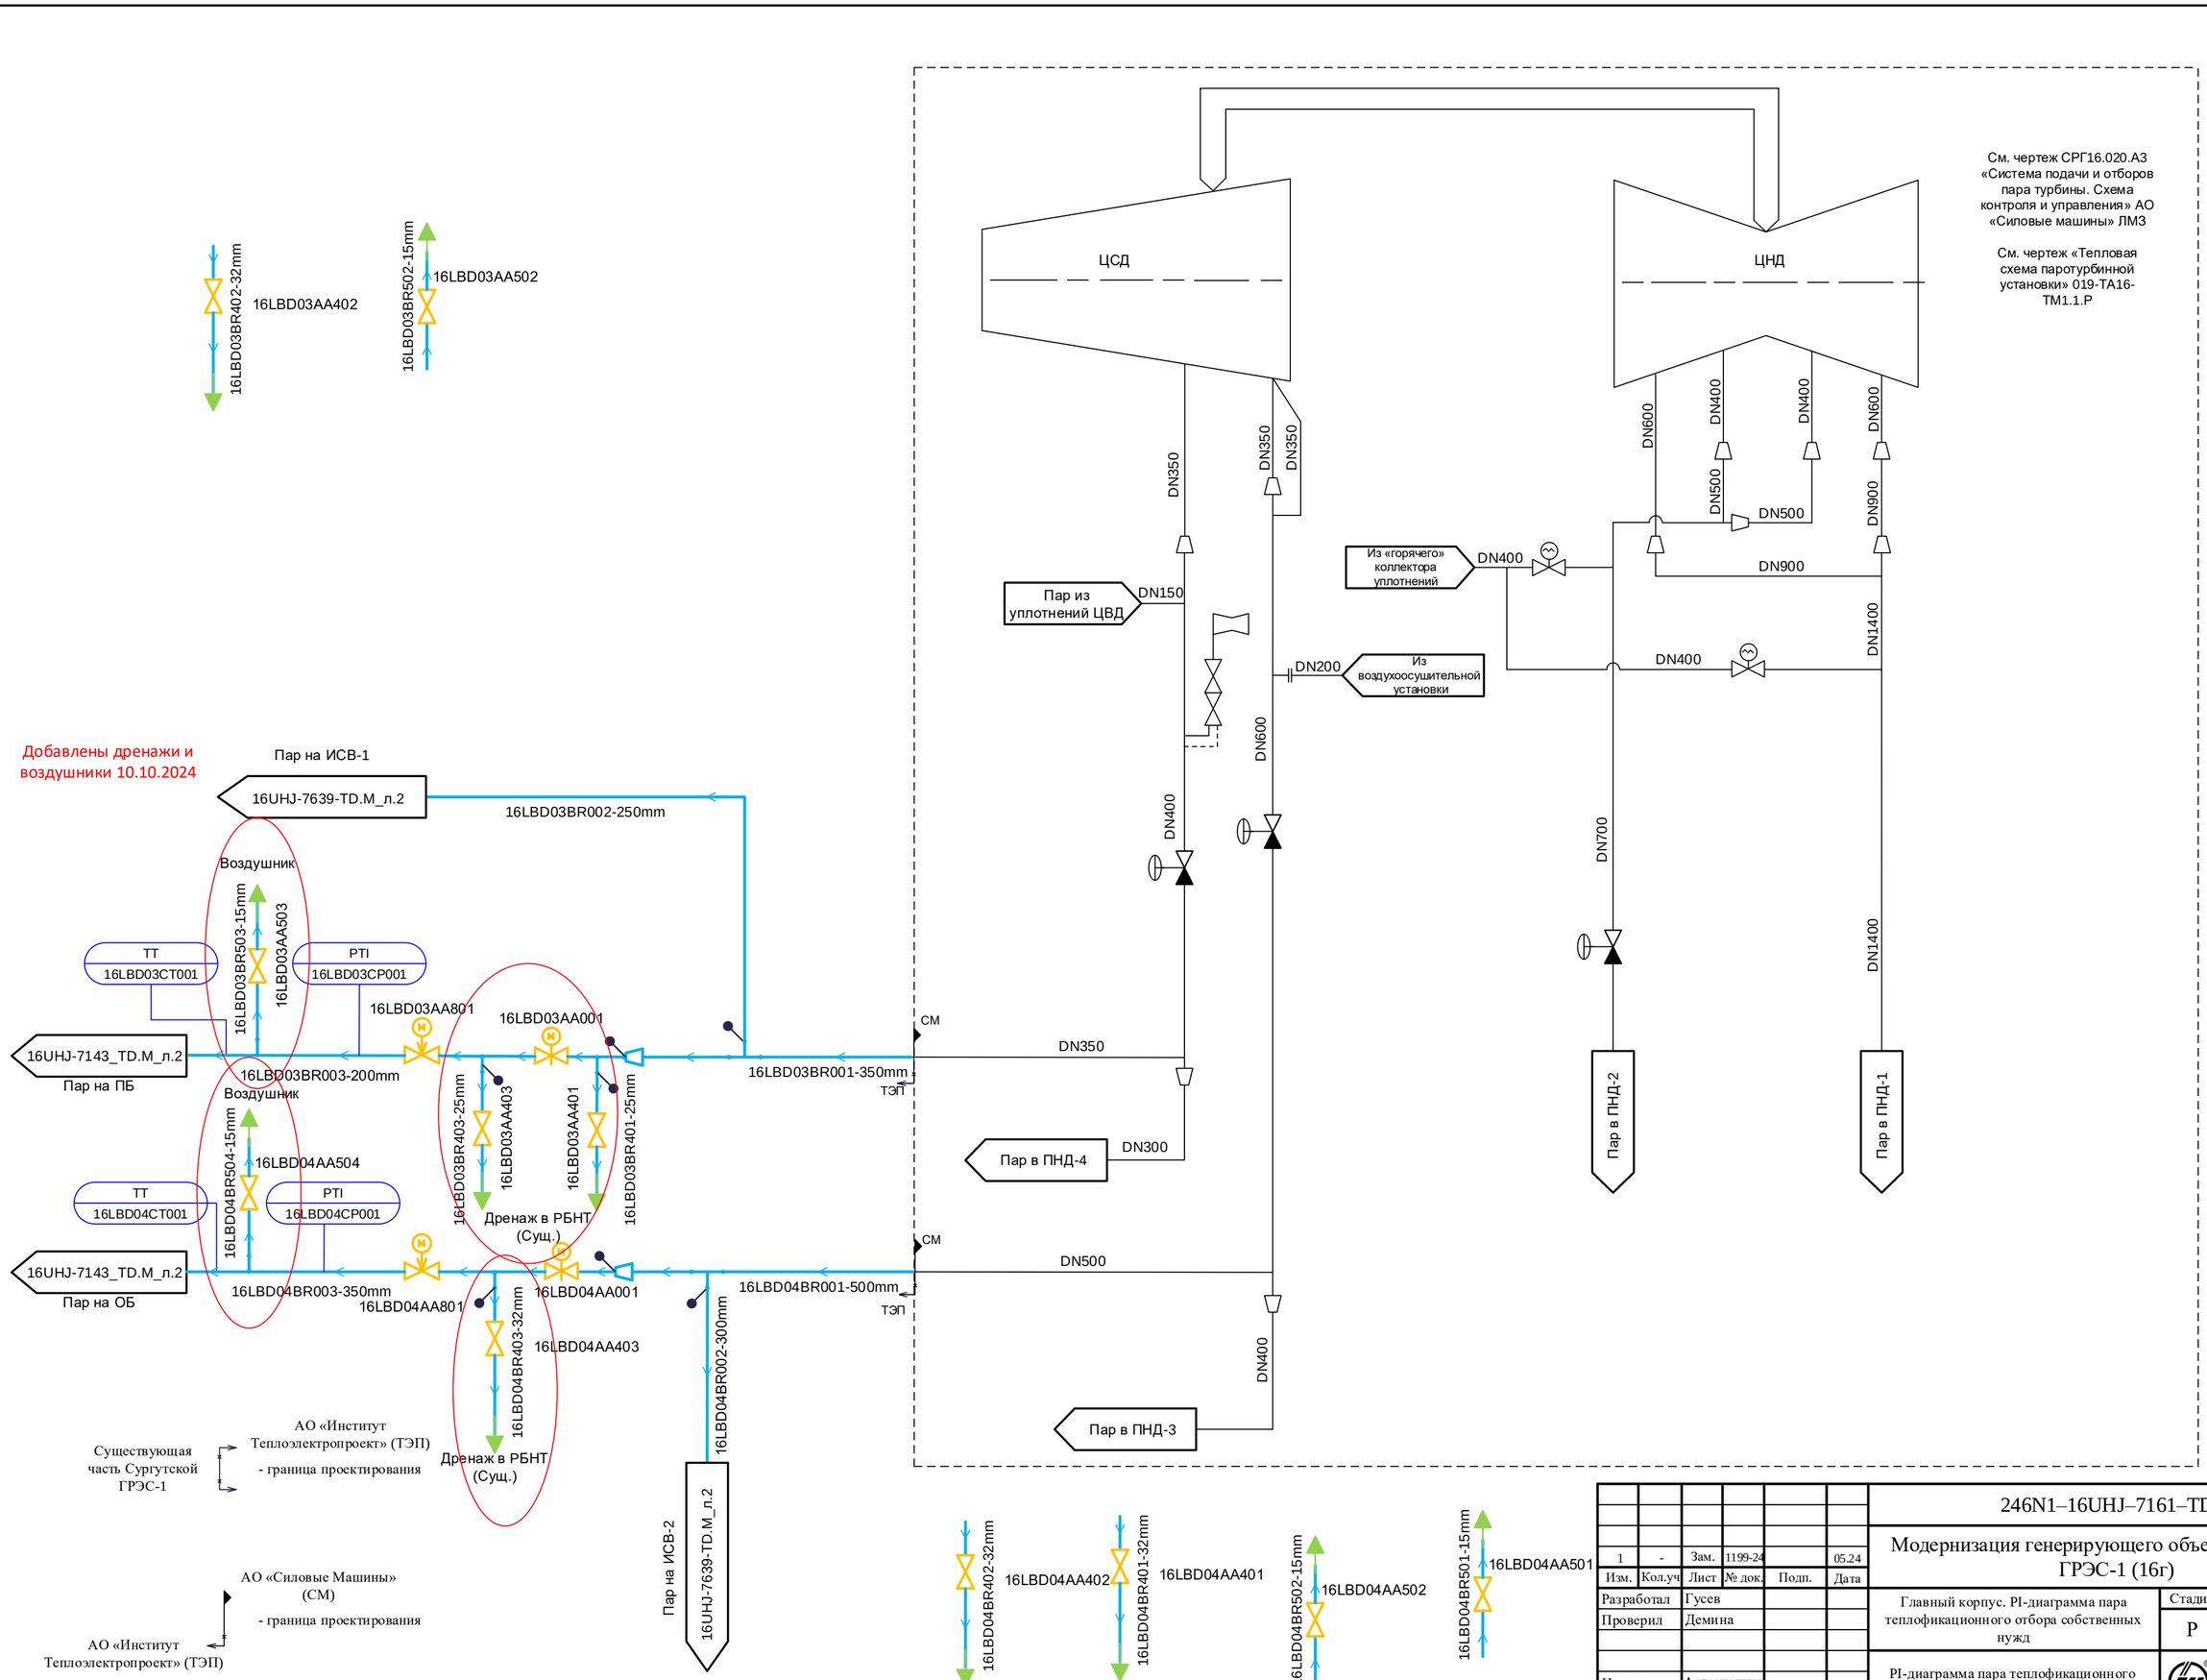

1	-	Зам.	1199-24		05.24	
Изм.	Кол.уч	Лист	№ док.	Подп.	Дата	
Разработал		Гусев				
Проверил		Демина				
Н. контр.		Астраханцев				

246N1–16UHJ–7161–TD.M

Модернизация генерирующего объекта Сургутская ГРЭС-1 (16г)

Главный корпус. PI-диаграмма пара теплофикационного отбора собственных нужд

Стадия	Лист	Листов
Р	2	

PI-диаграмма пара теплофикационного отбора собственных нужд. Система LBD

АКЦИОНЕРНОЕ ОБЩЕСТВО ИНСТИТУТ ТЕПЛОЭЛЕКТРОПРОЕКТ Г. МОСКВА

Согласовано
ОАСУ Соболева

Взам. инв. №

Подпись и дата

Инв. № подл.

Формат А2