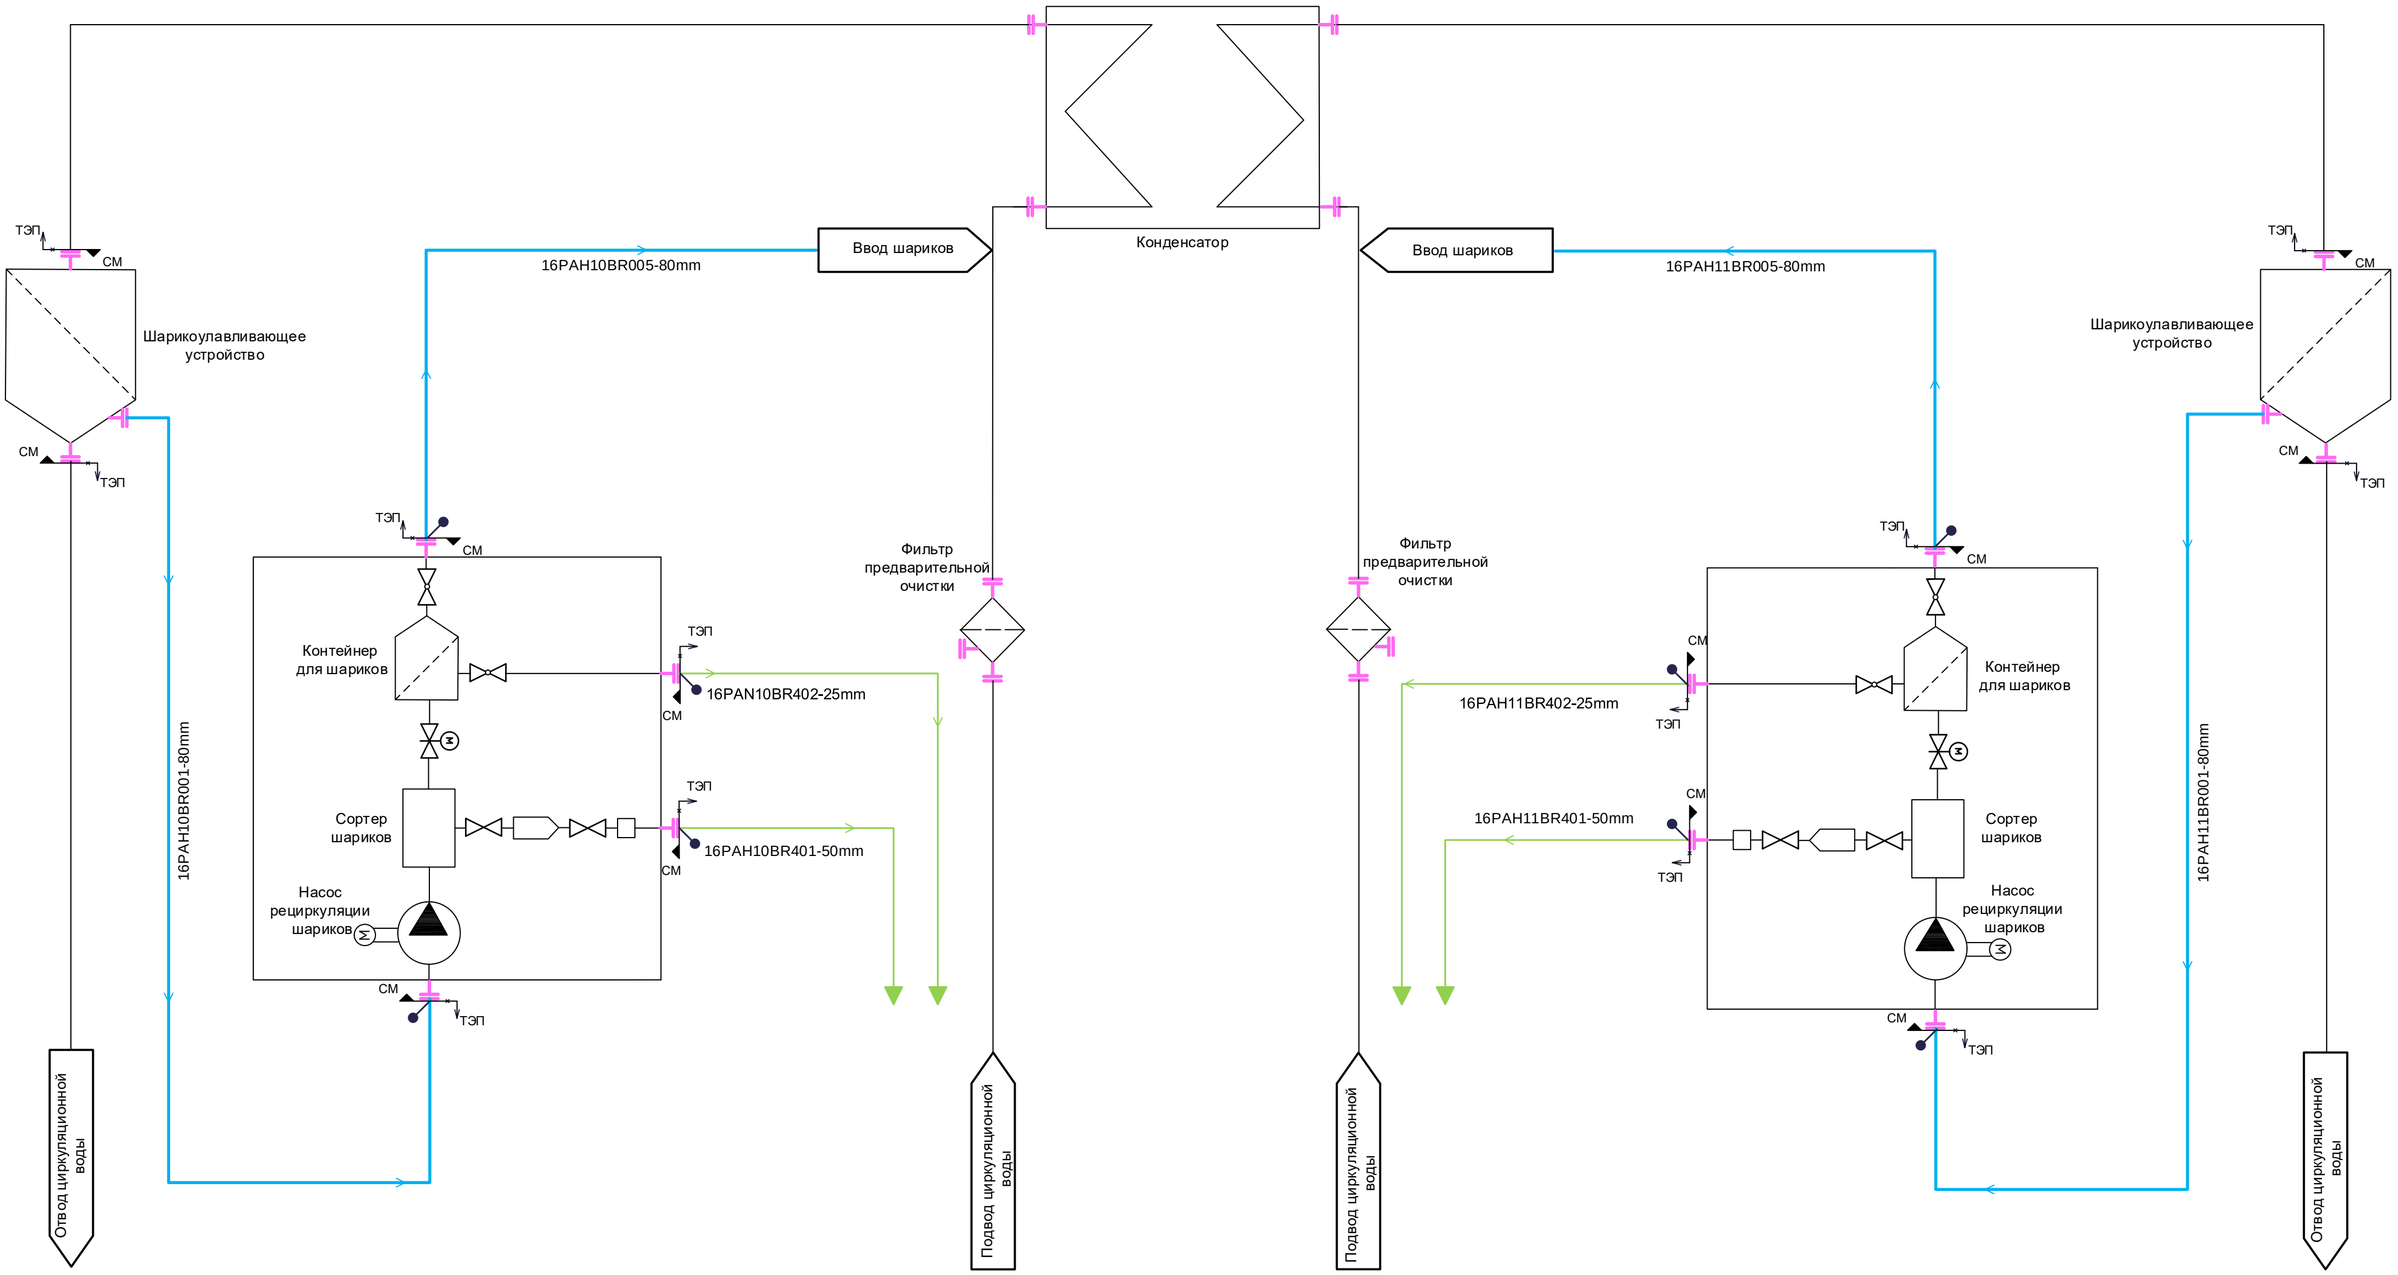

Согласовано

Взам. инв. №

Подпись и дата

Инв. № подл.

Изм.	Кол.уч	Лист	№ док.	Подп.	Дата
Разработал		Гусев.Т.			
Проверил		Сладков			
Н. контр.		Черемушкина			

246N1-16UHJ-7165-TD.M

Модернизация генерирующего объекта Сургутская ГРЭС-1(16г).

Главный корпус.PI-диаграмма трубопроводов системы шариковой очистки конденсатора турбоагрегата.

Стадия	Лист	Листов
Р	2	

PI-Диаграмма трубопроводов системы шариковой очистки конденсатора турбоагрегата. Система РАН

АКЦИОНЕРНОЕ ОБЩЕСТВО ИНСТИТУТ ТЕПЛОЭЛЕКТРОПРОЕКТ Г. МОСКВА

Формат А2