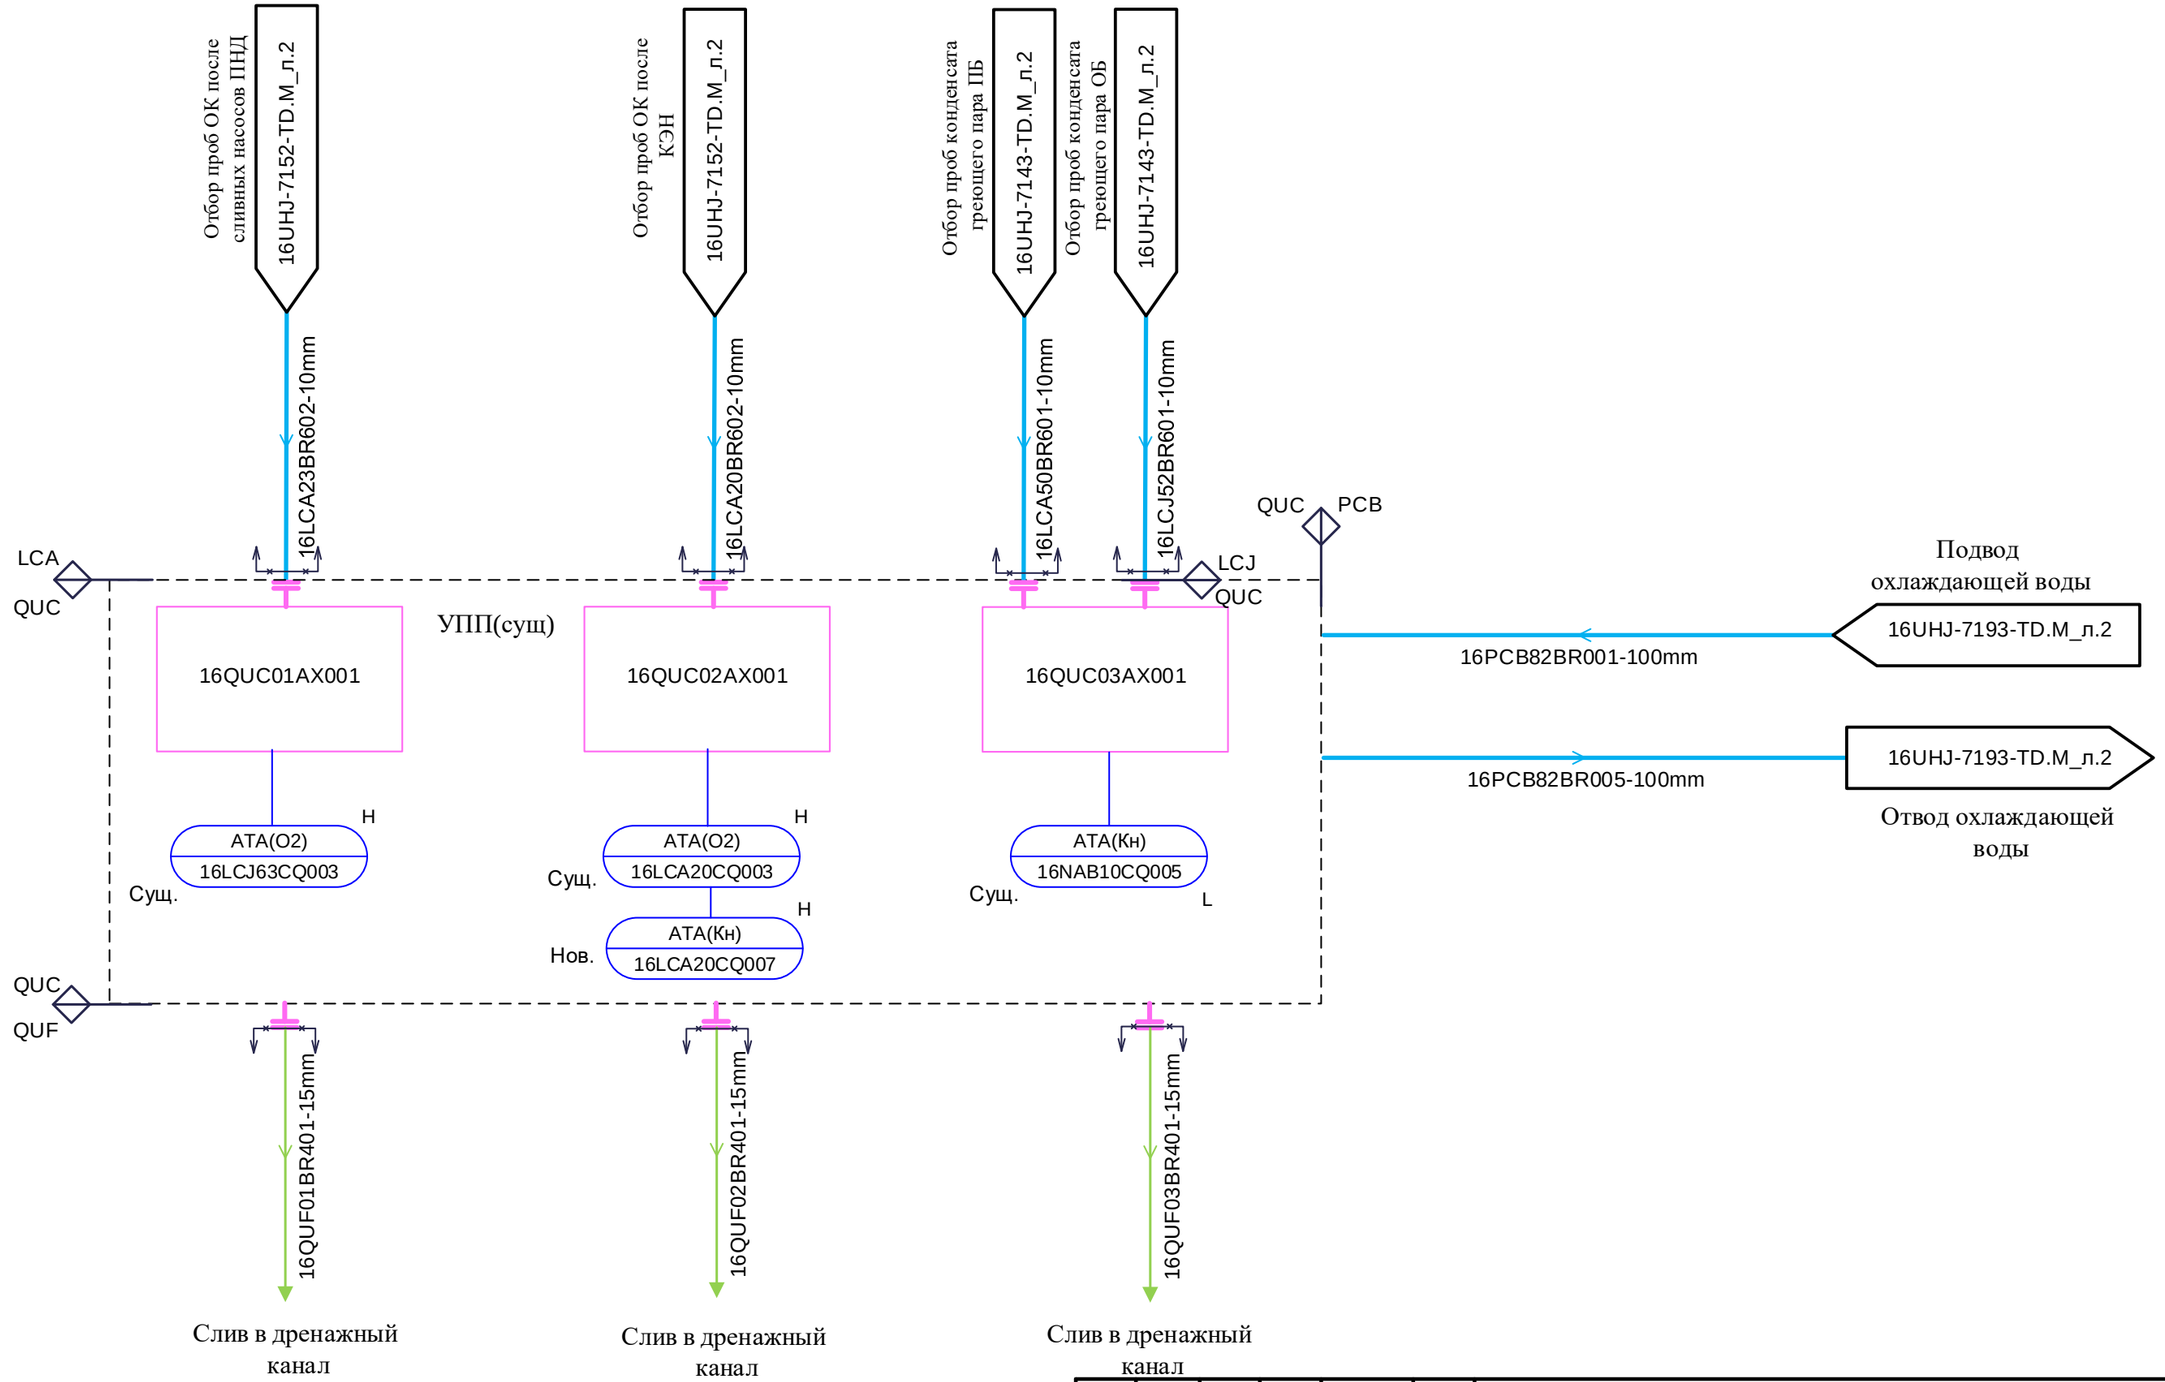

Существующая часть Сургутской ГРЭС-1

АО «Институт Теплоэлектропроект» (ТЭП)
- граница проектирования

АО «Силовые Машины» (СМ)
- граница проектирования

АО «Институт Теплоэлектропроект» (ТЭП)

Изм.	Кол.уч	Лист	№ док.	Подп.	Дата
1	-	Зам.	1199-24		05.24

Разработал	Дёмина	
Проверил	Гавриленко	
Н. контр.	Астраханцев	

246N1-16UHJ-7166-TD.M

Модернизация генерирующего объекта Сургутская ГРЭС-1 (16г)

Главный корпус
PI-диаграмма трубопроводов отборов проб основного конденсата

Стадия	Лист	Листов
Р	2	

PI-диаграмма трубопроводов отборов проб основного конденсата.
Система QUF, LCA, LCJ

АКЦИОНЕРНОЕ ОБЩЕСТВО ИНСТИТУТ ТЕПЛОЭЛЕКТРОПРОЕКТ Г. МОСКВА

Согласовано

Взам. инв. №

Подпись и дата

Инв. № подл.

Формат А3