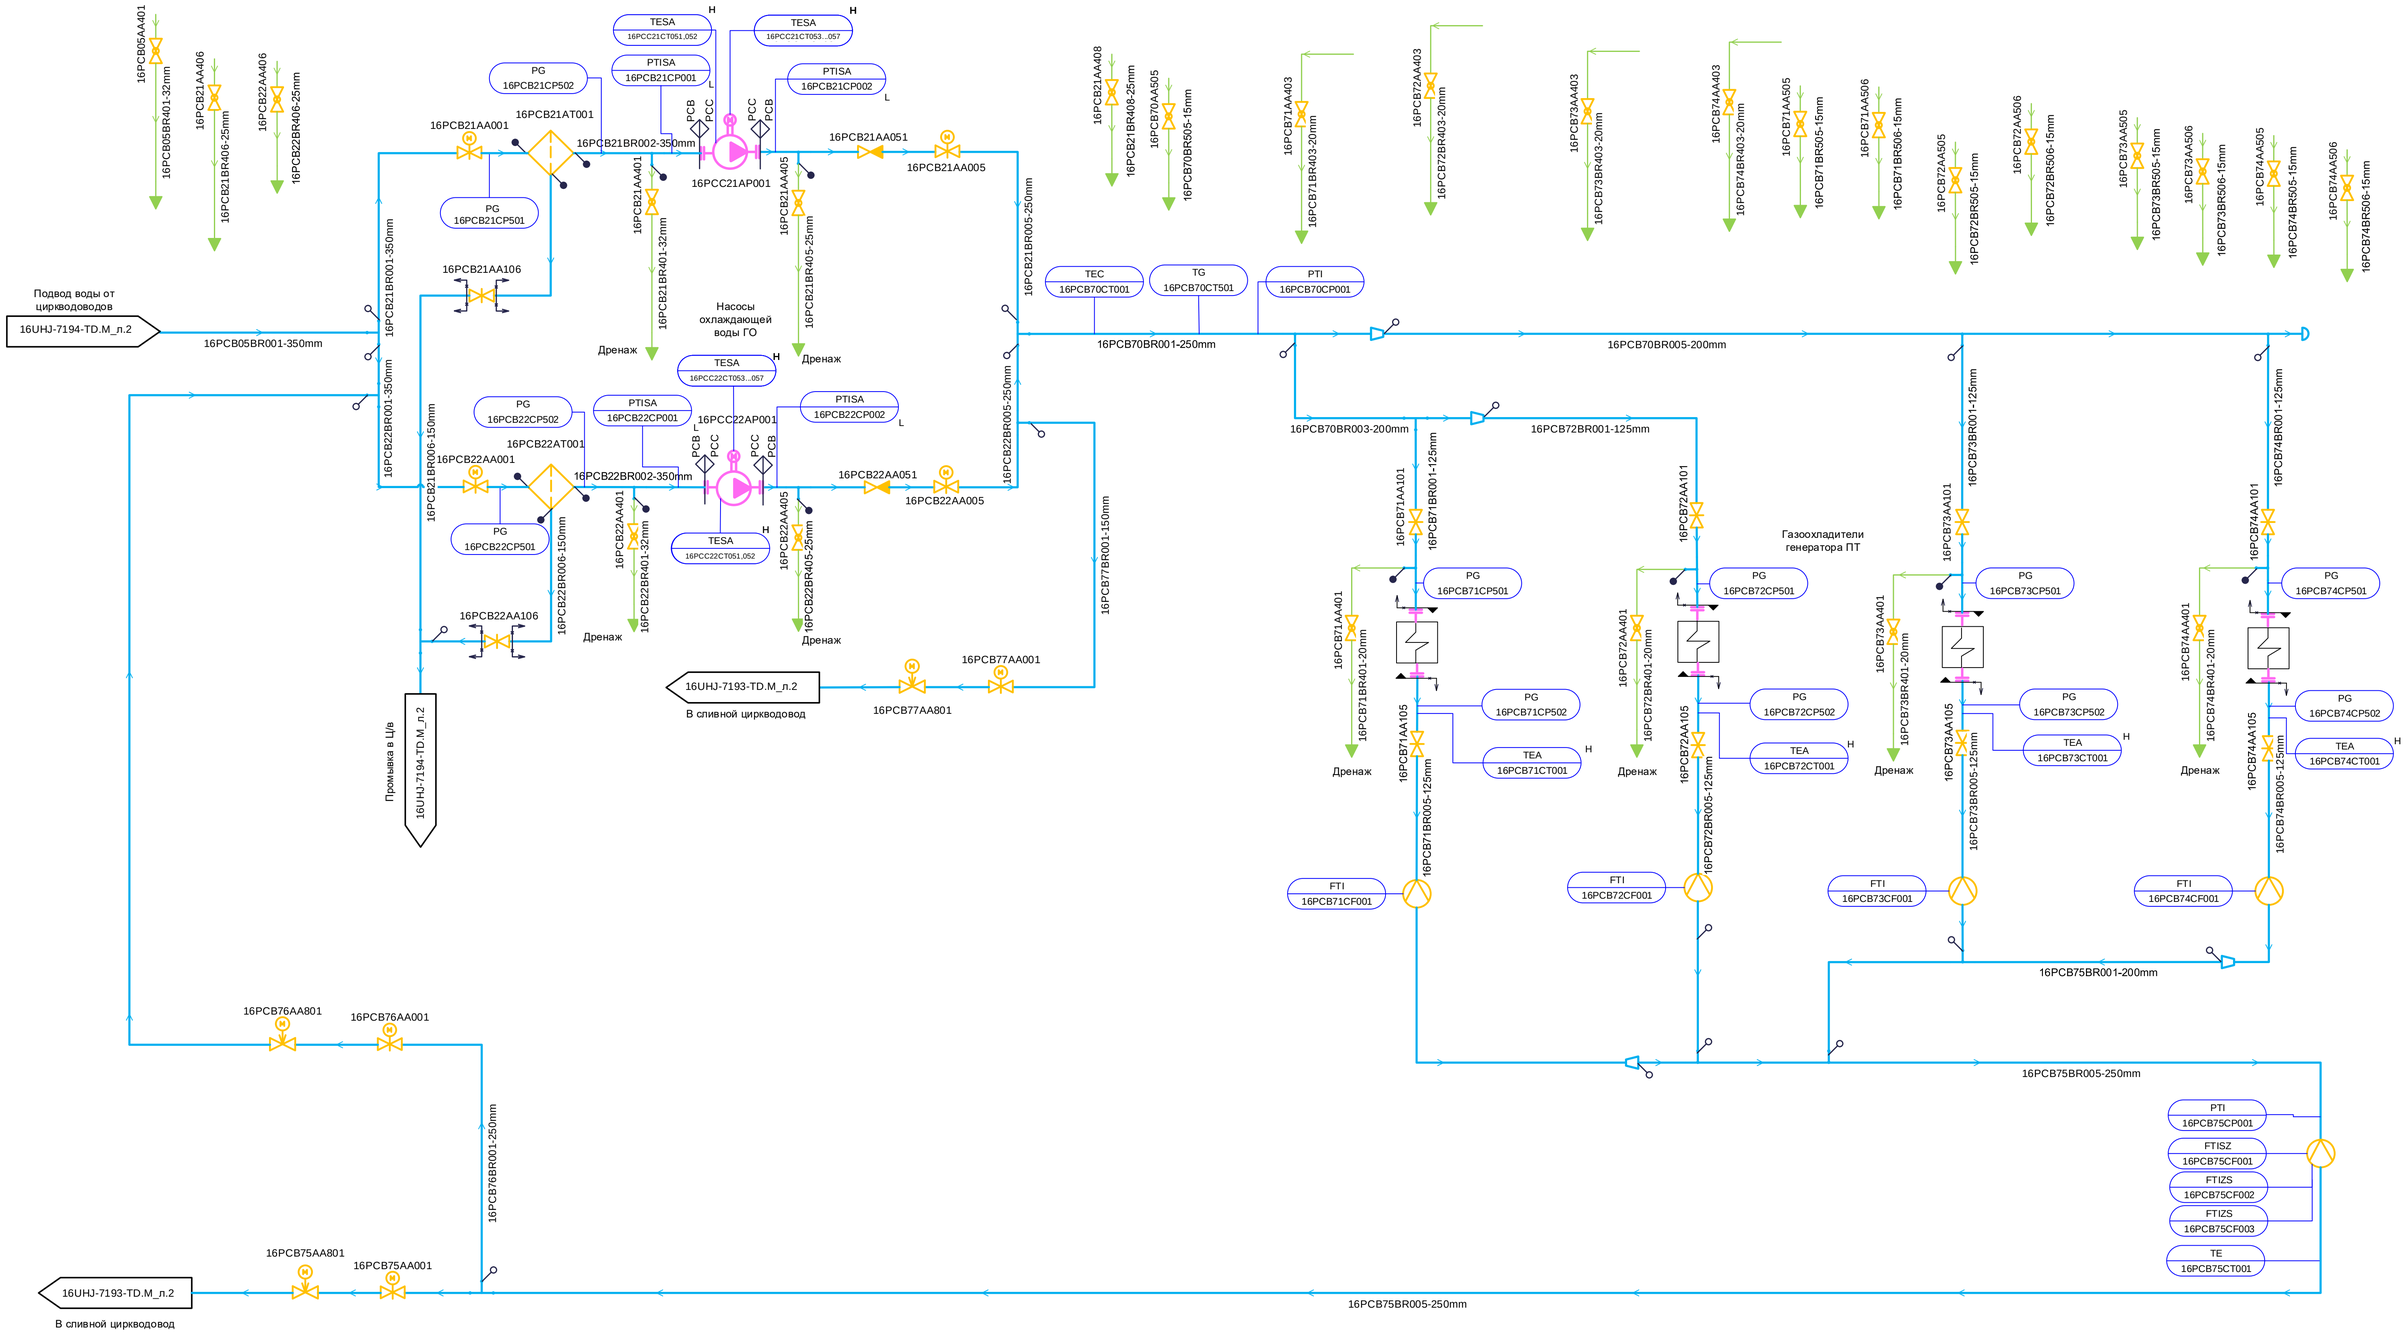

Существующая часть Сургутской ГРЭС-1 → АО «Институт Теплоэлектропроект» (ТЭП) - граница проектирования

АО «Институт Теплоэлектропроект» (ТЭП) → АО «Силовые Машины» (СМ) - граница проектирования

Примечание: Краны шаровые 16PCB21AA106 и 16PCB22AA106 поставляются комплектно с фильтрами

1	-	Зам.	1199-24		08.24	
Изм.	Кол.уч	Лист	№ док.	Подп.	Дата	
Разработал		Демина				
Проверил		Гавриленко				
Н. контр.		Астраханцев				

246N1 – 16UHJ – 7193 – TD.M

Модернизация генерирующего объекта Сургутская ГРЭС-1 (16Г)

Главный корпус. PI-диаграмма охлаждающей воды вспомогательного оборудования турбоагрегата

Стадия	Лист	Листов
Р	3	

PI-диаграмма охлаждающей воды вспомогательного оборудования турбоагрегата. Система РСВ

АКЦИОНЕРНОЕ ОБЩЕСТВО ИНСТИТУТ ТЕПЛОЭЛЕКТРОПРОЕКТ Г. МОСКВА

Согласовано

Взам. инв. №

Подпись и дата

Инв. № подл.

Формат А1