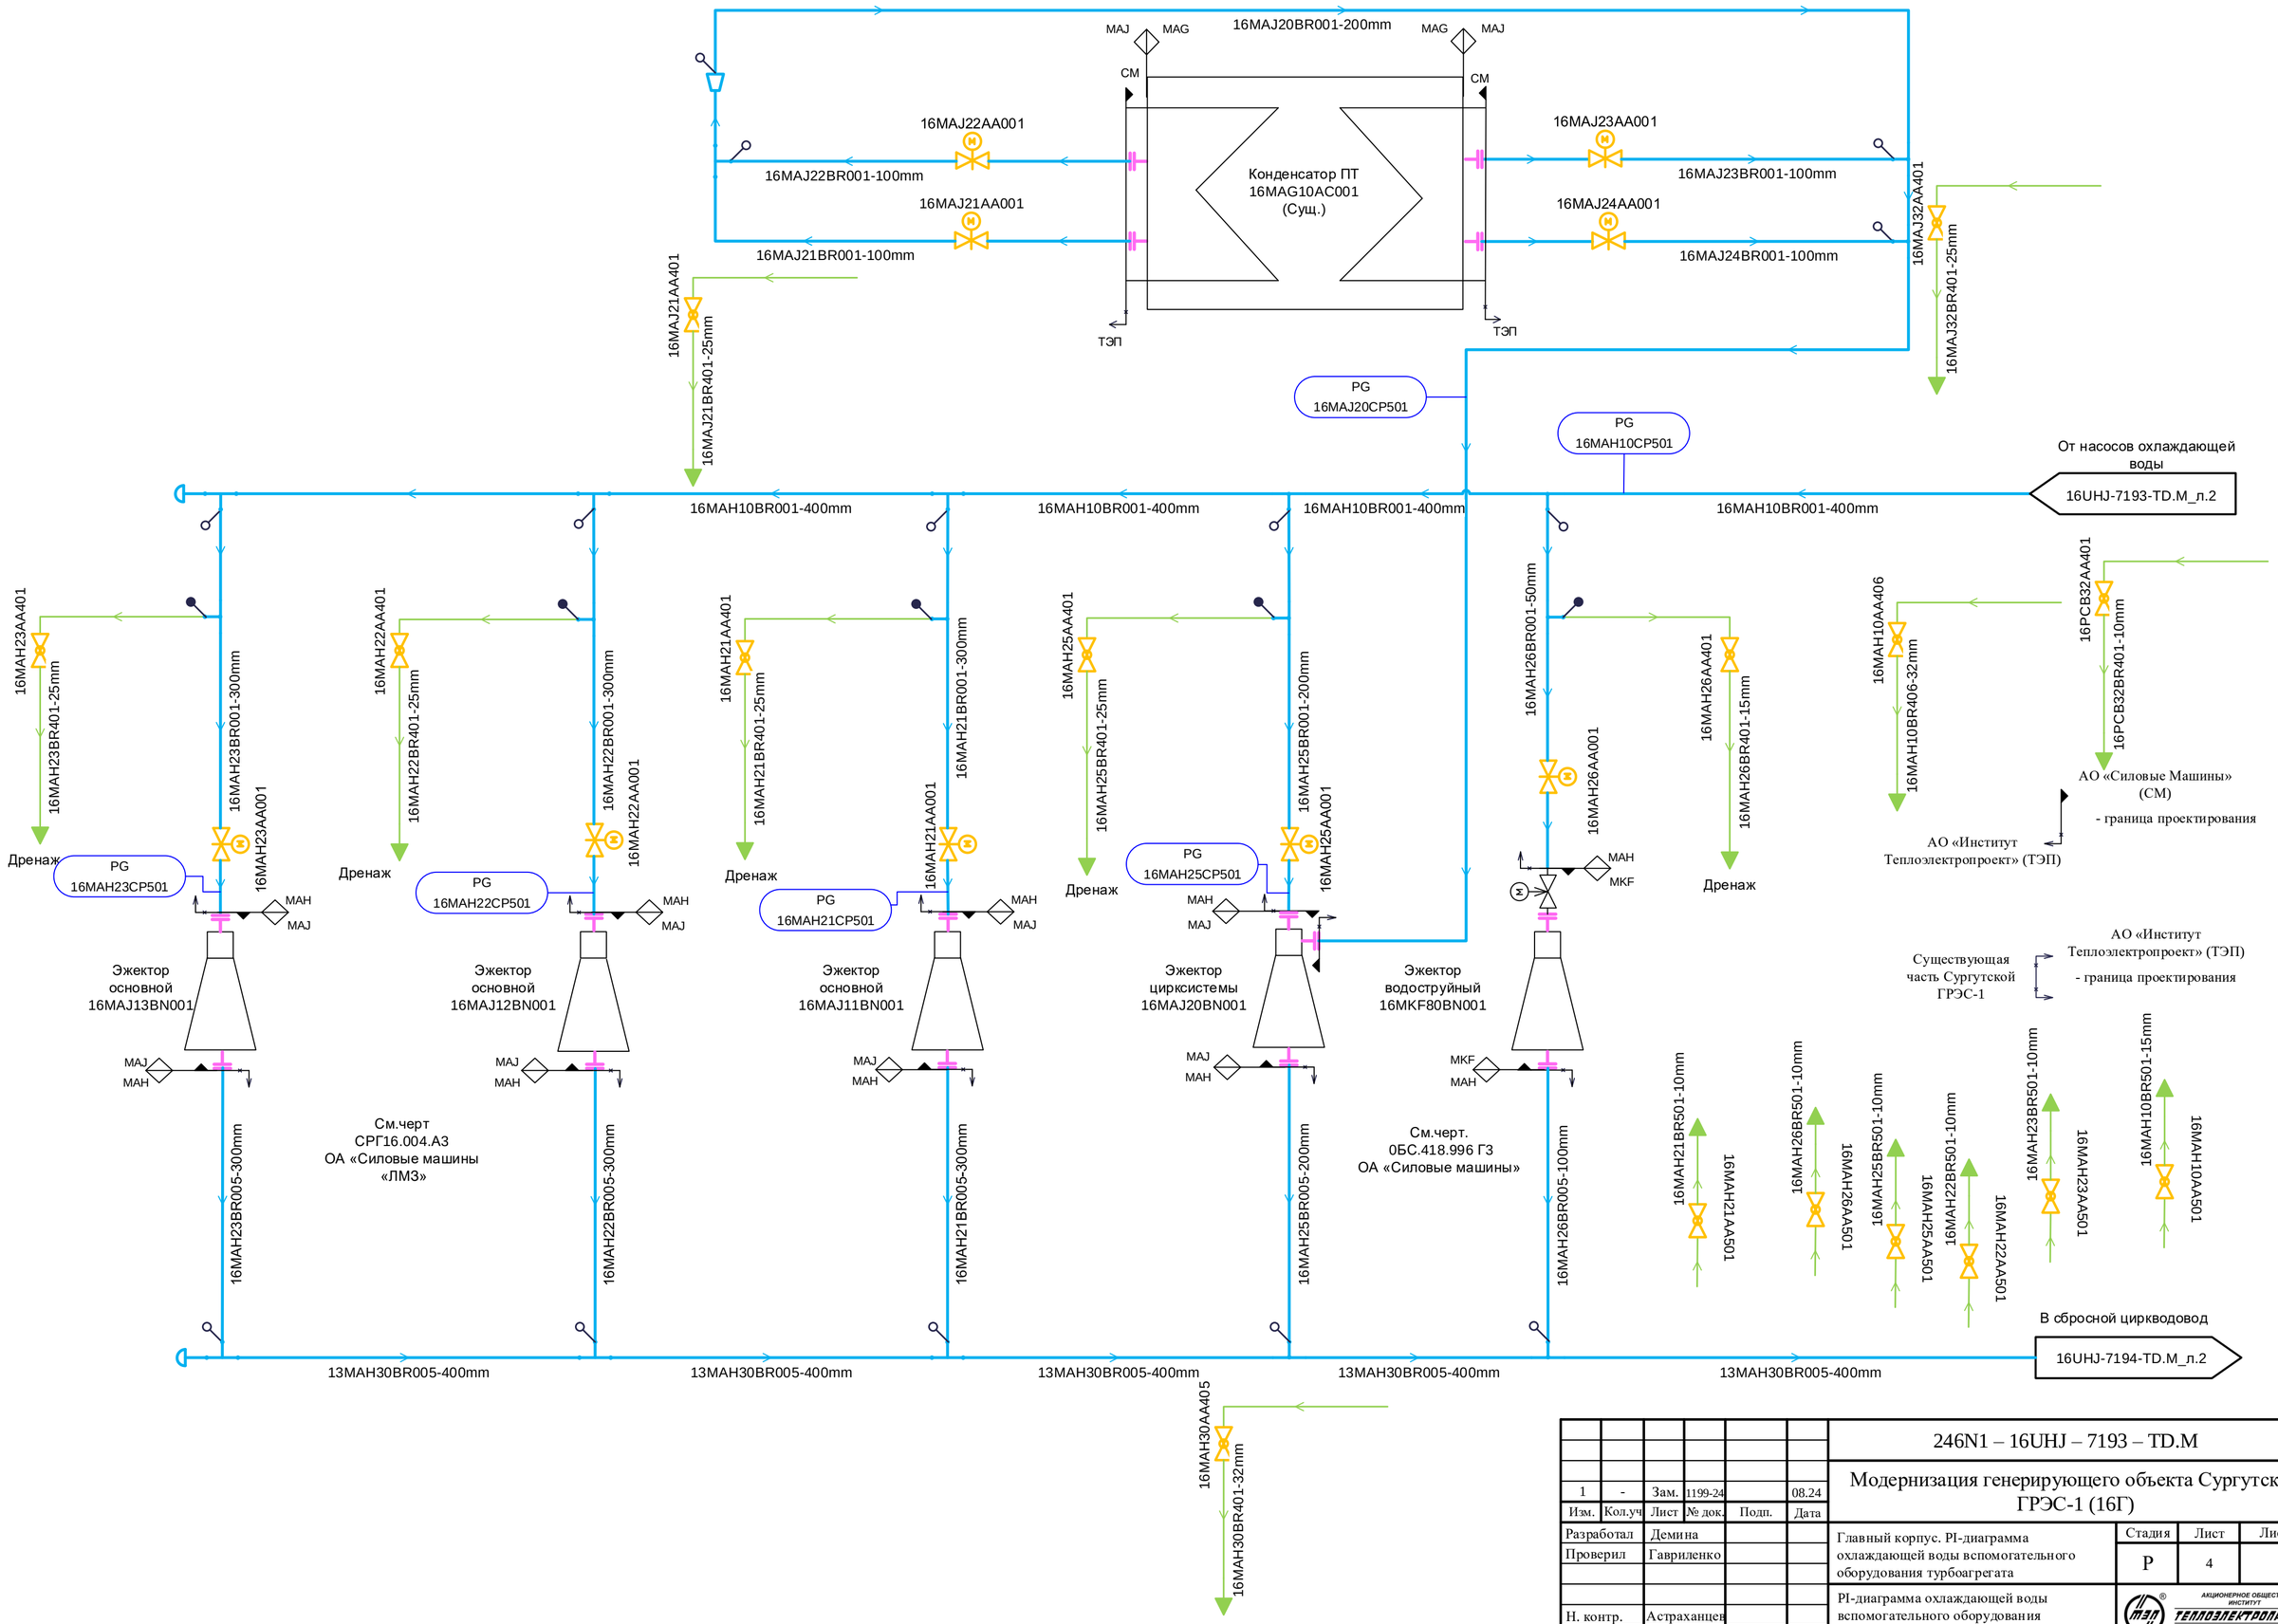

1	-	Зам.	1199-24		08.24	246N1 – 16UHJ – 7193 – TD.M
Изм.	Кол.уч	Лист	№ док.	Подп.	Дата	Модернизация генерирующего объекта Сургутская ГРЭС-1 (16Г)
Разработал		Демина				Главный корпус. PI-диаграмма охлаждающей воды вспомогательного оборудования турбоагрегата
Проверил		Гавриленко				Стадия: Р; Лист: 4; Листов:
Н. контр.		Астраханцев				PI-диаграмма охлаждающей воды вспомогательного оборудования турбоагрегата. Система МАН, МАJ

АКЦИОНЕРНОЕ ОБЩЕСТВО ИНСТИТУТ ТЕПЛОЭЛЕКТРОПРОЕКТ Г. МОСКВА

Согласовано

Взам. инв. №

Подпись и дата

Инв. № подл.

Формат А2