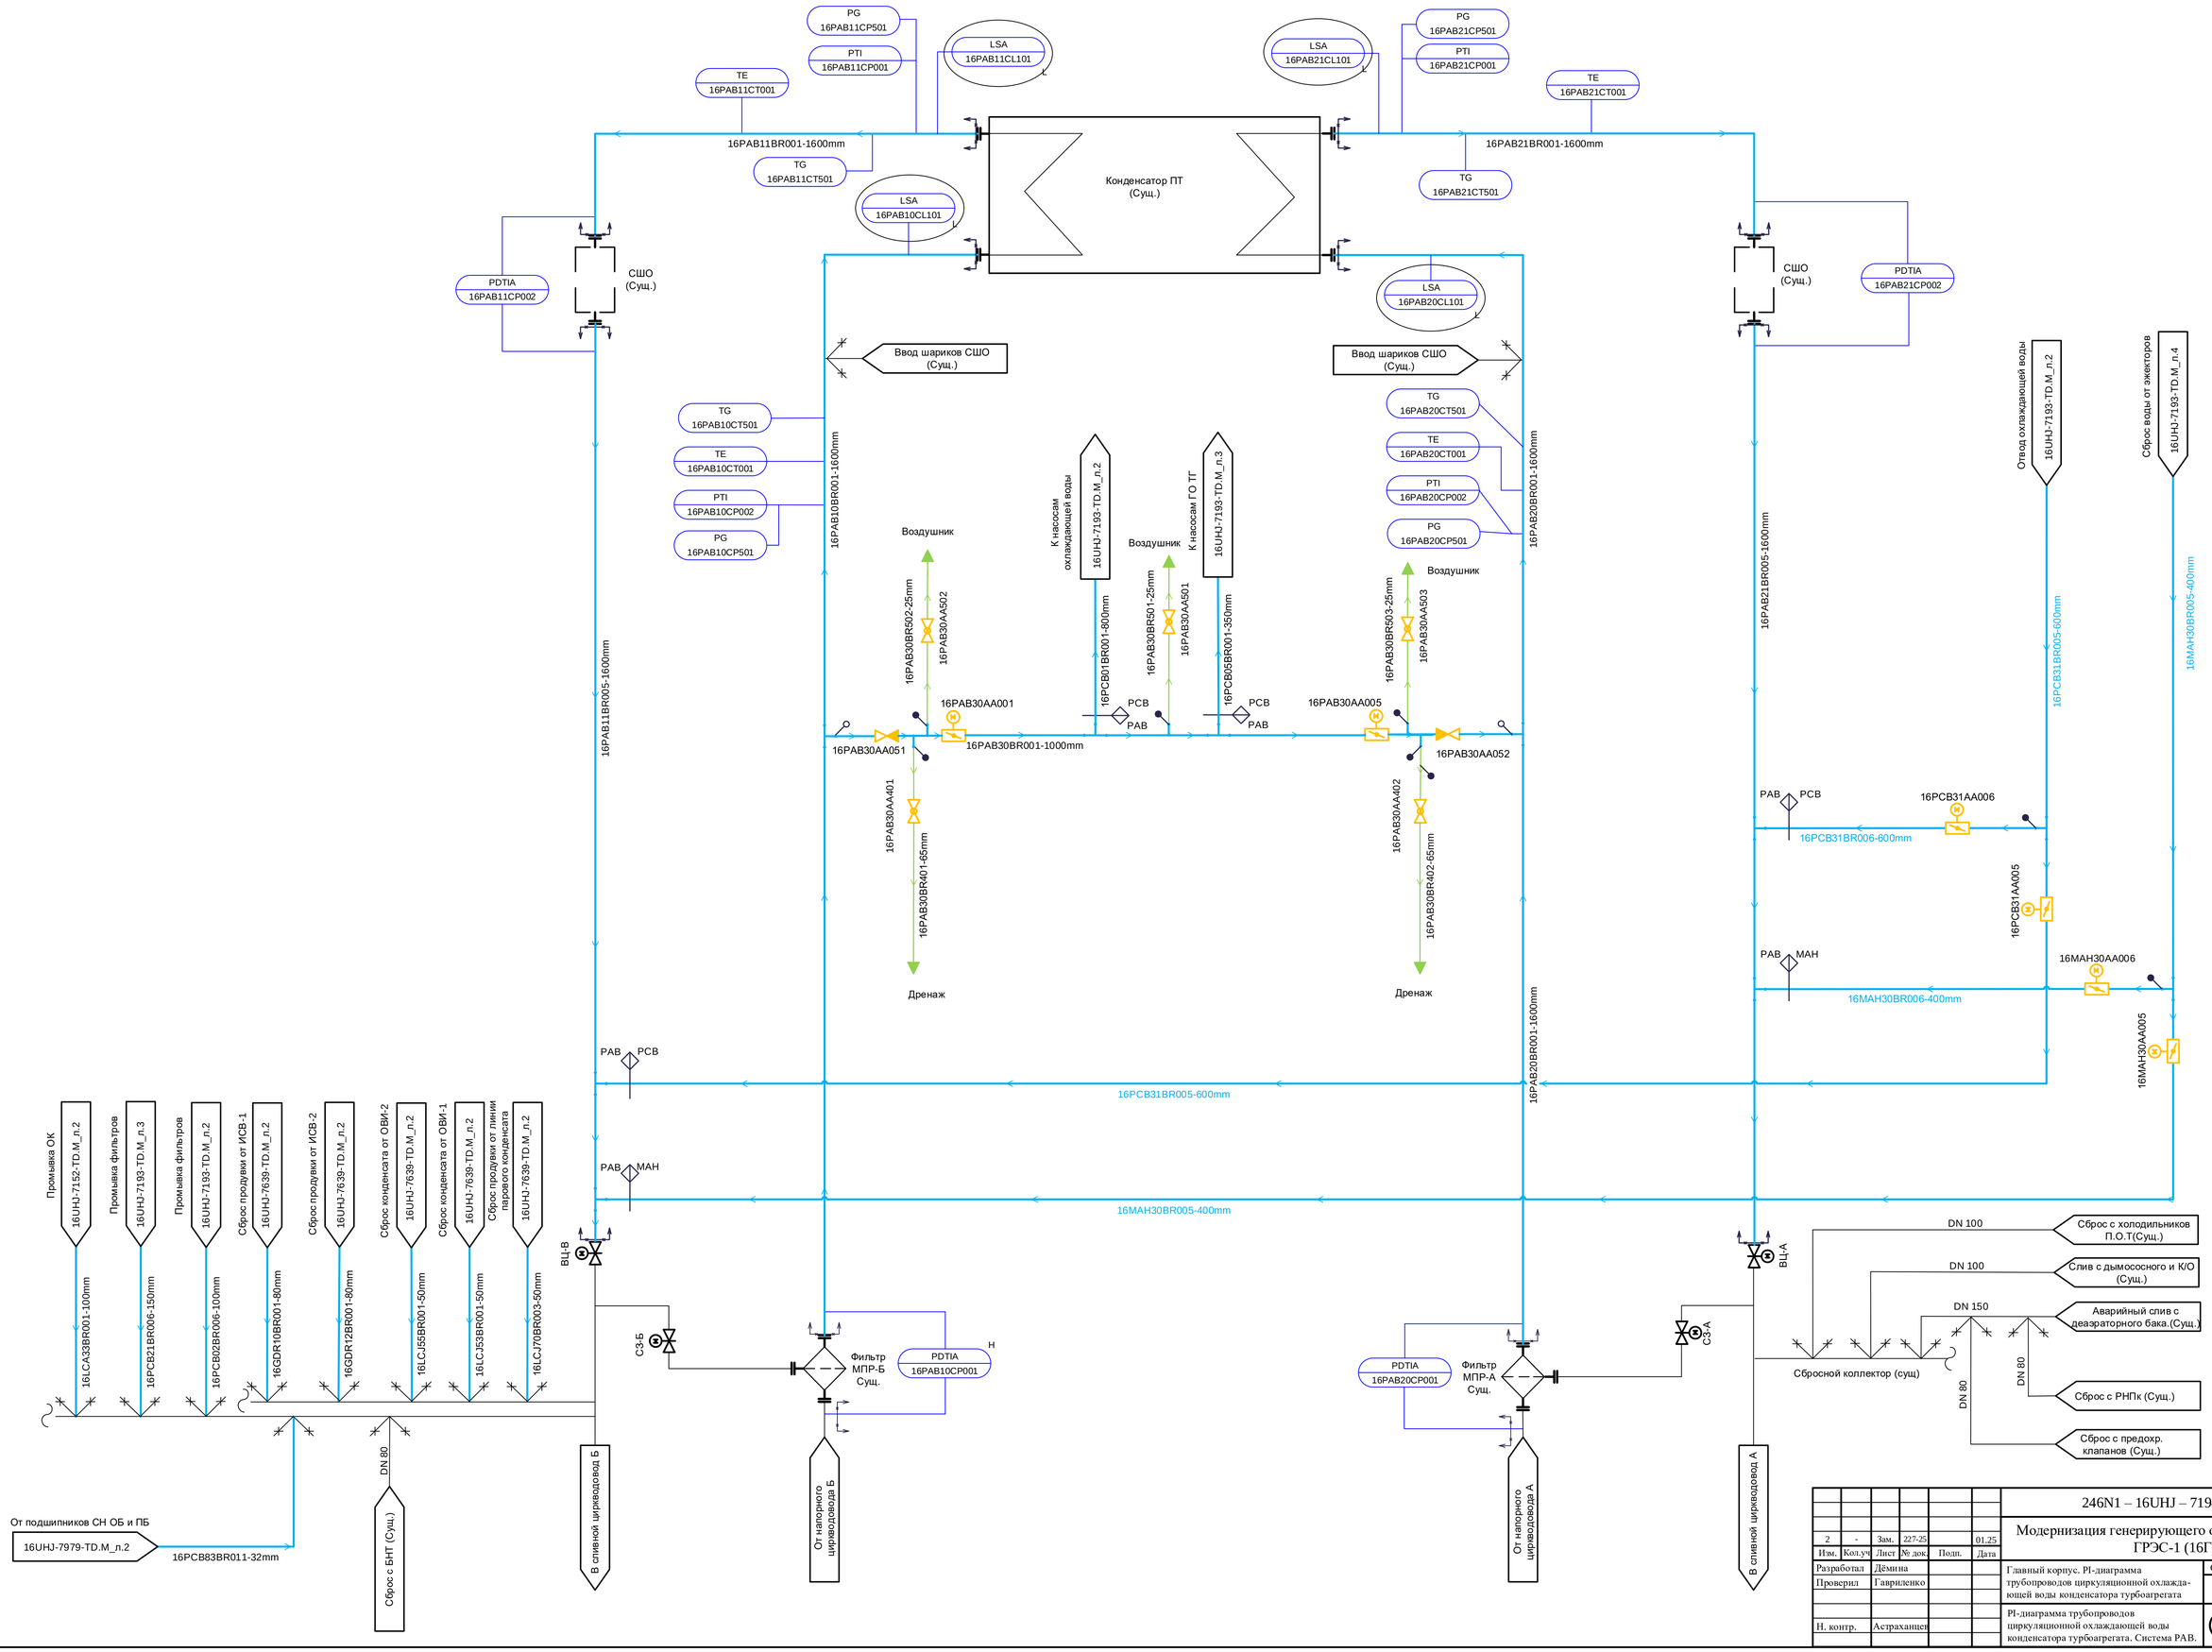

2	-	Зам.	227-25		01.25	
Изм.	Кол.уч	Лист	№ док.	Подп.	Дата	

246N1 – 16UHJ – 7194 – TD.M

Модернизация генерирующего объекта Сургутская ГРЭС-1 (16Г)

Разработал	Дёмина	
Проверил	Гавриленко	
Н. контр.	Астраханцев	

Главный корпус. PI-диаграмма трубопроводов циркуляционной охлаждающей воды конденсатора турбоагрегата

PI-диаграмма трубопроводов циркуляционной охлаждающей воды конденсатора турбоагрегата. Система PAB.

Стадия	Лист	Листов
Р	2	

АКЦИОНЕРНОЕ ОБЩЕСТВО ИНСТИТУТ ТЕПЛОЭЛЕКТРОПРОЕКТ г. МОСКВА

Согласовано

Взам. инв. №

Подпись и дата

Инв. № подл.

Формат А1