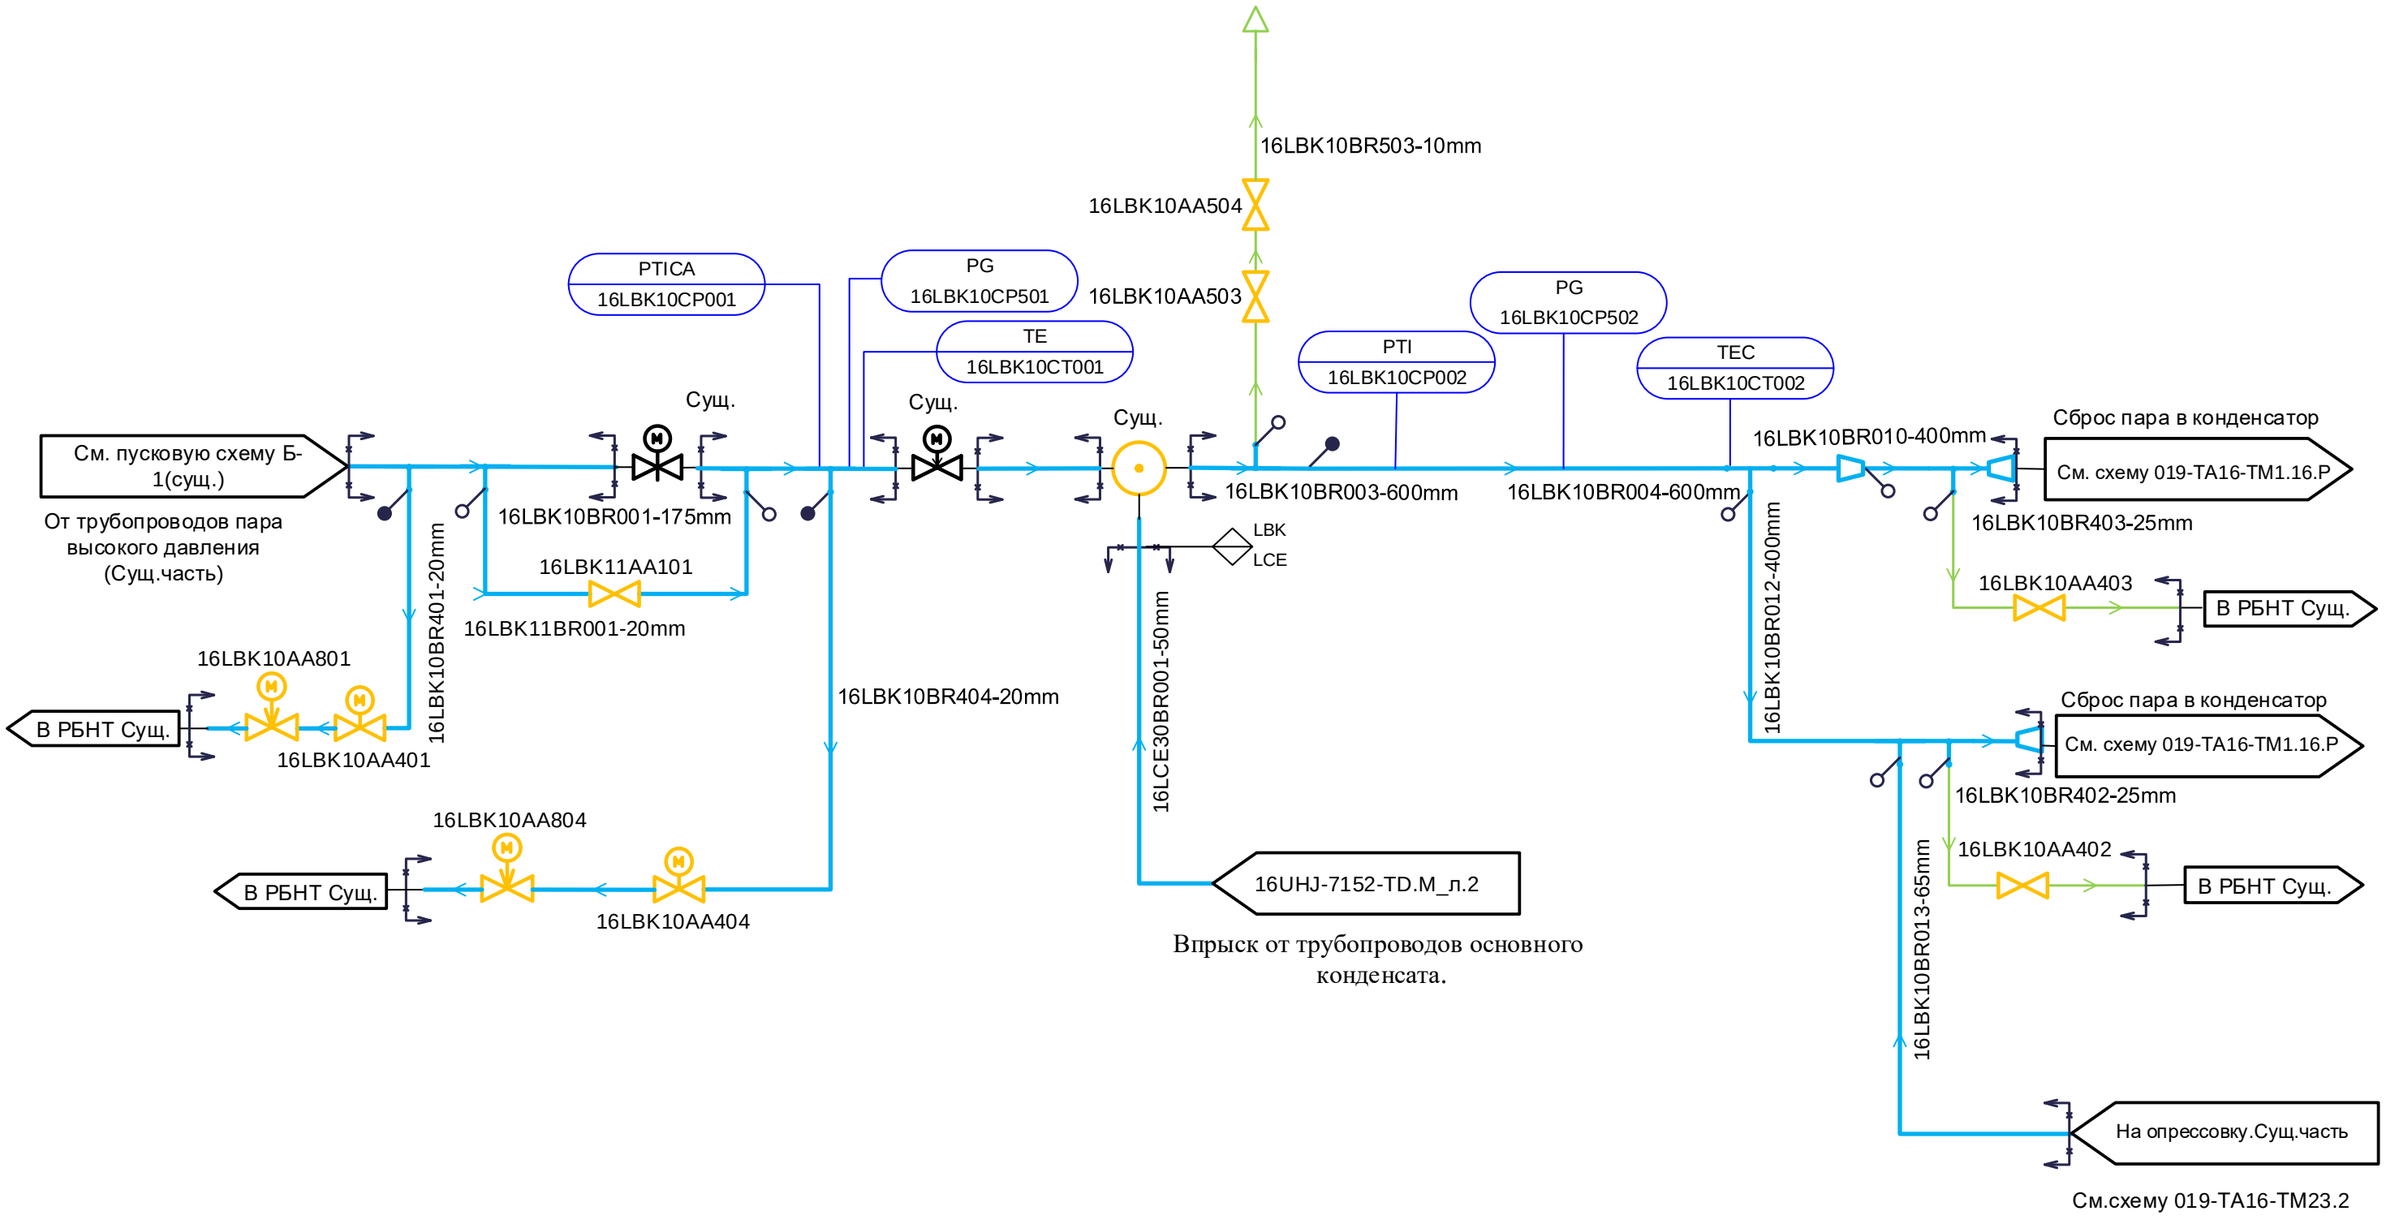

ТЭП
Граница проектирования Сущ./ТЭП
Сущ.

СМ.
Граница проектирования СМ./ТЭП
ТЭП

Согласовано

Взам. инв. №

Подпись и дата

Инв. № подл.

Изм.	Кол.уч	Лист	№ док.	Подп.	Дата
1	-	Зам.	564-24		
Разработал		Гусев.Т			
Проверил		Демина			
Н. контр.		Черемушкина			

246N1-16UHJ-7632-TD.M

Сургутская ГРЭС-1

Главный корпус.
PI-Диаграмма трубопроводов БРОУ

Стадия	Лист	Листов
Р	2	

PI-Диаграмма трубопроводов БРОУ.Система:LBK,LCE.

АКЦИОНЕРНОЕ ОБЩЕСТВО ИНСТИТУТ ТЕПЛОЭЛЕКТРОПРОЕКТ Г. МОСКВА

Формат А3