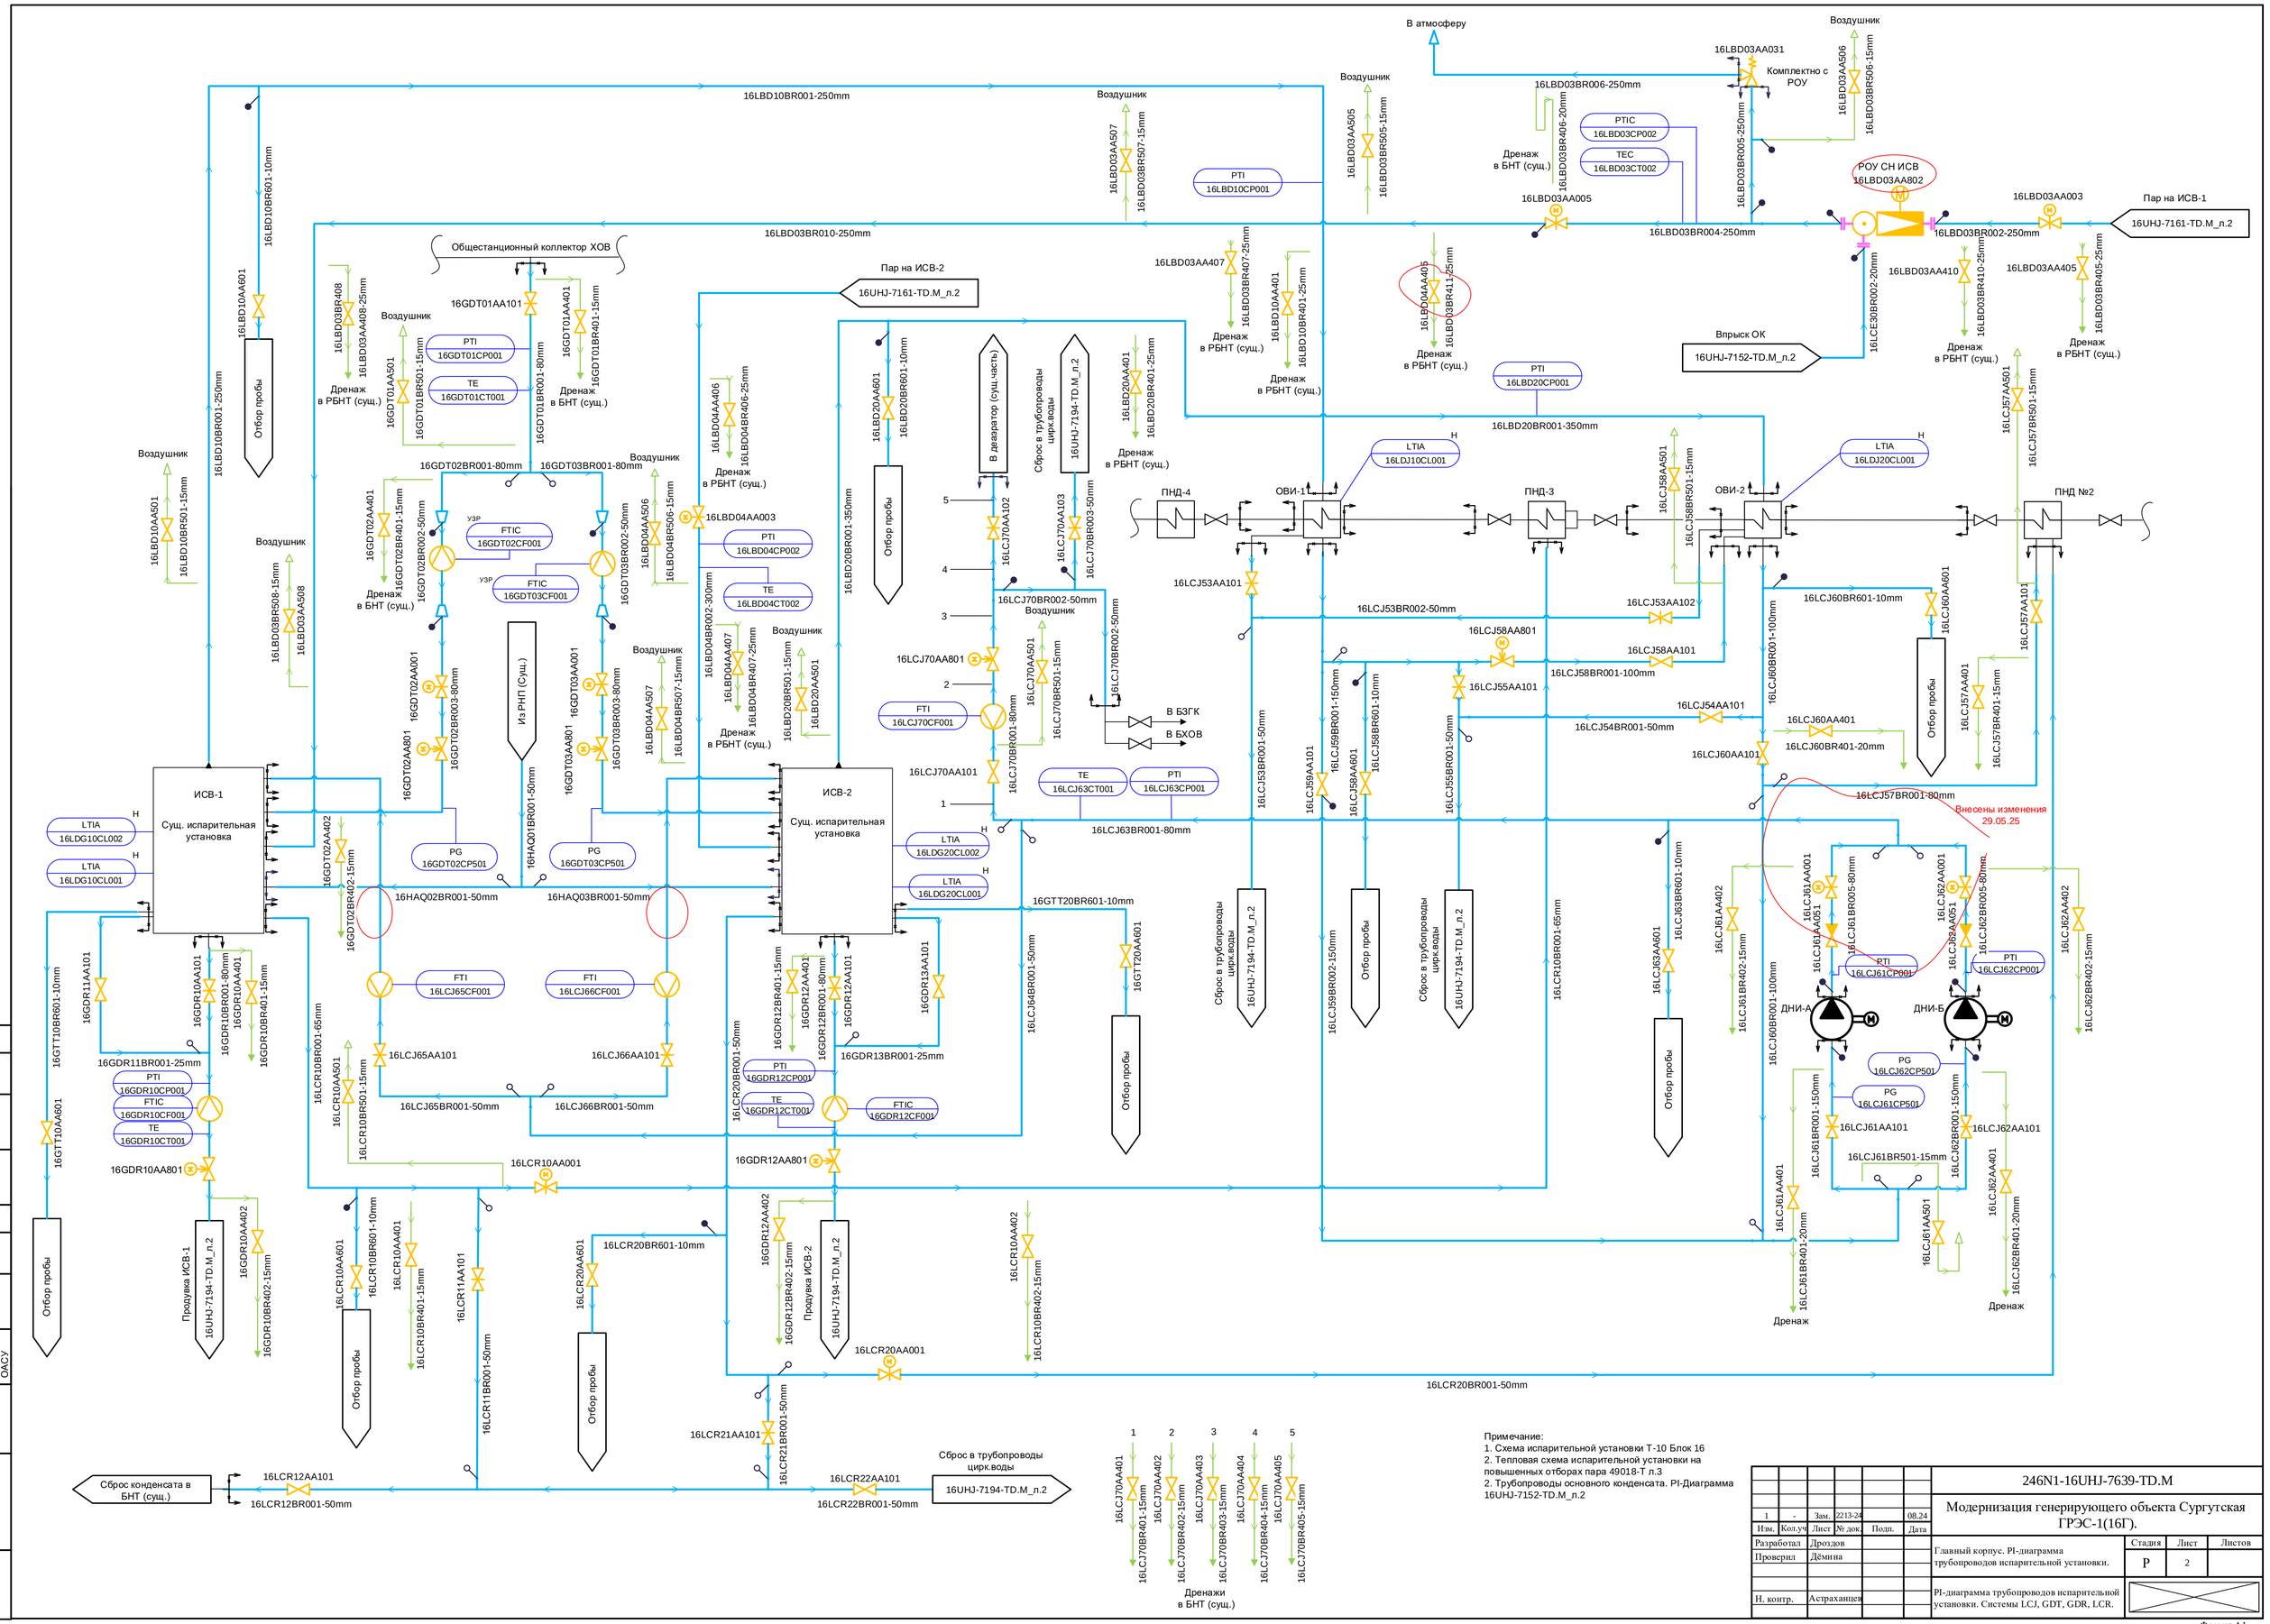

Примечание:
1. Схема испарительной установки Т-10 Блок 16
2. Тепловая схема испарительной установки на повышенных отборах пара 49018-Т л.3
2. Трубопроводы основного конденсата. PI-Диаграмма 16UHJ-7152-TD.M_п.2

1	-	Зам.	2213-24		08.24	246N1-16UHJ-7639-TD.M
Изм.	Кол.уч	Лист	№ док.	Подп.	Дата	Модернизация генерирующего объекта Сургутская ГРЭС-1(16Г).
Разработал		Дроздов				Главный корпус. PI-диаграмма трубопроводов испарительной установки.
Проверил		Дёмина				Стадия: Р; Лист: 2; Листов:
Н. контр.		Астраханцев				PI-диаграмма трубопроводов испарительной установки. Системы LCJ, GDT, GDR, LCR.

Согласовано
ОАСУ
Взам. инв. №
Подпись и дата
Инв. № подл.

Формат А1