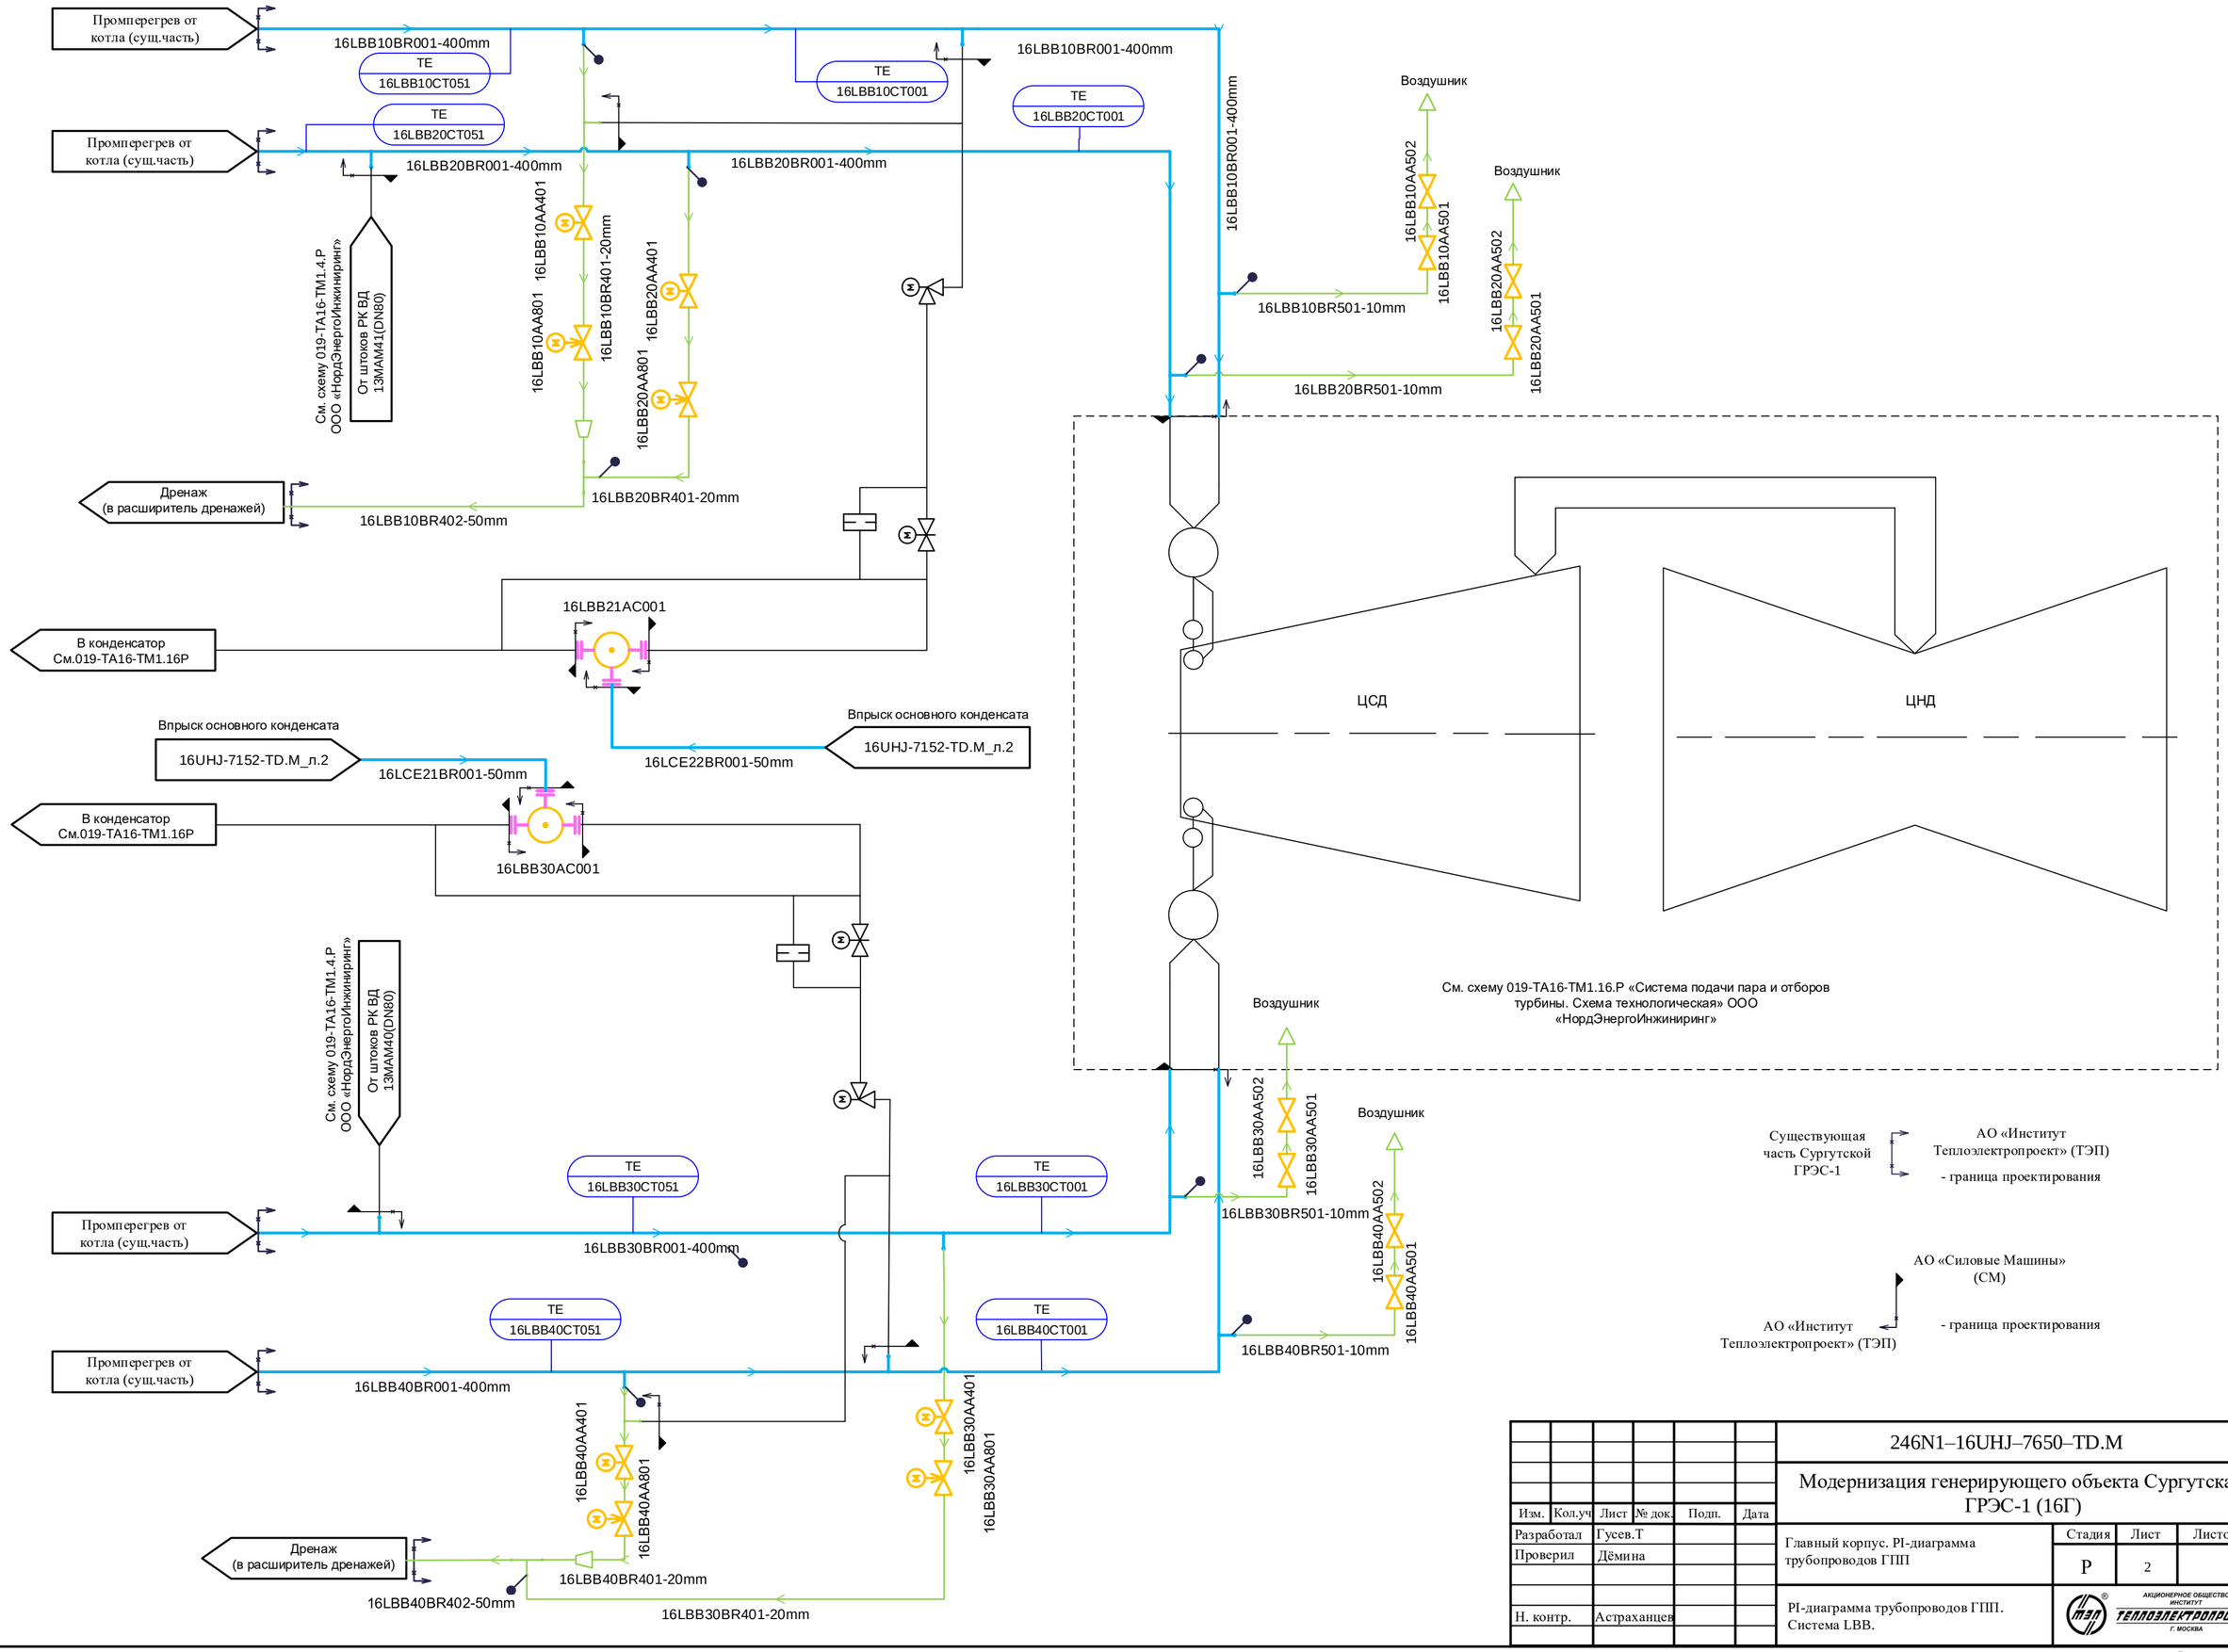

Изм.	Кол.уч	Лист	№ док.	Подп.	Дата
Разработал		Гусев.Т			
Проверил		Дёмина			
Н. контр.		Астраханцев			

246N1–16UHJ–7650–TD.M

Модернизация генерирующего объекта Сургутская ГРЭС-1 (16Г)

Главный корпус. PI-диаграмма трубопроводов ГПП

Стадия	Лист	Листов
Р	2	

PI-диаграмма трубопроводов ГПП. Система LBB.

АКЦИОНЕРНОЕ ОБЩЕСТВО ИНСТИТУТ ТЕПЛОЭЛЕКТРОПРОЕКТ Г. МОСКВА

Согласовано

Взам. инв. №

Подпись и дата

Инв. № подл.

Формат А2