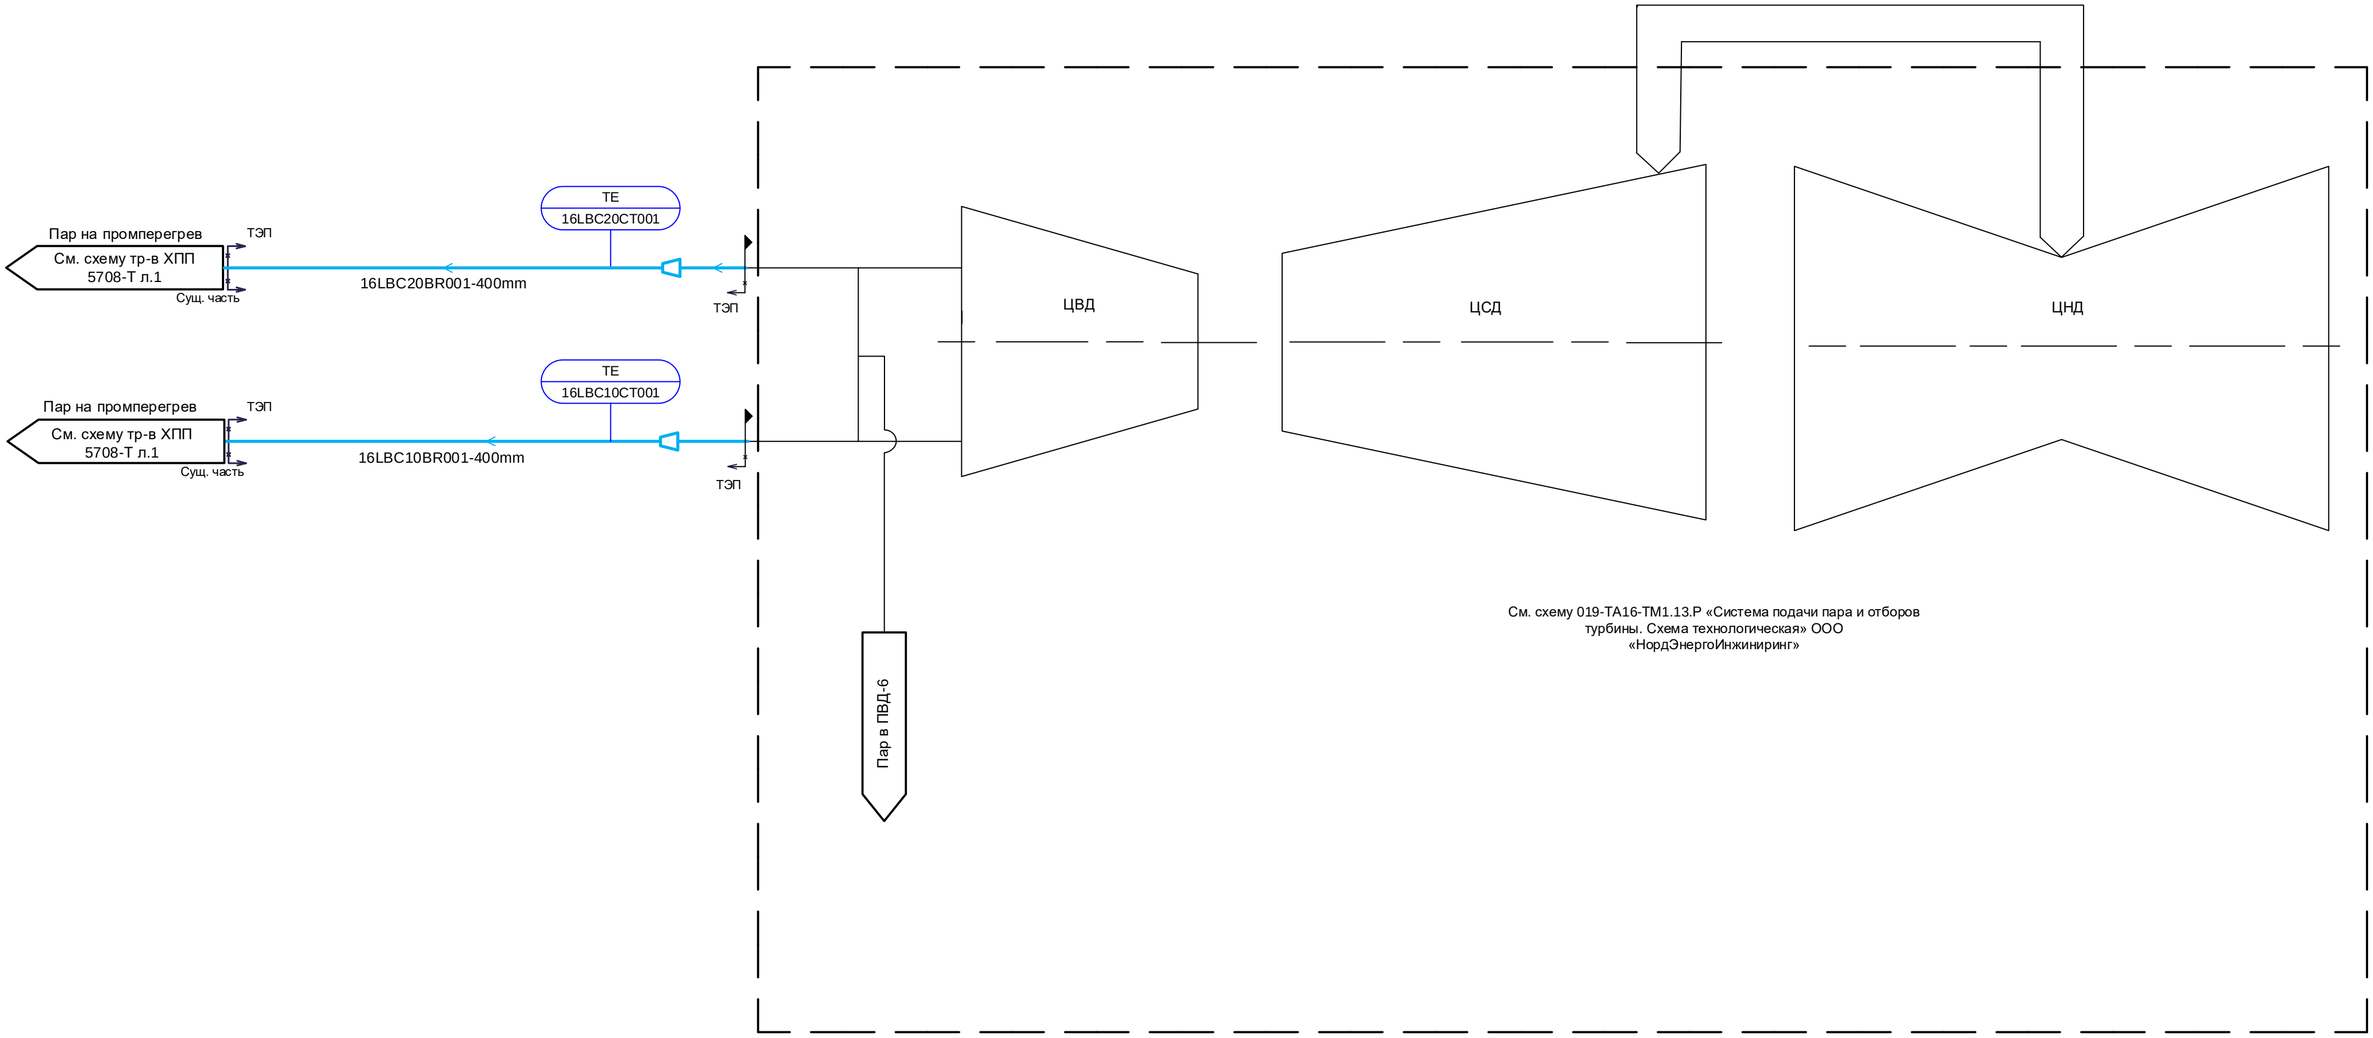

Согласовано

Взам. инв. №

Подпись и дата

Инв. № подл.

Изм.	Кол.уч	Лист	№ док.	Подп.	Дата	246N1–16UHJ–7657–TD.M
						Трубопроводы ХПП и ГПП за пределами ячейки блока 16г
Разработал		Гусев.Т				Главный корпус. PI-диаграмма трубопроводов ХПП
Проверил		Демина				Стадия: Р; Лист: 2; Листов:
Н. контр.		Черемушкина				PI-диаграмма трубопроводов ХПП. Система LBC.

АКЦИОНЕРНОЕ ОБЩЕСТВО ИНСТИТУТ ТЕПЛОЭЛЕКТРОПРОЕКТ Г. МОСКВА

Формат А2