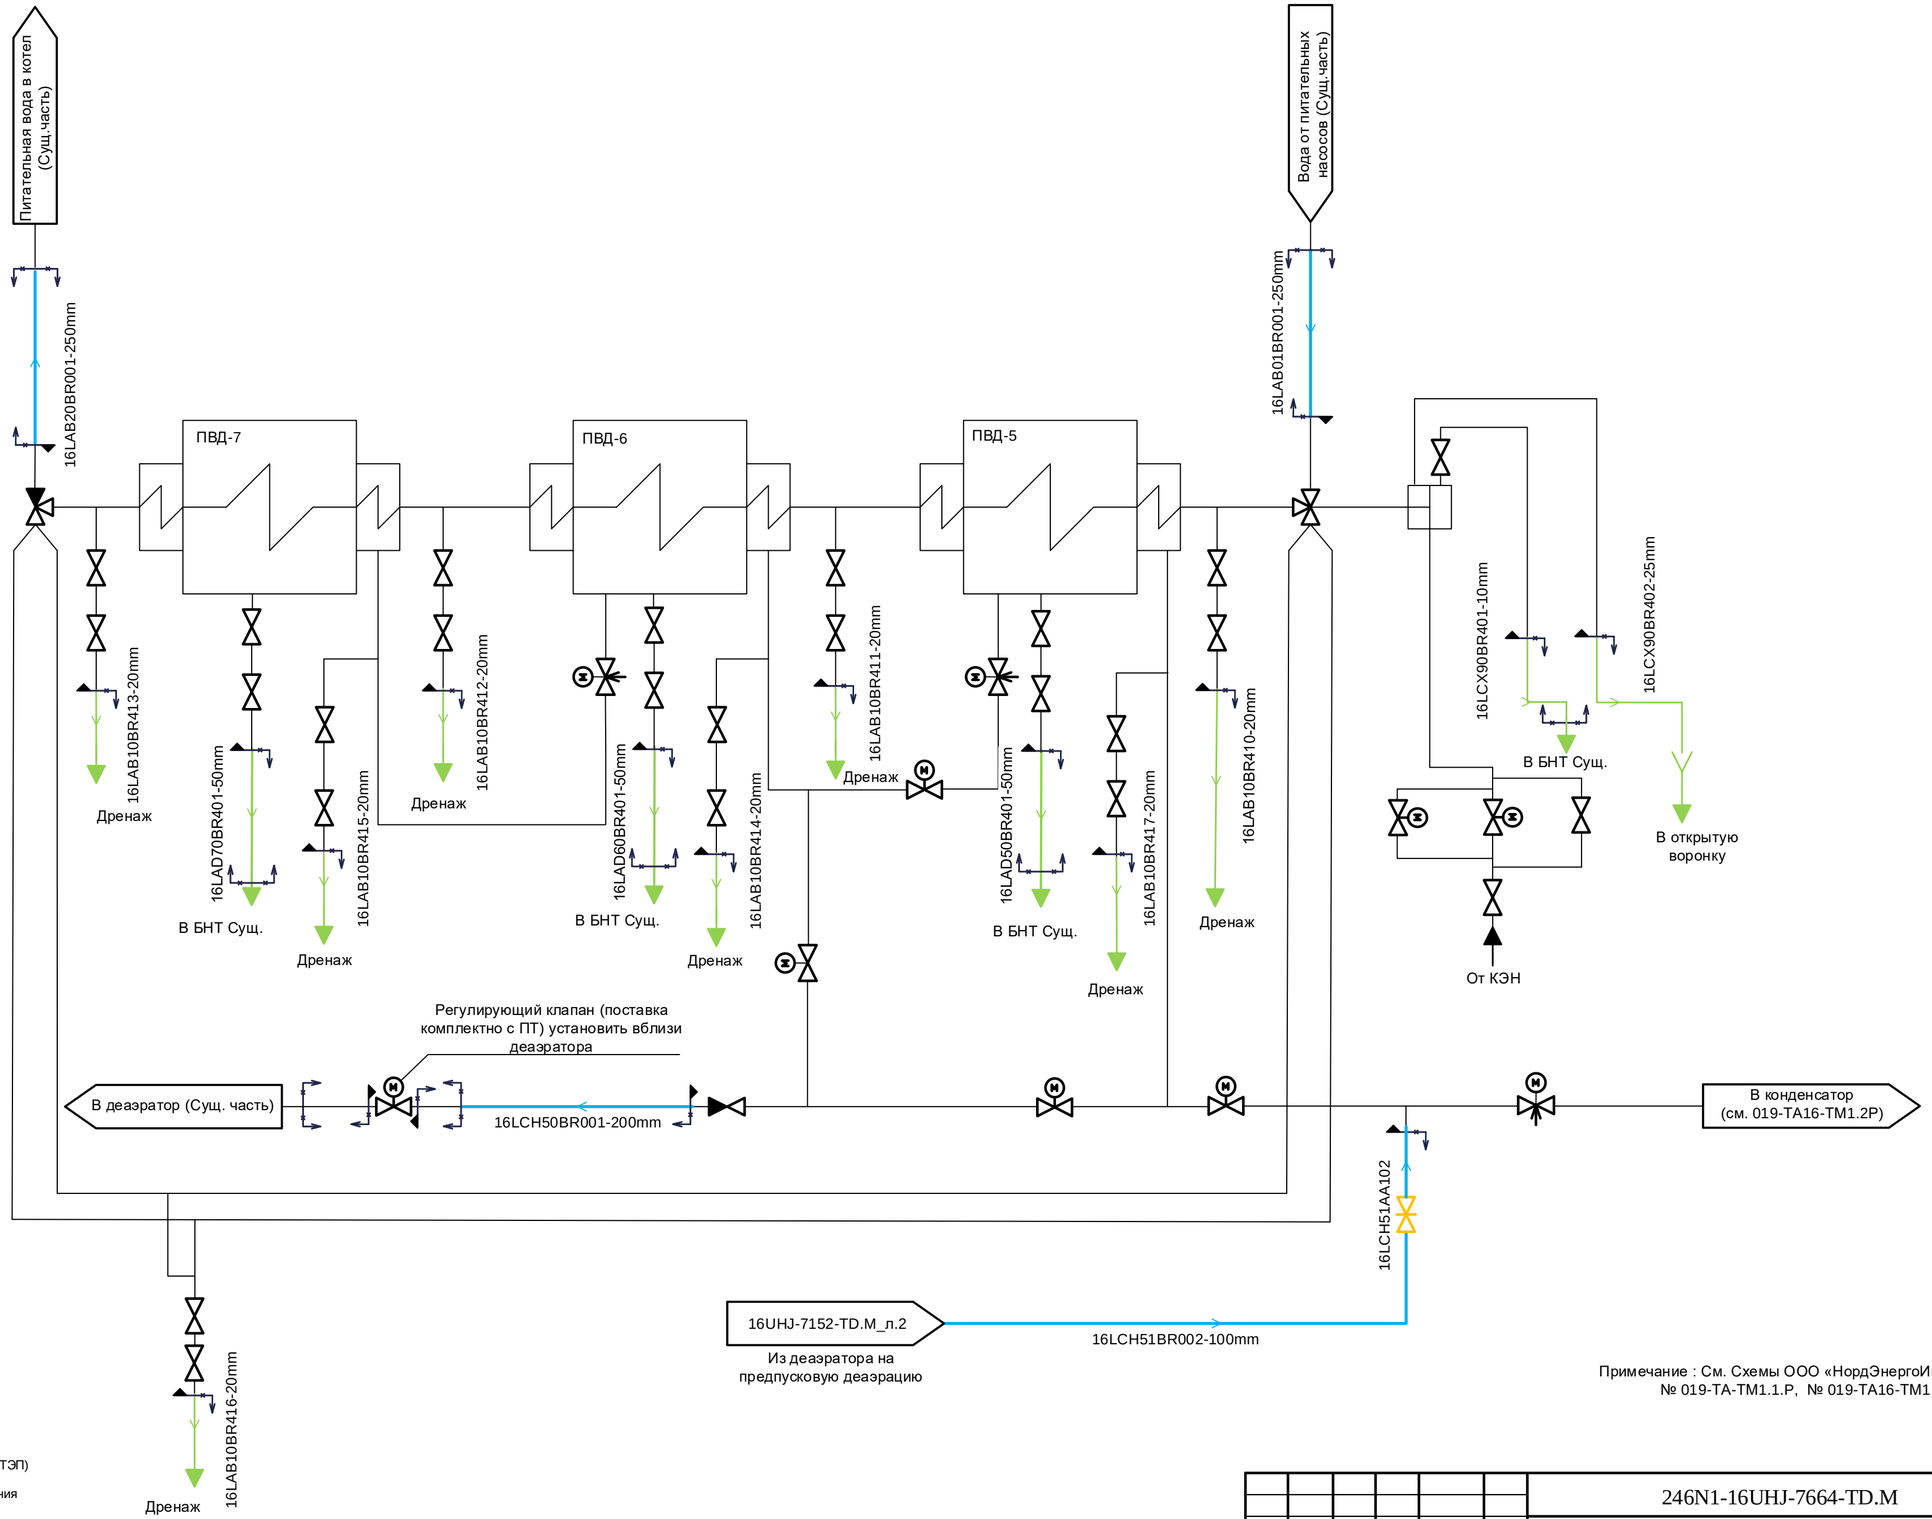

Примечание : См. Схемы ООО «НордЭнергоИнжиниринг» № 019-TA-TM1.1.P, № 019-TA16-TM1.7.P

Существующая часть Сургутской ГРЭС-1

АО «Институт Теплоэлектропроект»(ТЭП)

- граница проектирования

АО «Силовые Машины» (СМ)

- граница проектирования

АО «Институт Теплоэлектропроект»(ТЭП)

Согласовано

Взам. инв. №

Подпись и дата

Инв. № подл.

1	-	Зам.	2213-24		08.24	
Изм.	Кол.уч	Лист	№ док.	Подп.	Дата	
Разработал		Гусев.Т				
Проверил		Демина				
Н. контр.		Черемушкина				

246N1-16UHJ-7664-TD.M

Модернизация генерирующего объекта Сургутская ГРЭС-1(16г)

Главный корпус. Трубопроводы питательной воды.

Стадия	Лист	Листов
Р	2	

Системы LAD,LAB,LCX,LCH.

АКЦИОНЕРНОЕ ОБЩЕСТВО ИНСТИТУТ ТЕПЛОЭЛЕКТРОПРОЕКТ Г. МОСКВА

Формат А2