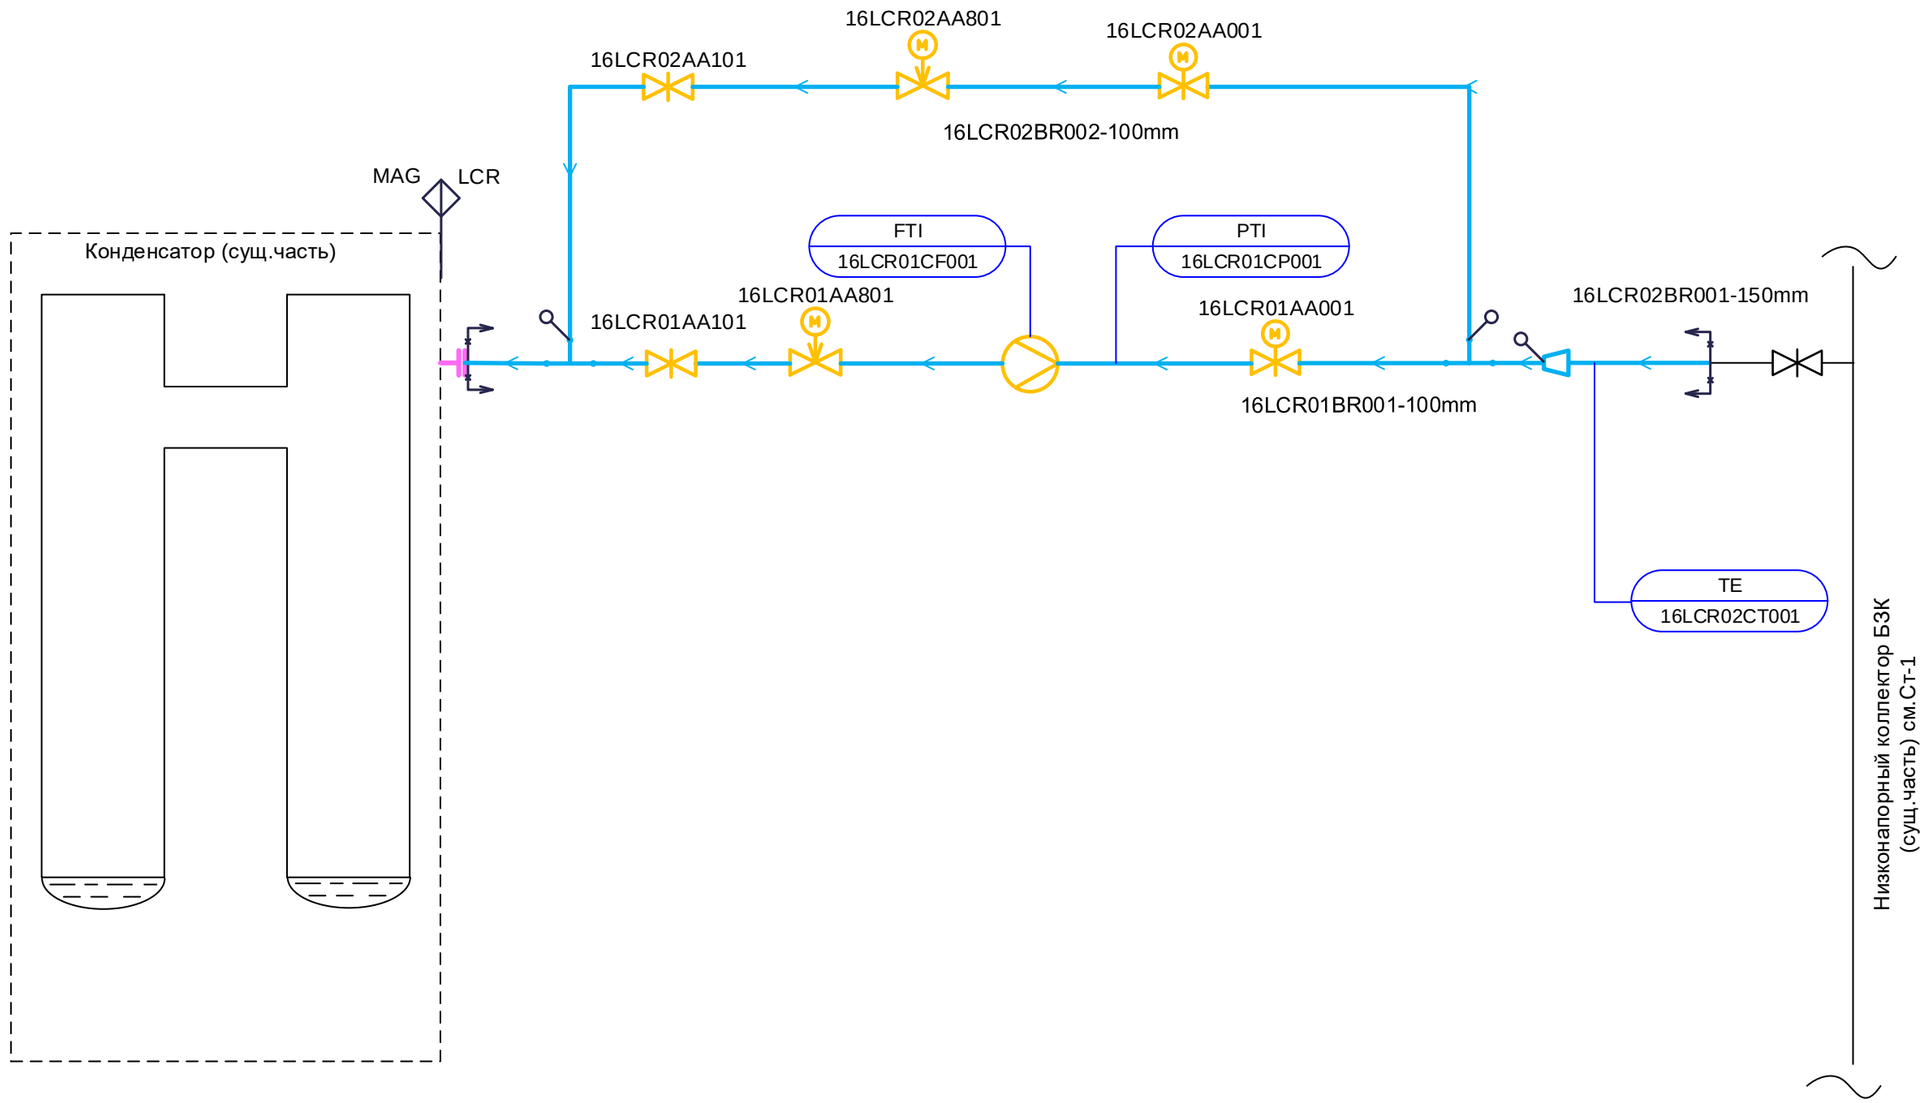

1. Задвижка 16LCR01AA001 на линии постоянного добавка обессоленной воды открывается автоматически при начале открытия РК 16LCR01AA801, закрытие автоматически после полного закрытия РК 16LCR01AA801 с выдержкой времени 20с.
2. Регулирующий клапан расхода постоянного добавка 16LCR01AA801 управляется оператором дистанционно. Задание устанавливается оператором.
3. Задвижка 16LCR02AA001 на байпасной линии постоянного добавка обессоленной воды открывается автоматически при начале открытия РК 16LCR02AA801, закрытие автоматически после полного закрытия РК 16LCR02AA801 с выдержкой времени 20с.
4. Регулирующий клапан расхода на байпасной линии постоянного добавка 16LCR02AA801 управляется оператором дистанционно. Задание устанавливается оператором.

Согласовано

Взам. инв. №

Подпись и дата

Инв. № подл.

Изм.	Кол.уч	Лист	№ док.	Подп.	Дата
2	-	Зам.	774-25		02.25

246N1-16UHJ-7671-TD.M

Модернизация генерирующего объекта Сургутская ГРЭС-1(16Г)

Разработал	Демина	
Проверил	Гавриленко	
Н. контр.	Черемушкина	

Главный корпус.PI-Диаграмма трубопроводов аварийной и постоянной подпитки конденсатора.

Стадия	Лист	Листов
Р	2	

PI-Диаграмма трубопроводов аварийной и постоянной подпитки конденсатора. Система LCR.

АКЦИОНЕРНОЕ ОБЩЕСТВО ИНСТИТУТ ТЕПЛОЭЛЕКТРОПРОЕКТ Г. МОСКВА

Формат А3