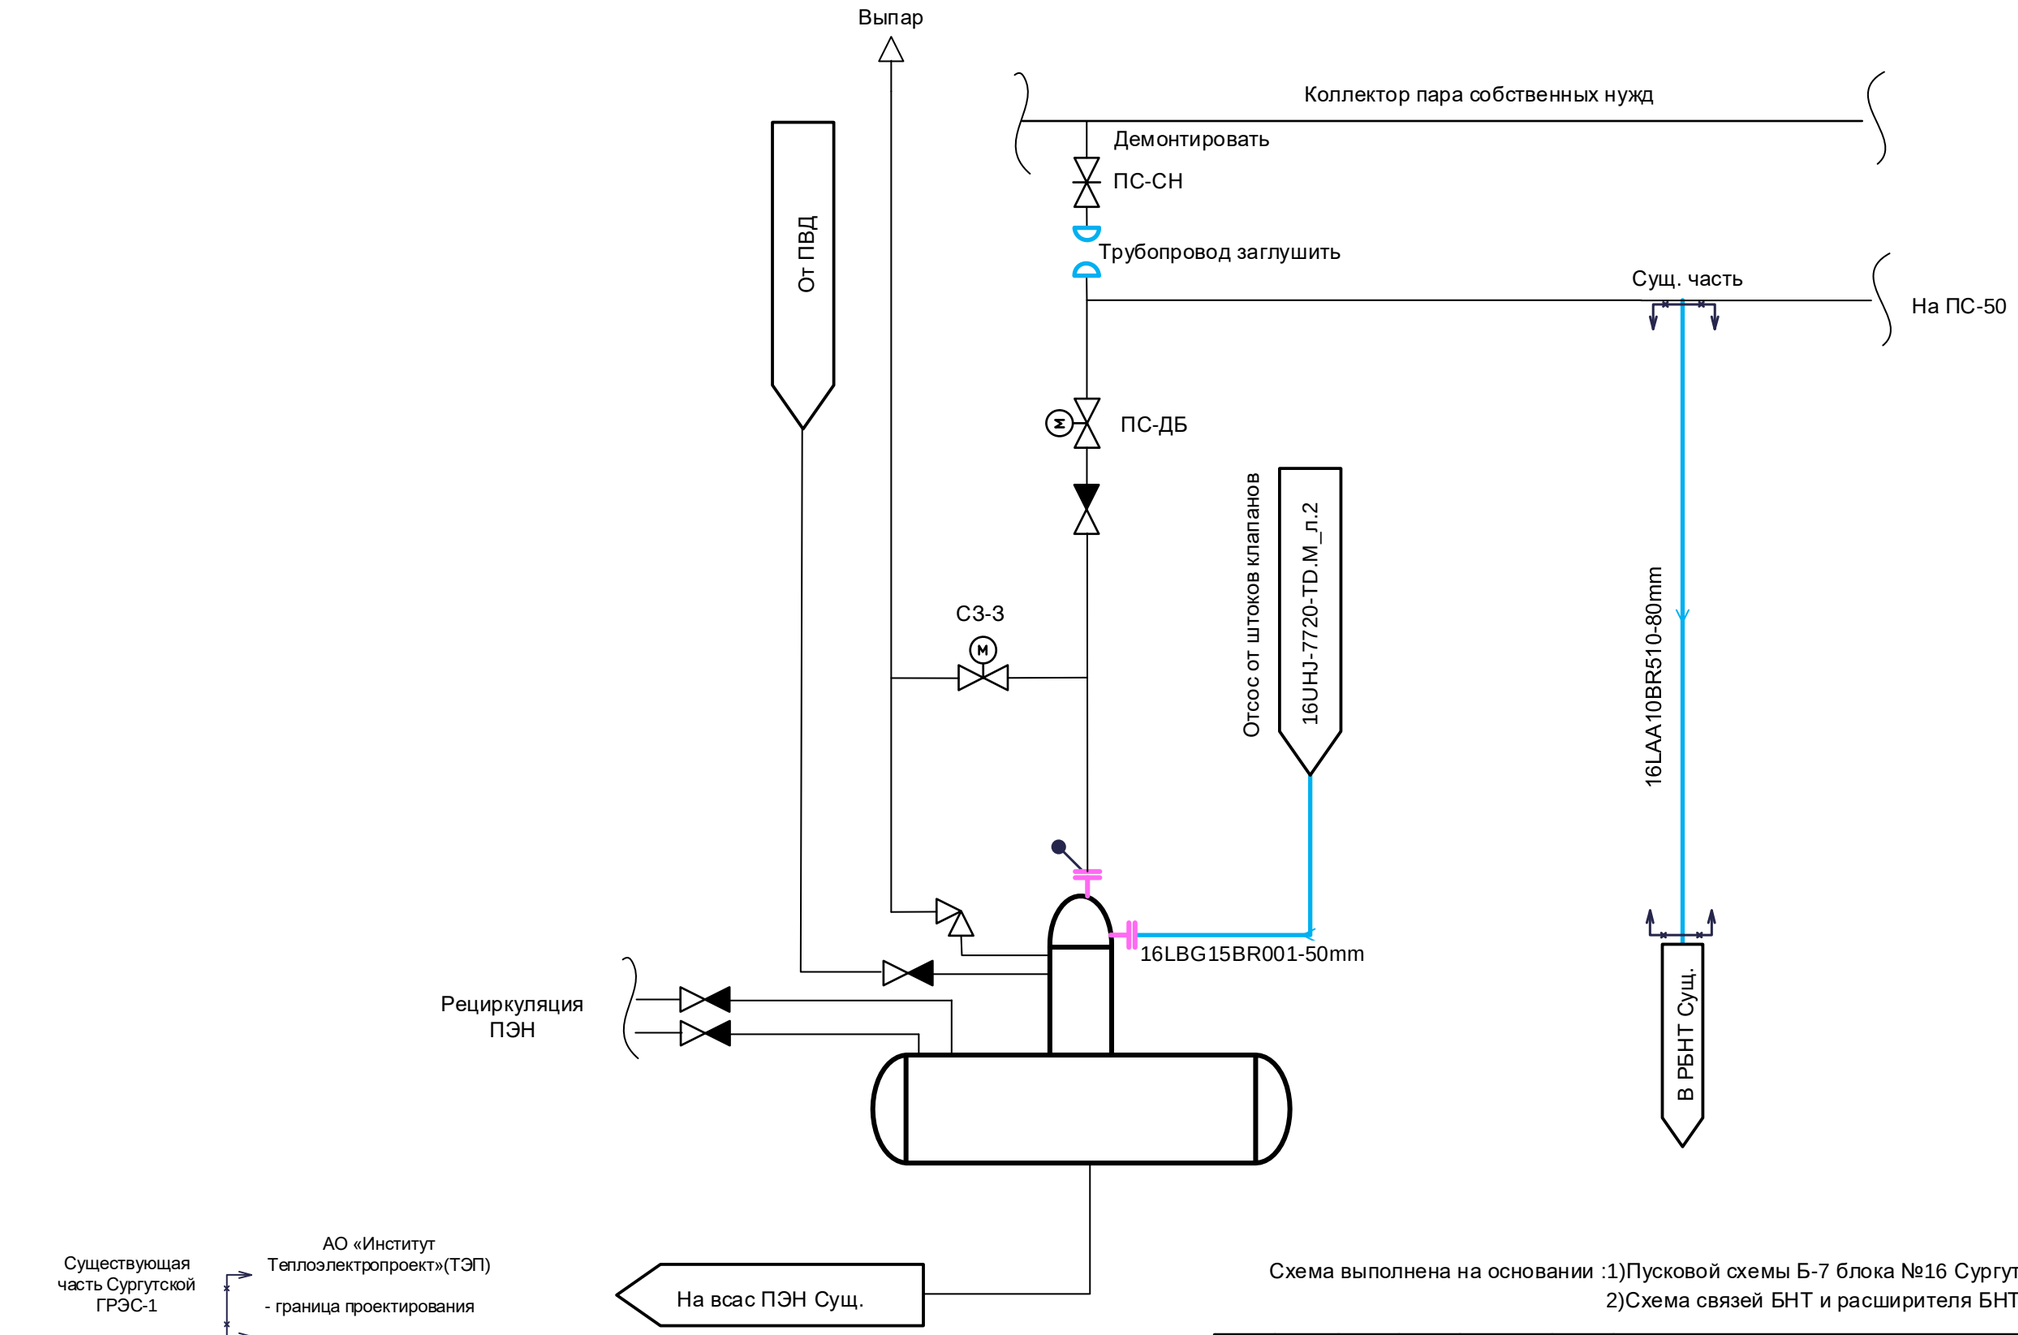

Существующая часть Сургутской ГРЭС-1

АО «Институт Теплоэлектропроект»(ТЭП)

- граница проектирования

АО «Силовые Машины» (СМ)

- граница проектирования

АО «Институт Теплоэлектропроект»(ТЭП)

Схема выполнена на основании :1)Пусковой схемы Б-7 блока №16 Сургутская ГРЭС-1.
2)Схема связей БНТ и расширителя БНТ Т-18

Согласовано

Взам. инв. №

Подпись и дата

Инв. № подл.

Изм.	Кол.уч	Лист	№ док.	Подп.	Дата
1	-	Зам.	2213-24		08.24

246N1-16UHJ-7678-TD.M

Модернизация генерирующего объекта Сургутская ГРЭС-1(16г)

Разработал	Гусев.Т	
Проверил	Демина	
Н. контр.	Черемушкина	

Главный корпус. PI-диаграмма трубопровода выпара деаэратора.

Стадия	Лист	Листов
Р	2	

PI-диаграмма трубопровода выпара деаэратора. Система LAA, LCH.

АКЦИОНЕРНОЕ ОБЩЕСТВО ИНСТИТУТ ТЕПЛОЭЛЕКТРОПРОЕКТ Г. МОСКВА

Формат А3