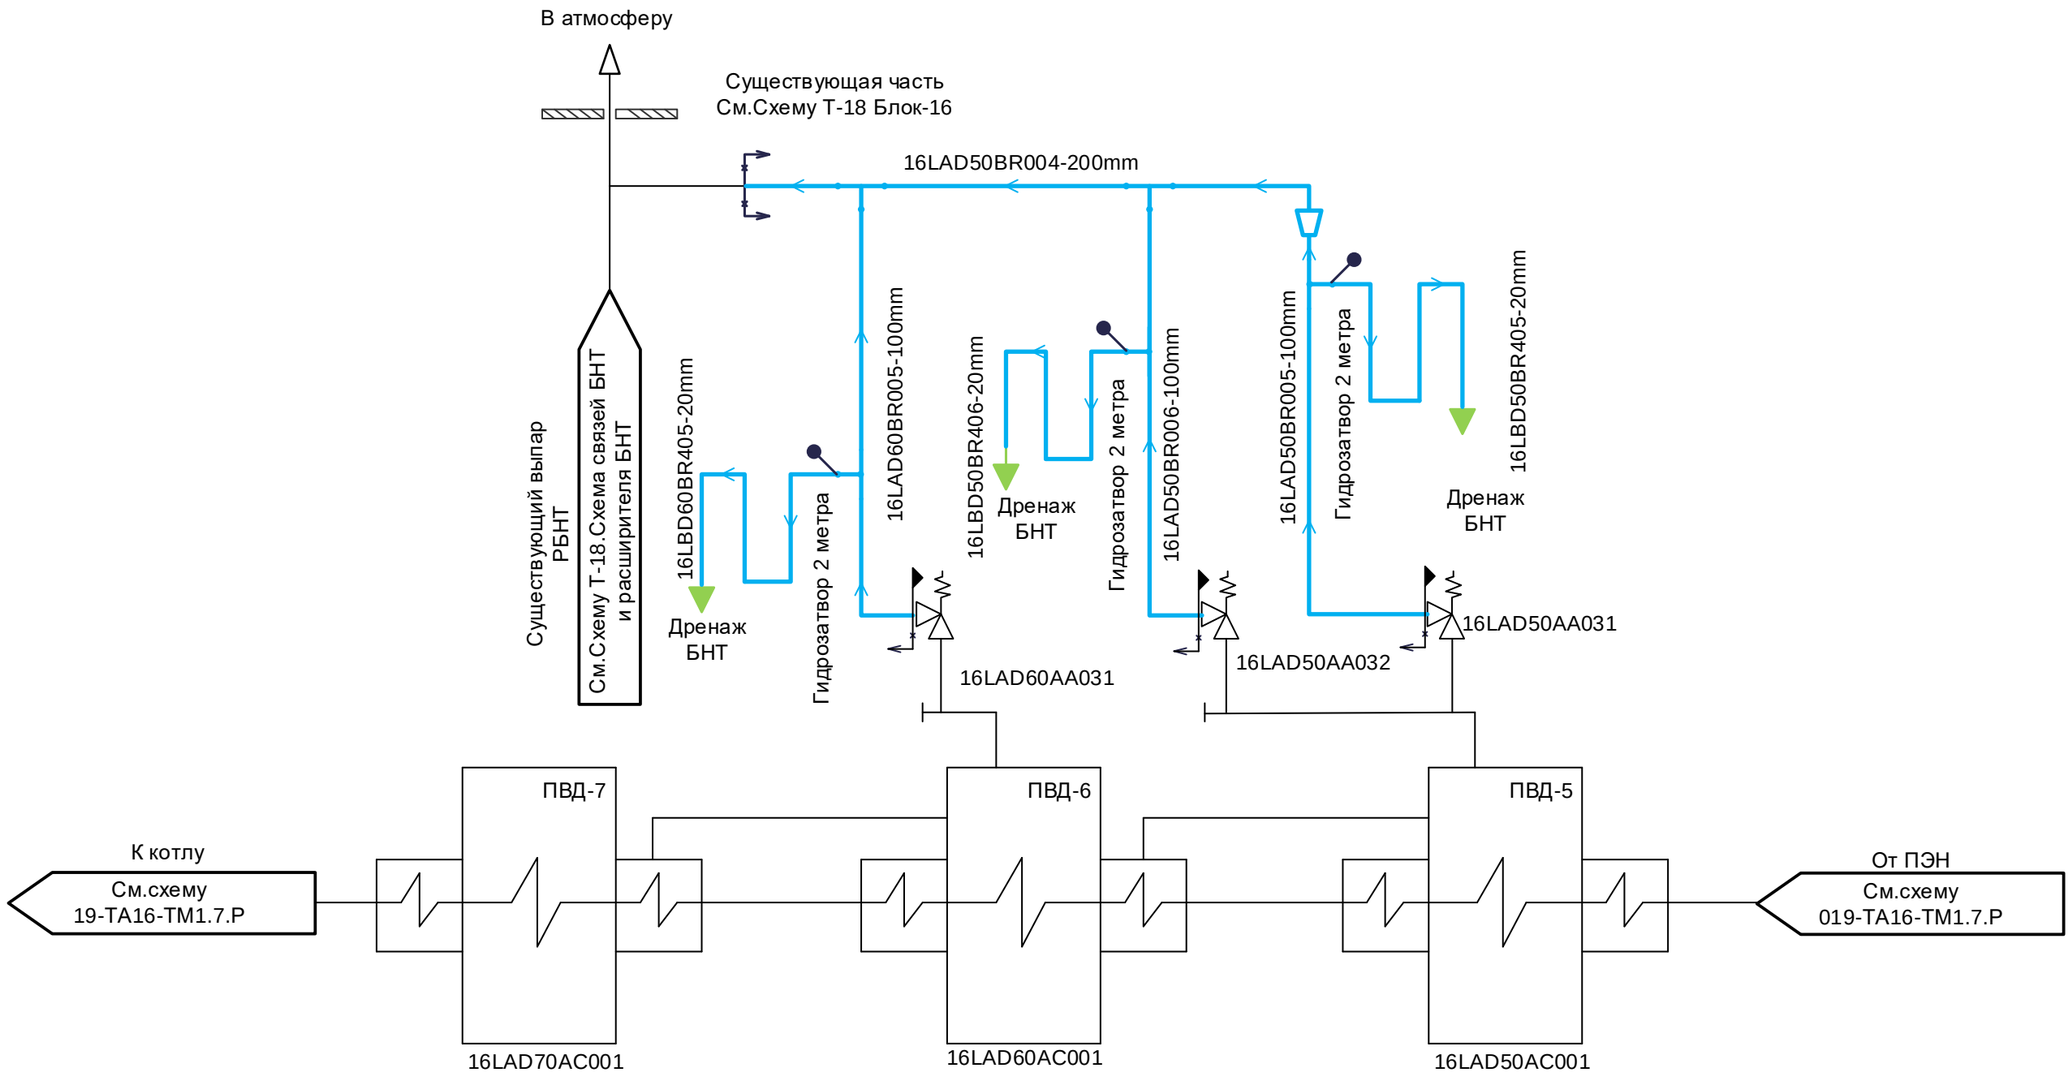

Примечание : См. Тепловую схему ООО «НордЭнергоИнжиниринг» № 019-ТА16-ТМ1.1.Р изм.8
Сх. ООО «НордЭнергоИнжиниринг» № 019-ТА16-ТМ1.7.Р

Существующая часть Сургутской ГРЭС-1 — АО «Институт Теплоэлектропроект»(ТЭП) — - граница проектирования

АО «Силовые Машины» (СМ) — - граница проектирования — АО «Институт Теплоэлектропроект»(ТЭП)

Согласовано

Взам. инв. №

Подпись и дата

Инв. № подл.

Изм.	Кол.уч	Лист	№ док.	Подп.	Дата
2	-	Зам.	3438-24		11.24

246N1 – 16UHJ – 7727 – TD.M

Модернизация генерирующего объекта Сургутская ГРЭС-1 (16Г)

Разработал	Гусев Т.	
Проверил	Демина	
Н. контр.	Черемушкина	

Главный корпус. PI-диаграмма трубопровода сброса пара с предохранительных клапанов ПВД.

Стадия	Лист	Листов
Р	2	

PI-диаграмма трубопровода сброса пара с предохранительных клапанов ПВД. Система LAD.

АКЦИОНЕРНОЕ ОБЩЕСТВО ИНСТИТУТ ТЕПЛОЭЛЕКТРОПРОЕКТ Г. МОСКВА

Формат А3