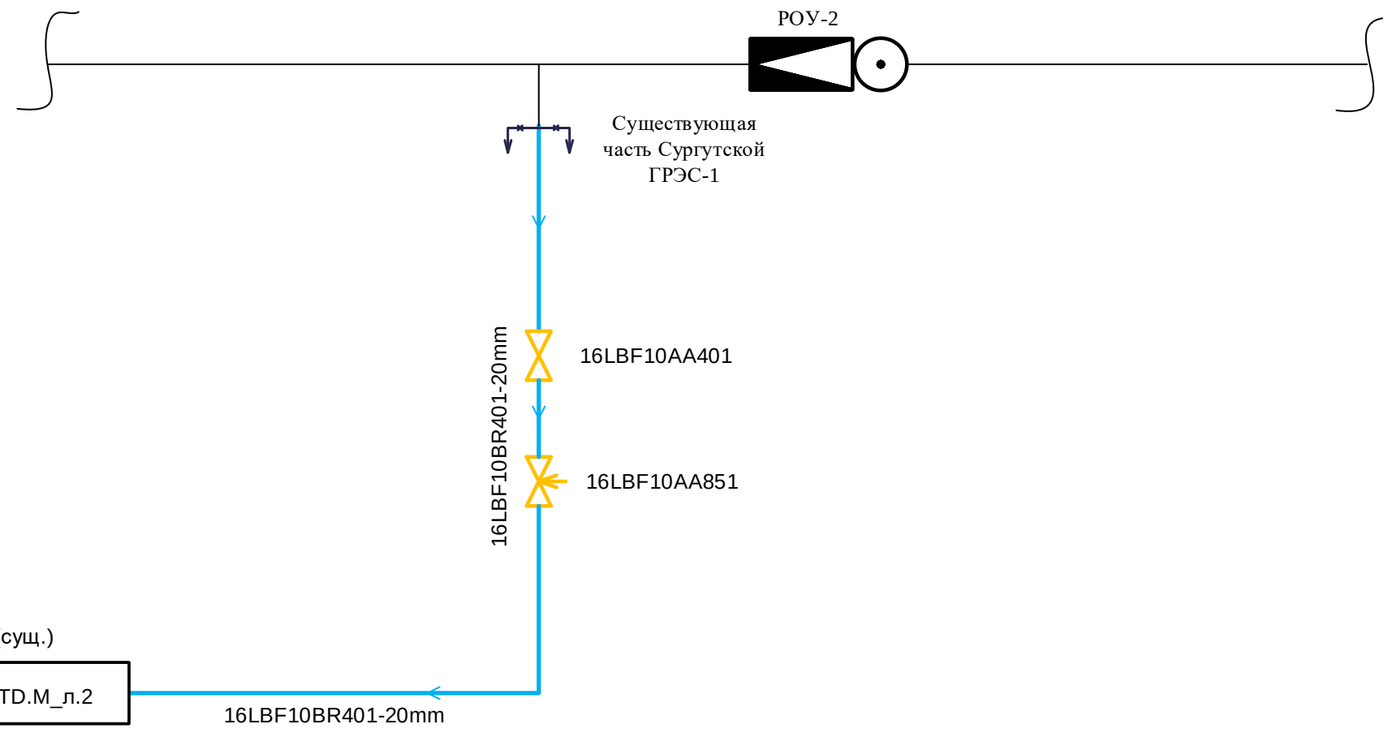

Существующая часть Сургутской ГРЭС-1 — АО «Институт Теплоэлектропроект» (ТЭП) - граница проектирования

Согласовано

Взам. инв. №

Подпись и дата

Инв. № подл.

Изм.	Кол.уч	Лист	№ док.	Подп.	Дата
Разработал		Гусев.Т			
Проверил		Демина			
Н. контр.		Черемушкина			

246N1 – 16UHJ – 7741 – TD.M

Модернизация генерирующего объекта Сургутская ГРЭС-1 (16Г)

Главный корпус. PI-диаграмма трубопровода дренажа с РОУ-2 на врезку в дренаж ГПЗ.

Стадия	Лист	Листов
Р	2	

Система LBF.

АКЦИОНЕРНОЕ ОБЩЕСТВО ИНСТИТУТ ТЕПЛОЭЛЕКТРОПРОЕКТ Г. МОСКВА

Формат А3