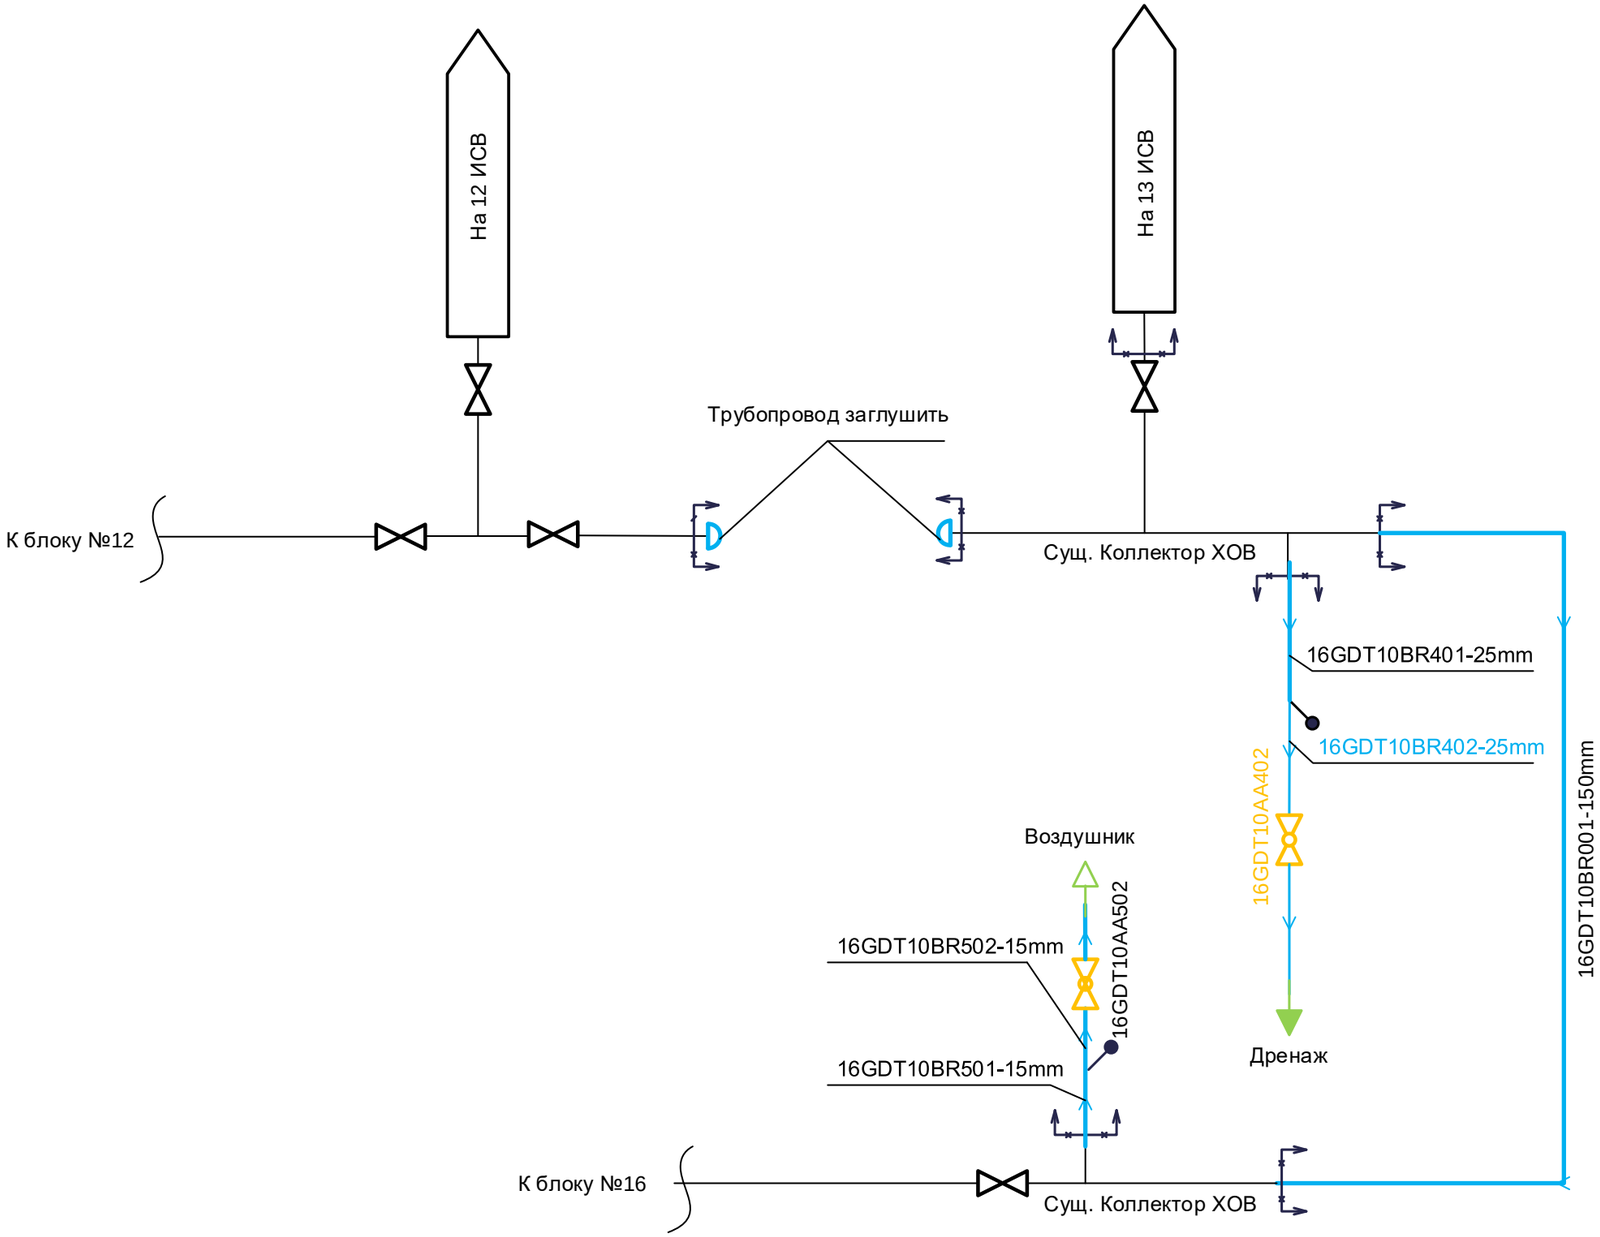

Примечание: Восстановление существующего трубопровода ХОВ от блока 15 к блоку 16.

Существующая часть Сургутской ГРЭС-1

АО «Институт Теплоэлектропроект» (ТЭП)

- граница проектирования

Изм.	Кол.уч	Лист	№ док.	Подп.	Дата
Разработал		Гусев			
Проверил		Демина			
Н. контр.		Черемушкина			

246N1-16UHJ-7748-TD.M

Модернизация генерирующего объекта Сургутская ГРЭС-1(16г).

Главный корпус. PI-Диаграмма трубопровода-перемычки ХОВ у блока 15 (перенос от блока 16)

Стадия	Лист	Листов
Р	2	

PI-Диаграмма трубопровода-перемычки ХОВ у блока 15 (перенос от блока 16)
Система: GDT

АКЦИОНЕРНОЕ ОБЩЕСТВО ИНСТИТУТ ТЕПЛОЭЛЕКТРОПРОЕКТ Г. МОСКВА

Согласовано

Взам. инв. №

Подпись и дата

Инв. № подл.

Формат А3