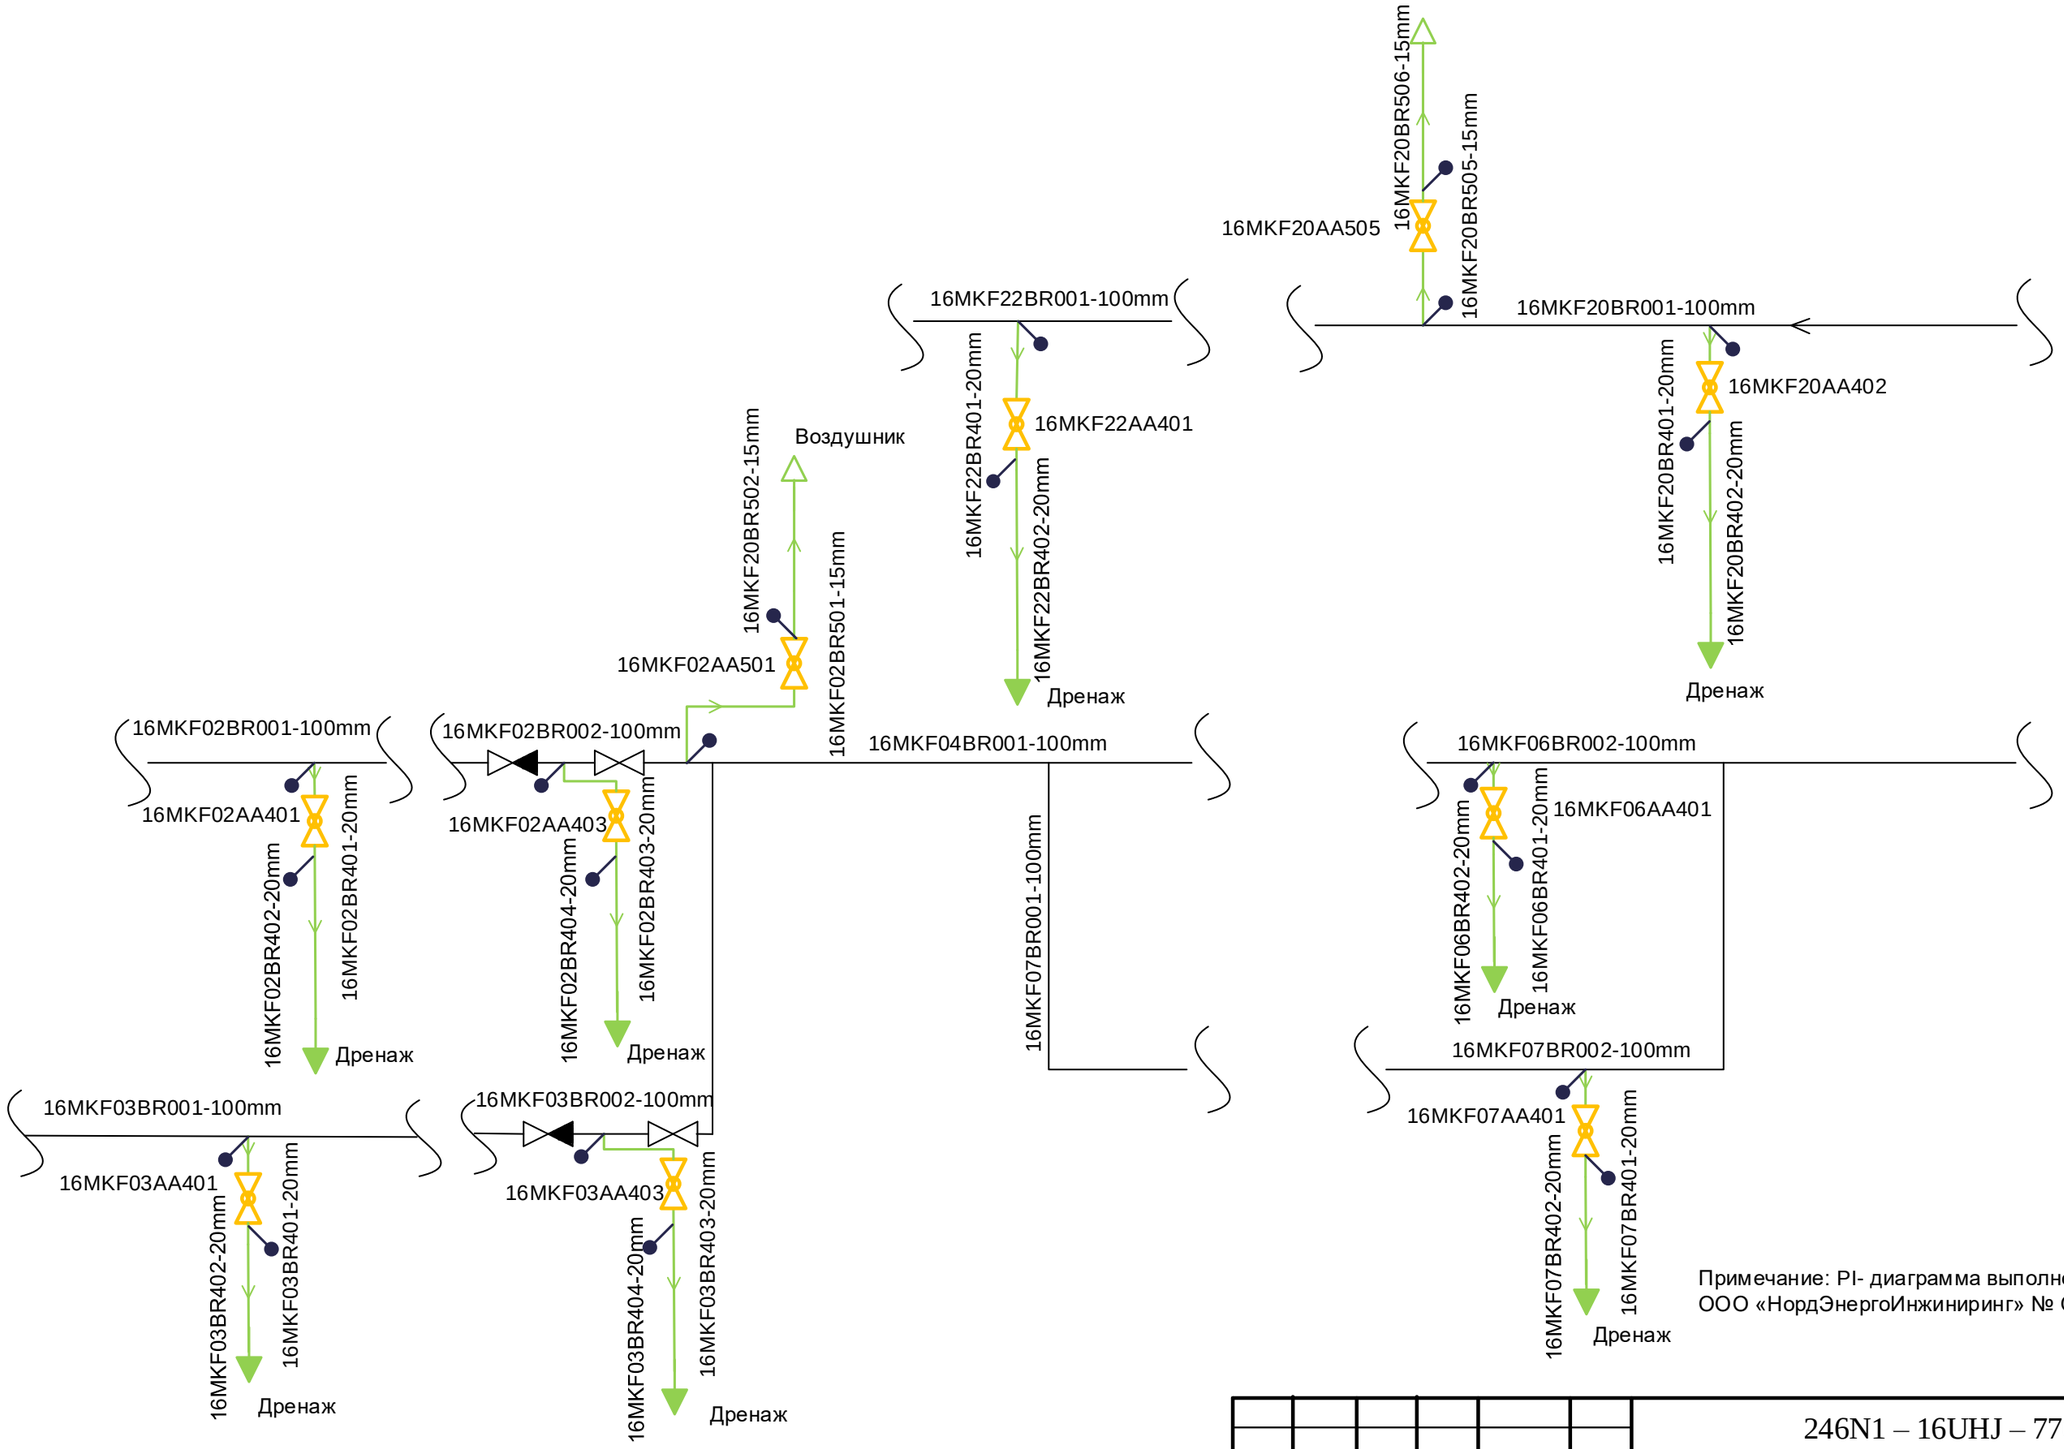

Примечание: PI- диаграмма выполнена на основании схемы ООО «НордЭнергоИнжиниринг» № ОБС.349.081 ГЗ

Изм.	Кол.уч	Лист	№ док.	Подп.	Дата
Разработал		Гусев			
Проверил		Демина			
Н. контр.		Черемушкина			

246N1 – 16UHJ – 7762 – TD.M

Модернизация генерирующего объекта Сургутская ГРЭС-1 (16Г)

Главный корпус.PI -диаграмма дренажей, воздушников и вспомогательных трубопроводов системы охлаждения турбогенератора.

Стадия	Лист	Листов
Р	2	

PI -диаграмма дренажей, воздушников и вспомогательных трубопроводов системы охлаждения турбогенератора. Система MKF.

АКЦИОНЕРНОЕ ОБЩЕСТВО ИНСТИТУТ ТЕПЛОЭЛЕКТРОПРОЕКТ Г. МОСКВА

Взам. инв. №

Подпись и дата

Инв. № подл.

Формат А3