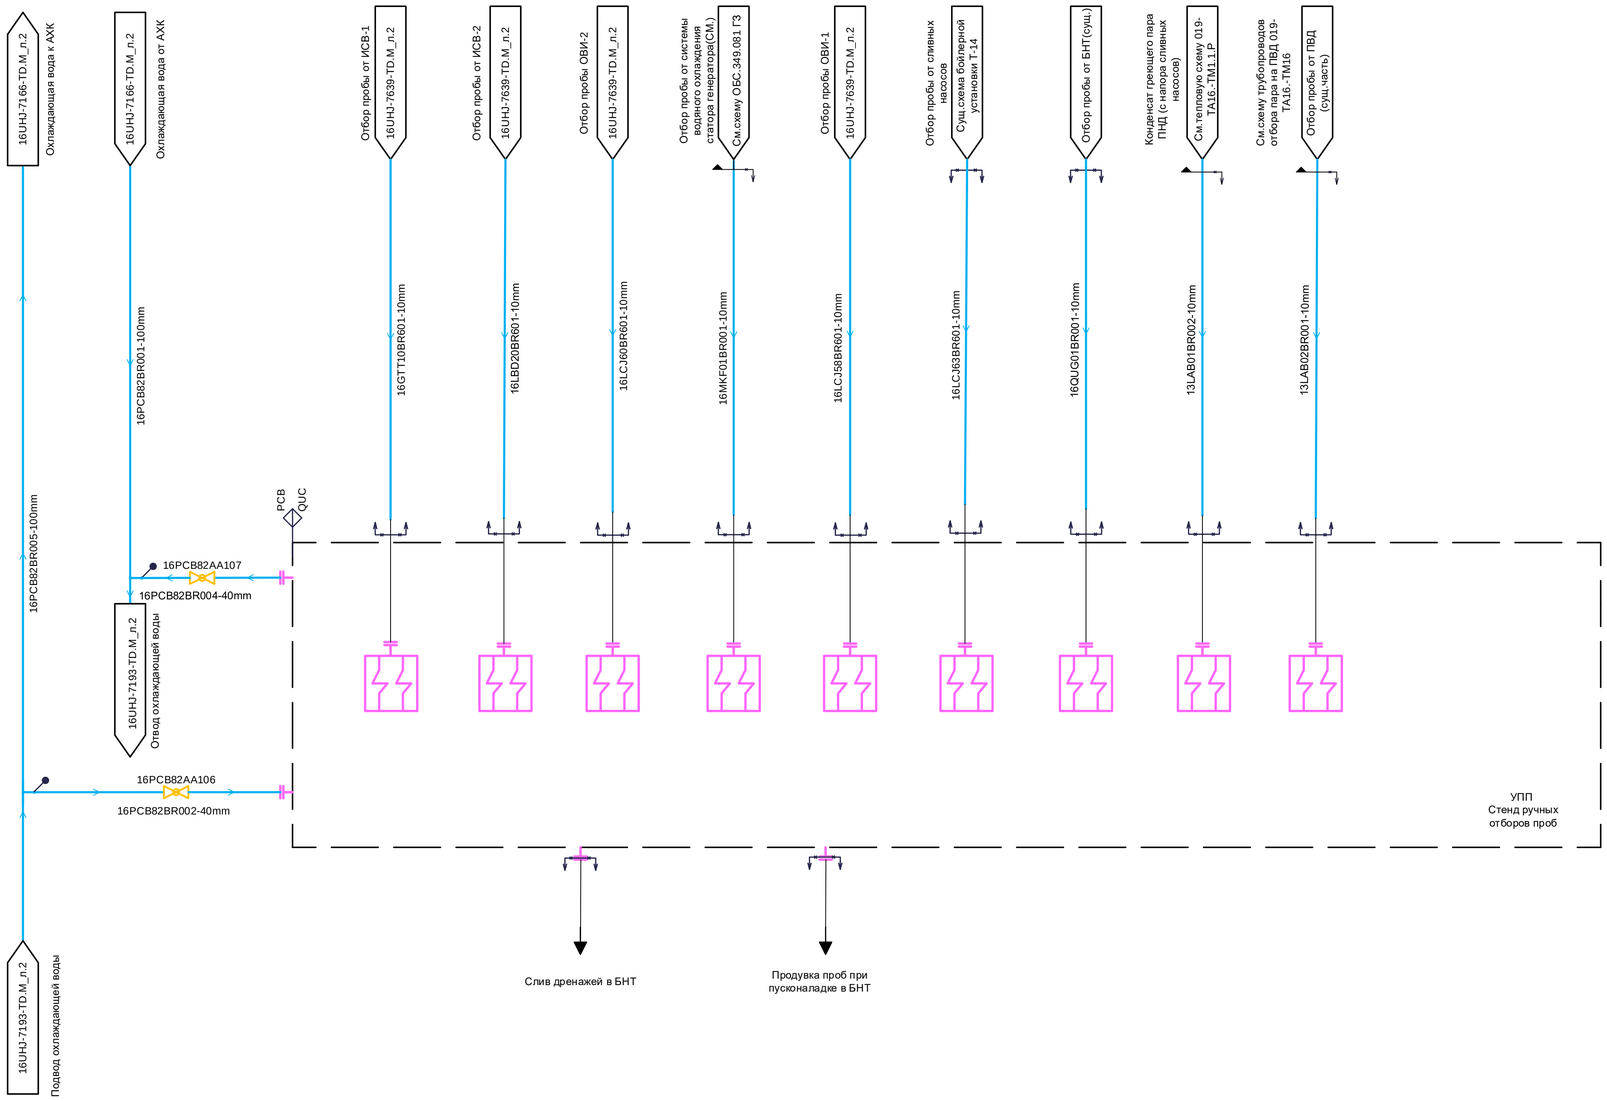

Существующая часть Сургутской ГРЭС-1

АО «Институт Теплоэлектропроект» (ТЭП)
- граница проектирования

АО «Силовые Машины» (СМ)
- граница проектирования

АО «Институт Теплоэлектропроект» (ТЭП)

Примечание:
Схему рассматривать совместно со схемой АХК 246N1-16UHJ-7166-TD.M
PI-Диаграмма трубопроводов отбора проб основного конденсата.

Согласовано

Взам. инв. №

Подпись и дата

Инв. № подл.

Изм.	Кол.уч.	Лист	№ док.	Подп.	Дата	246N1-16UHJ-7764-TD.M		
						Модернизация генерирующего обьекта Сургутская ГРЭС-1		
Разработал		Гусев				Главный корпус.PI-Диаграмма трубопроводов отбора проб пара и воды.	Стадия	Лист	Листов
Проверил		Демина					Р	2	
Гл.спец		Гавриленко							
Н. контр.		Черемушкина				PI-Диаграмма трубопроводов отбора проб пара и воды.	АКЦИОНЕРНОЕ ОБЩЕСТВО «ИНСТИТУТ ТЕПЛОЭЛЕКТРОПРОЕКТ» Г. МОСКВА	

Формат А1