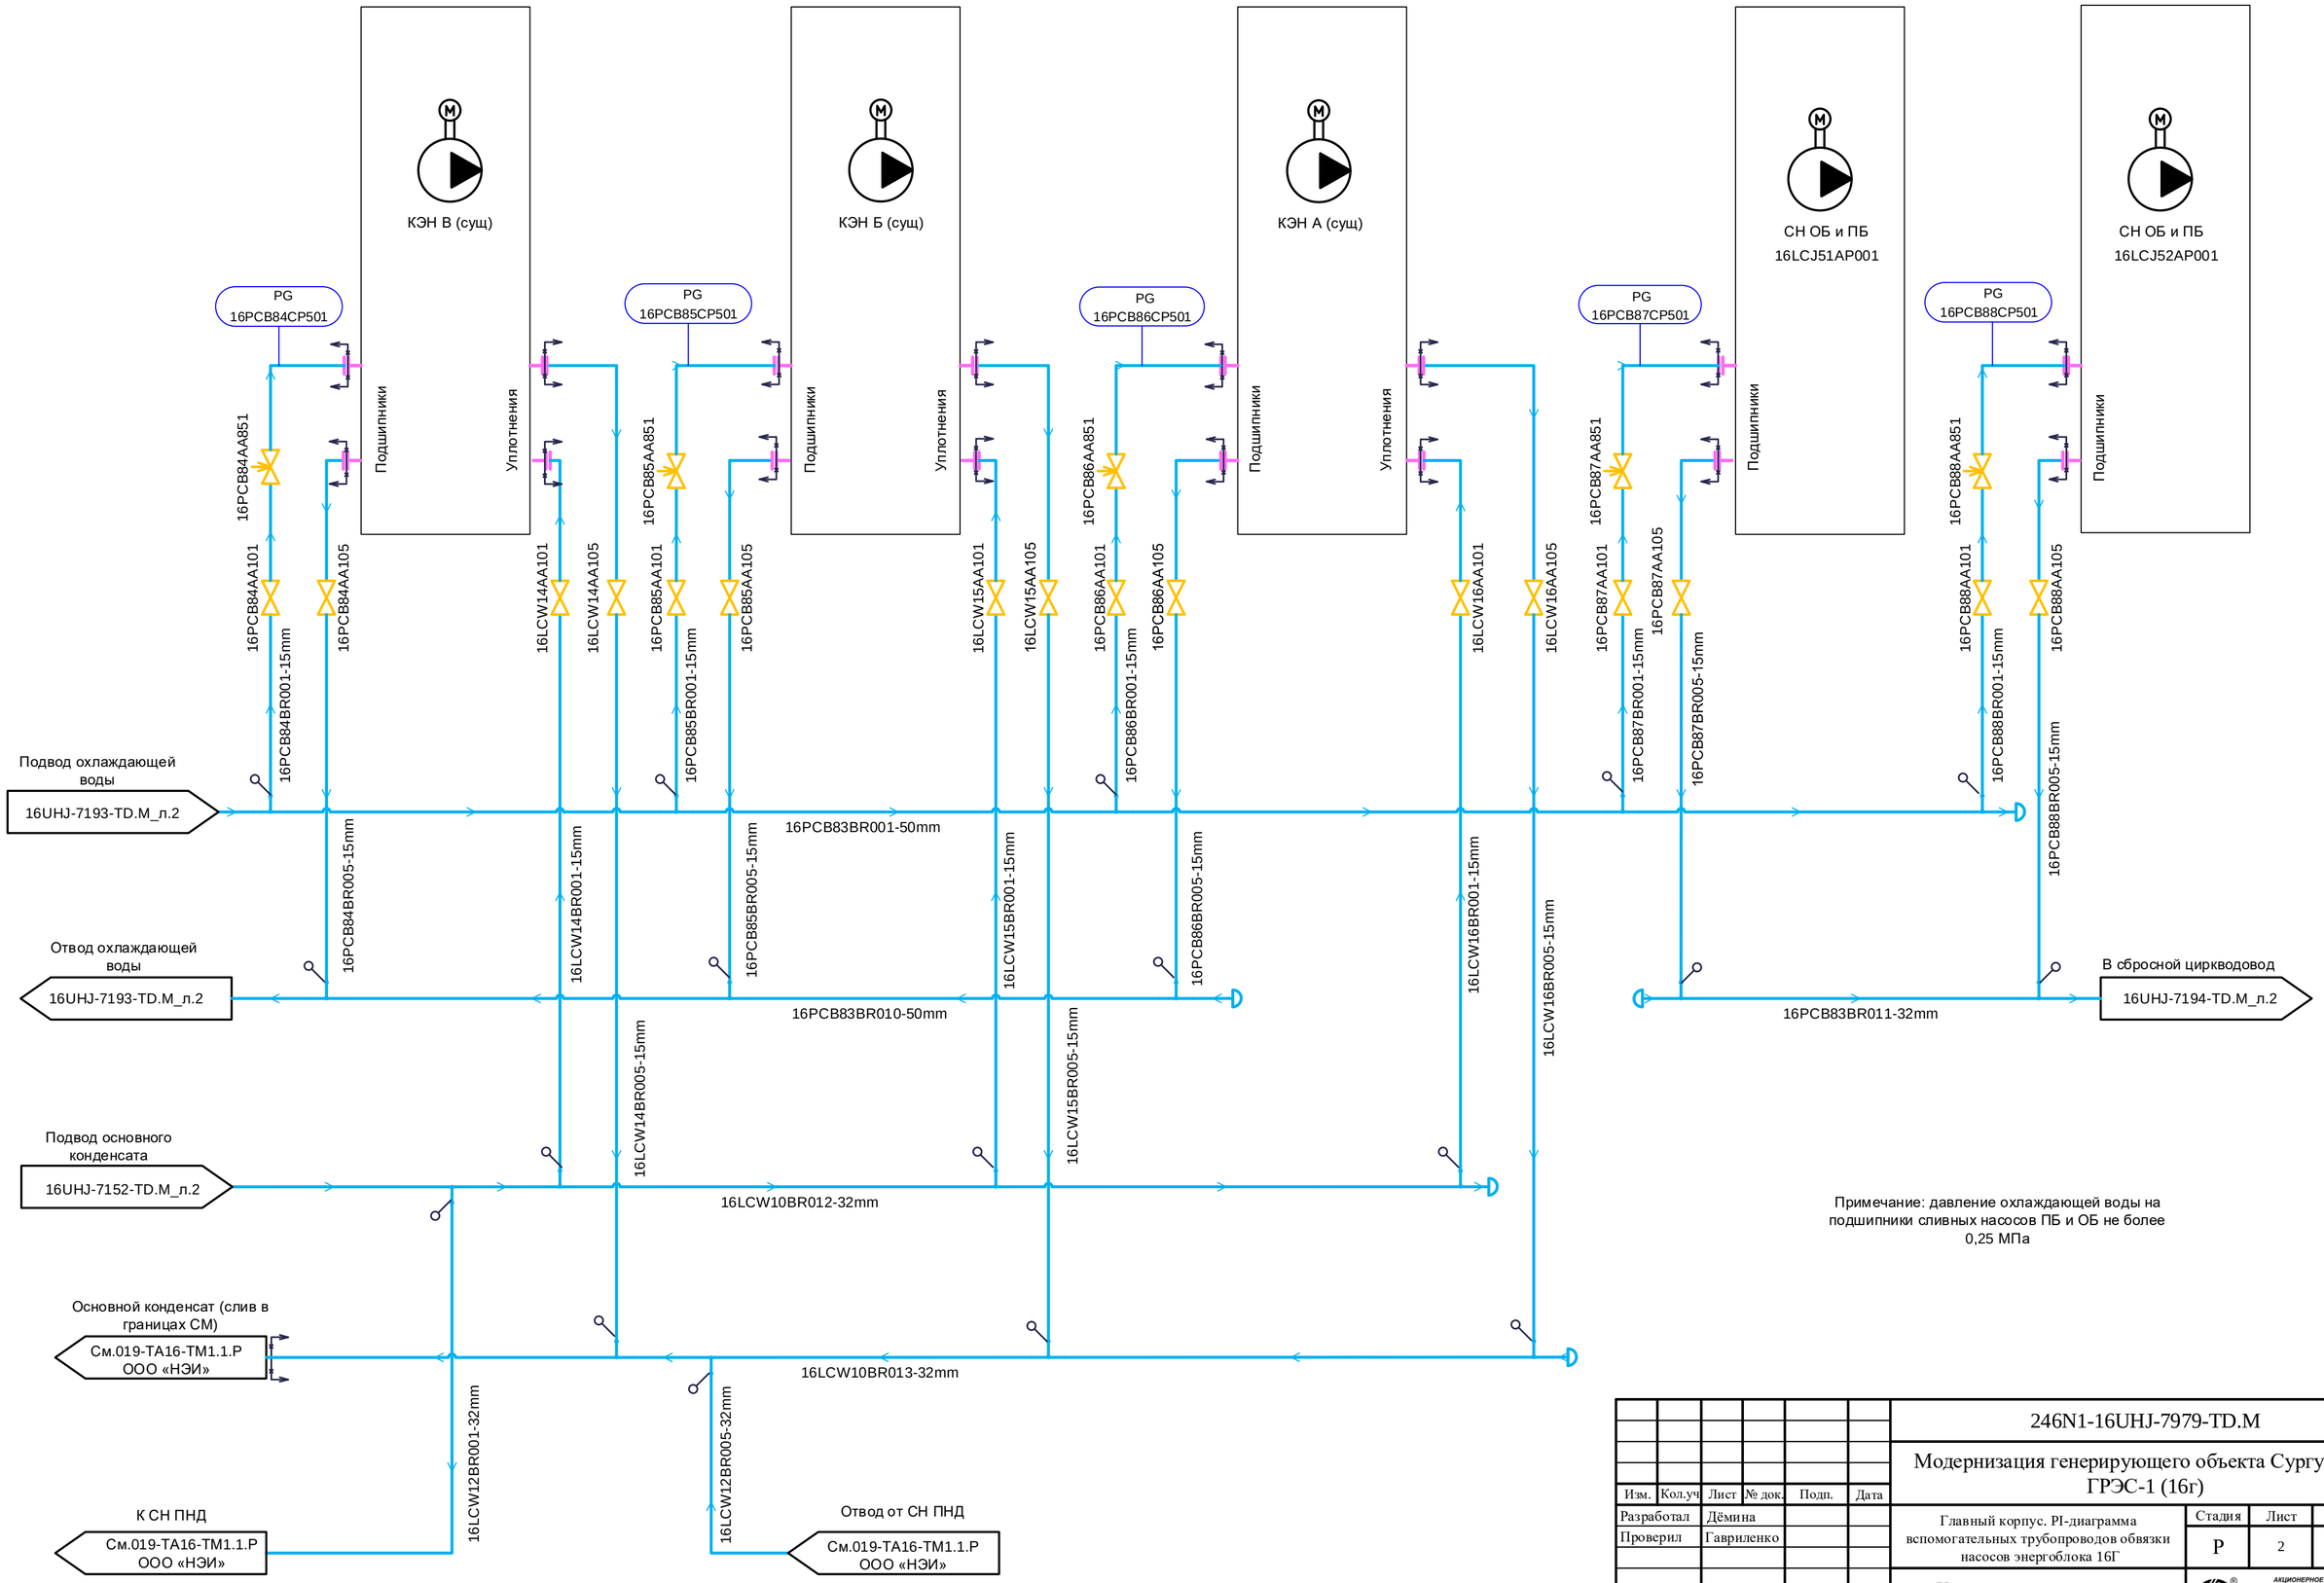

Примечание: давление охлаждающей воды на подшипники сливных насосов ПБ и ОБ не более 0,25 МПа

Изм.	Кол.уч	Лист	№ док.	Подп.	Дата	246N1-16UHJ-7979-TD.M		
						Модернизация генерирующего объекта Сургутская ГРЭС-1 (16г)		
Разработал		Дёмина				Главный корпус. PI-диаграмма вспомогательных трубопроводов обвязки насосов энергоблока 16Г	Стадия	Лист	Листов
Проверил		Гавриленко					Р	2	
Н. контр.		Астраханцев				PI-диаграмма вспомогательных трубопроводов обвязки насосов энергоблока 16Г. Системы LCW, PCB	АКЦИОНЕРНОЕ ОБЩЕСТВО ИНСТИТУТ ТЕПЛОЭЛЕКТРОПРОЕКТ Г. МОСКВА	

Согласовано

ОАСУ Соболева

Взам. инв. №

Подпись и дата

Инв. № подл.

Формат А2