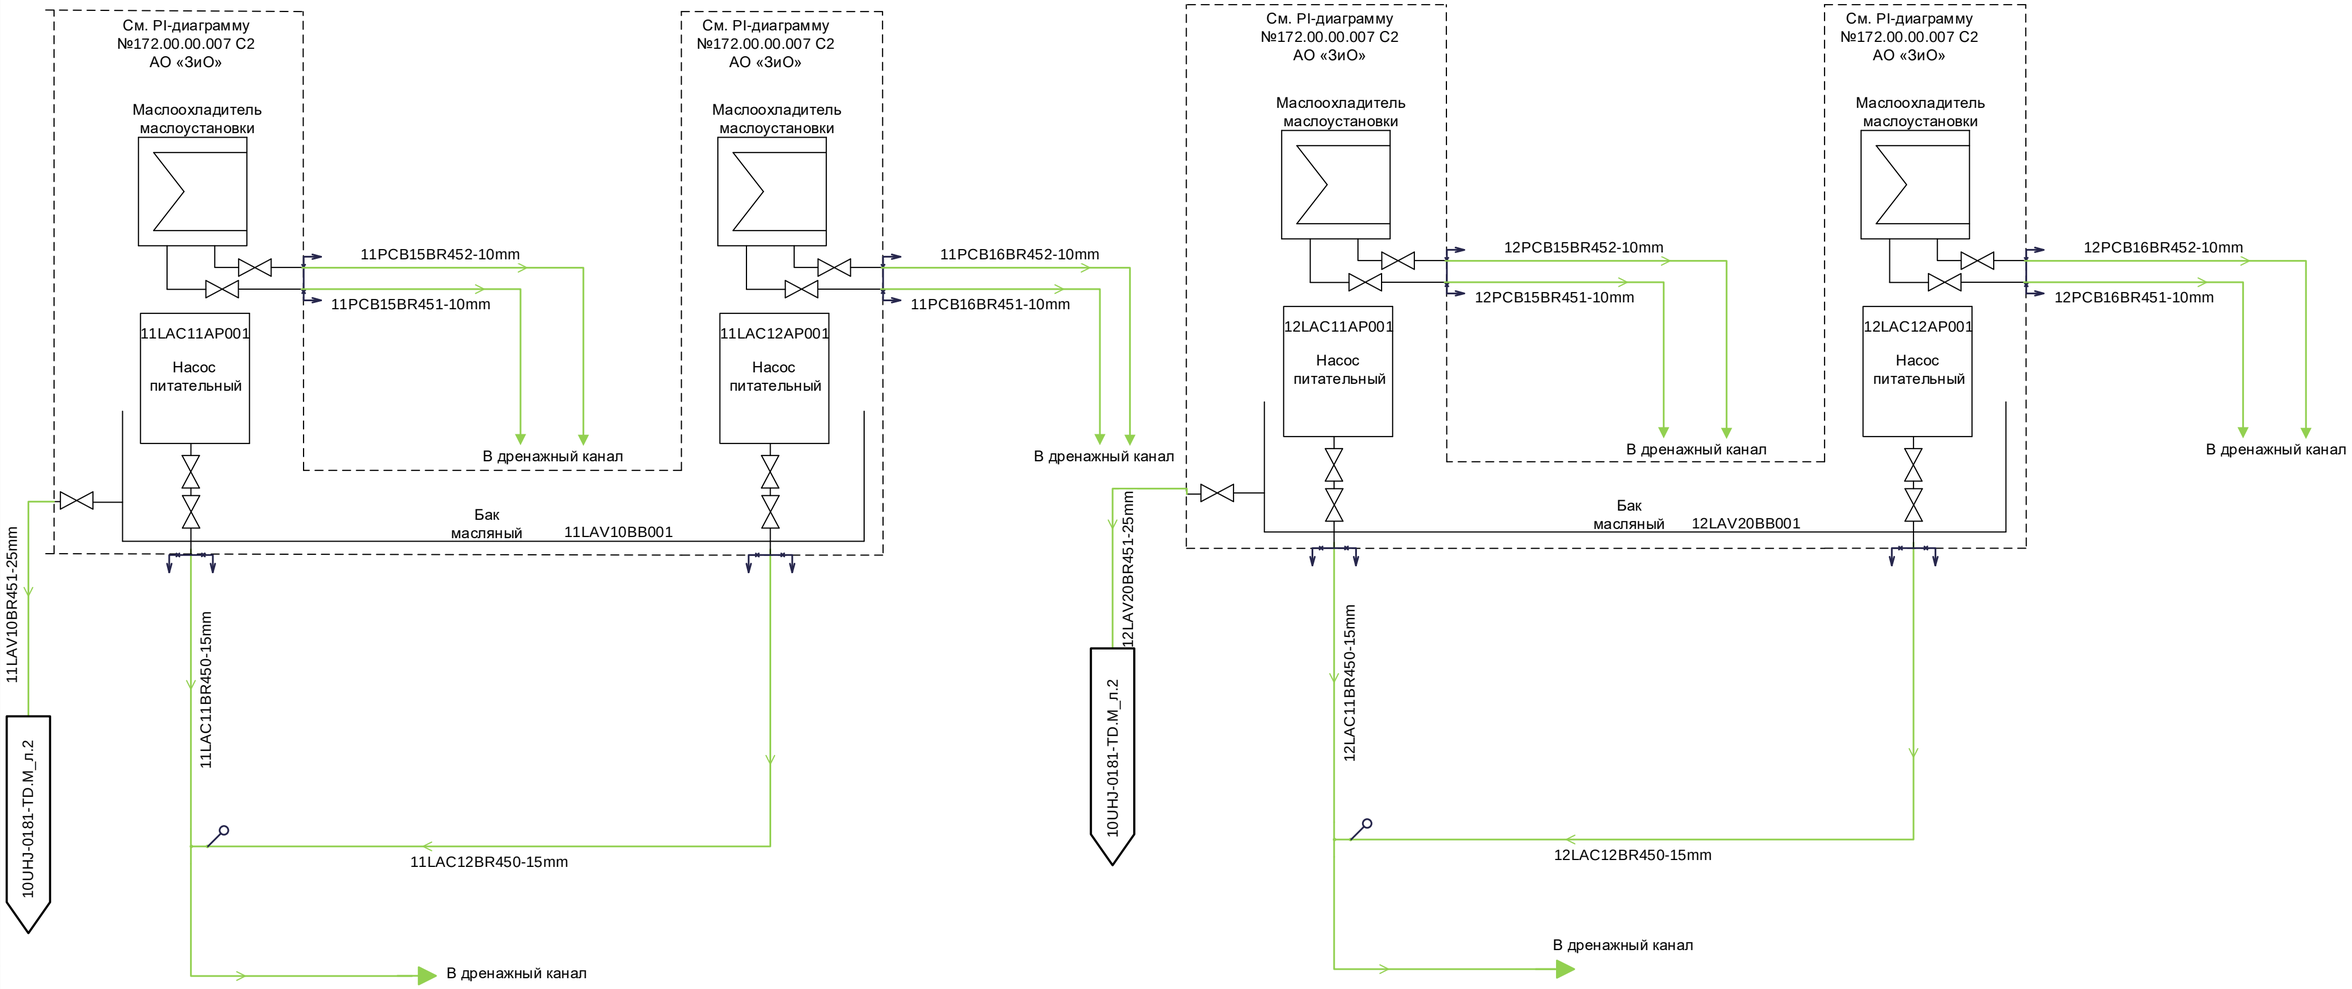

Примечание:
Диаметр опорожнения насоса изменен в соответствии со схемой ЛН17.180.00-002 МЧ
АО «ГМС Ливгидромаш»

1	-	Зам.	5061-25		12.25	
Изм.	Кол.уч	Лист	№ док.	Подп.	Дата	
Разработал		Евстифеев				
Проверил		Лаврякова				
Гл. спец.		Сергеева				
Н. контр.		Черемушкина				

261N1 – 10UHJ – 0157 – TD.M

Южно-Якутская ТЭС. Рабочая документация

Главный корпус. PI-диаграмма вспомогательных трубопроводов низкого давления.

Стадия	Лист	Листов
Р	2	

PI-диаграмма вспомогательных трубопроводов низкого давления. Система LAC, PCB.

АКЦИОНЕРНОЕ ОБЩЕСТВО ИНСТИТУТ ТЕПЛОЭЛЕКТРОПРОЕКТ Г. МОСКВА

Согласовано

ОАСУ

Взам. инв. №

Подпись и дата

Инв. № подл.

Формат А2