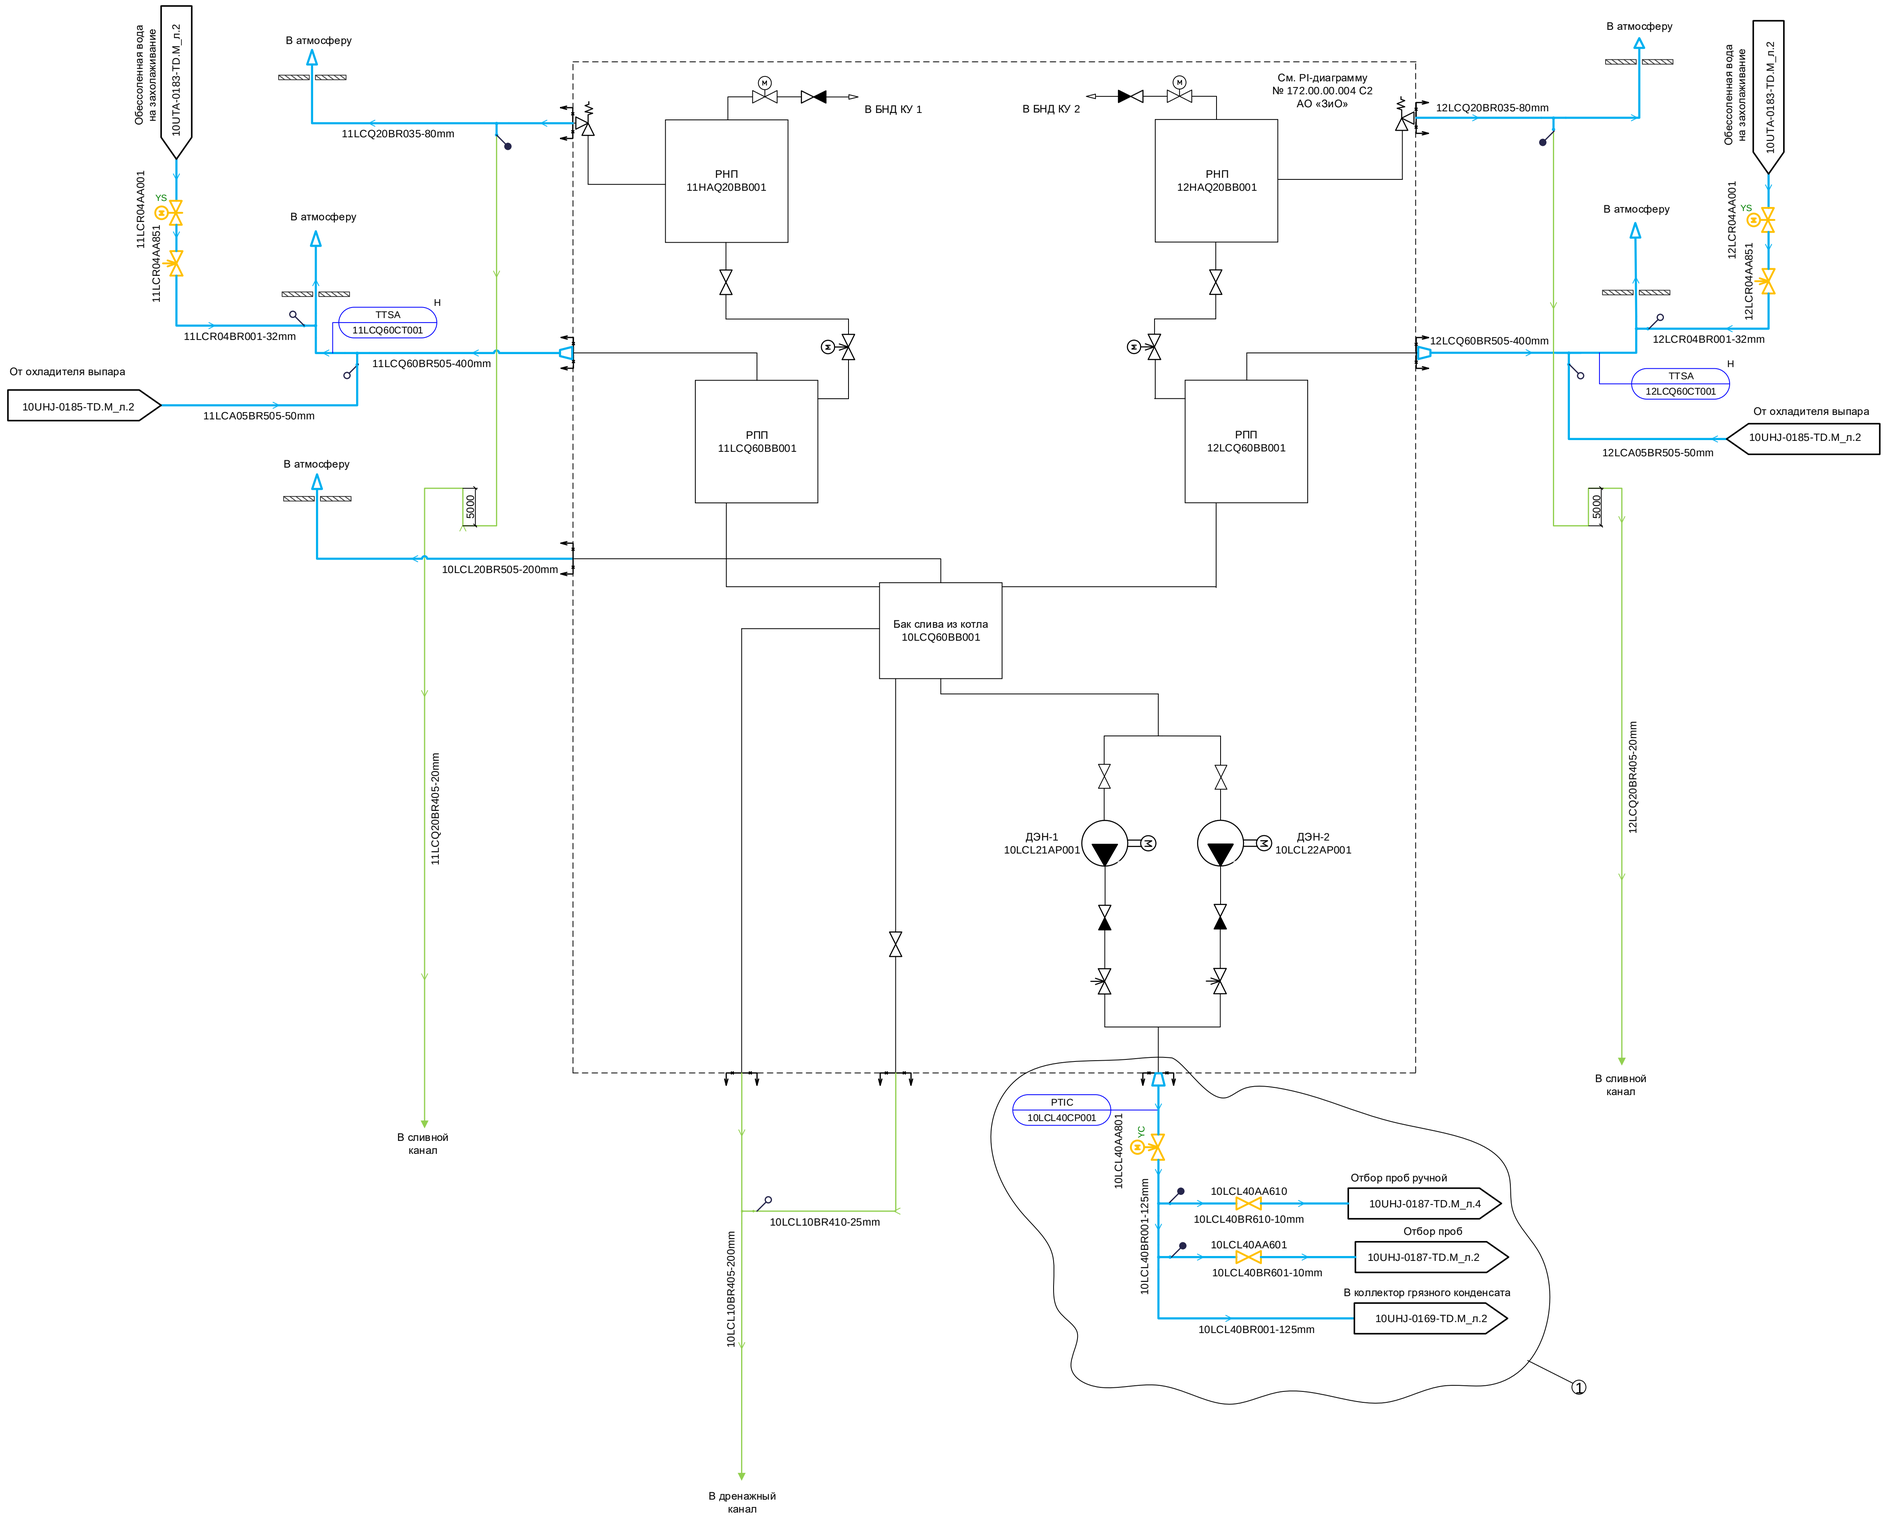

Согласовано

ОАСУ

Взам. инв. №

Подпись и дата

Инв. № подл.

3	1	Зам.	154-26		01.26	261N1-10UHJ-0161-TD.M
Изм.	Кол.уч	Лист	№ док.	Подп.	Дата	Южно-Якутская ТЭС. Рабочая документация
Разработал		Евстифеев				P&I-диаграмма дренажей, воздушников и вспомогательных трубопроводов котла.
Проверил		Лаврякова				Стадия: Р; Лист: 2; Листов:
Глав.спец.		Сергеева				
Н. контр.		Черемушкина				P&I-диаграмма дренажей, воздушников и вспомогательных трубопроводов котла. Система LCL, LBA.

АКЦИОНЕРНОЕ ОБЩЕСТВО ИНСТИТУТ ТЕПЛОЭЛЕКТРОПРОЕКТ г. МОСКВА

Формат А1