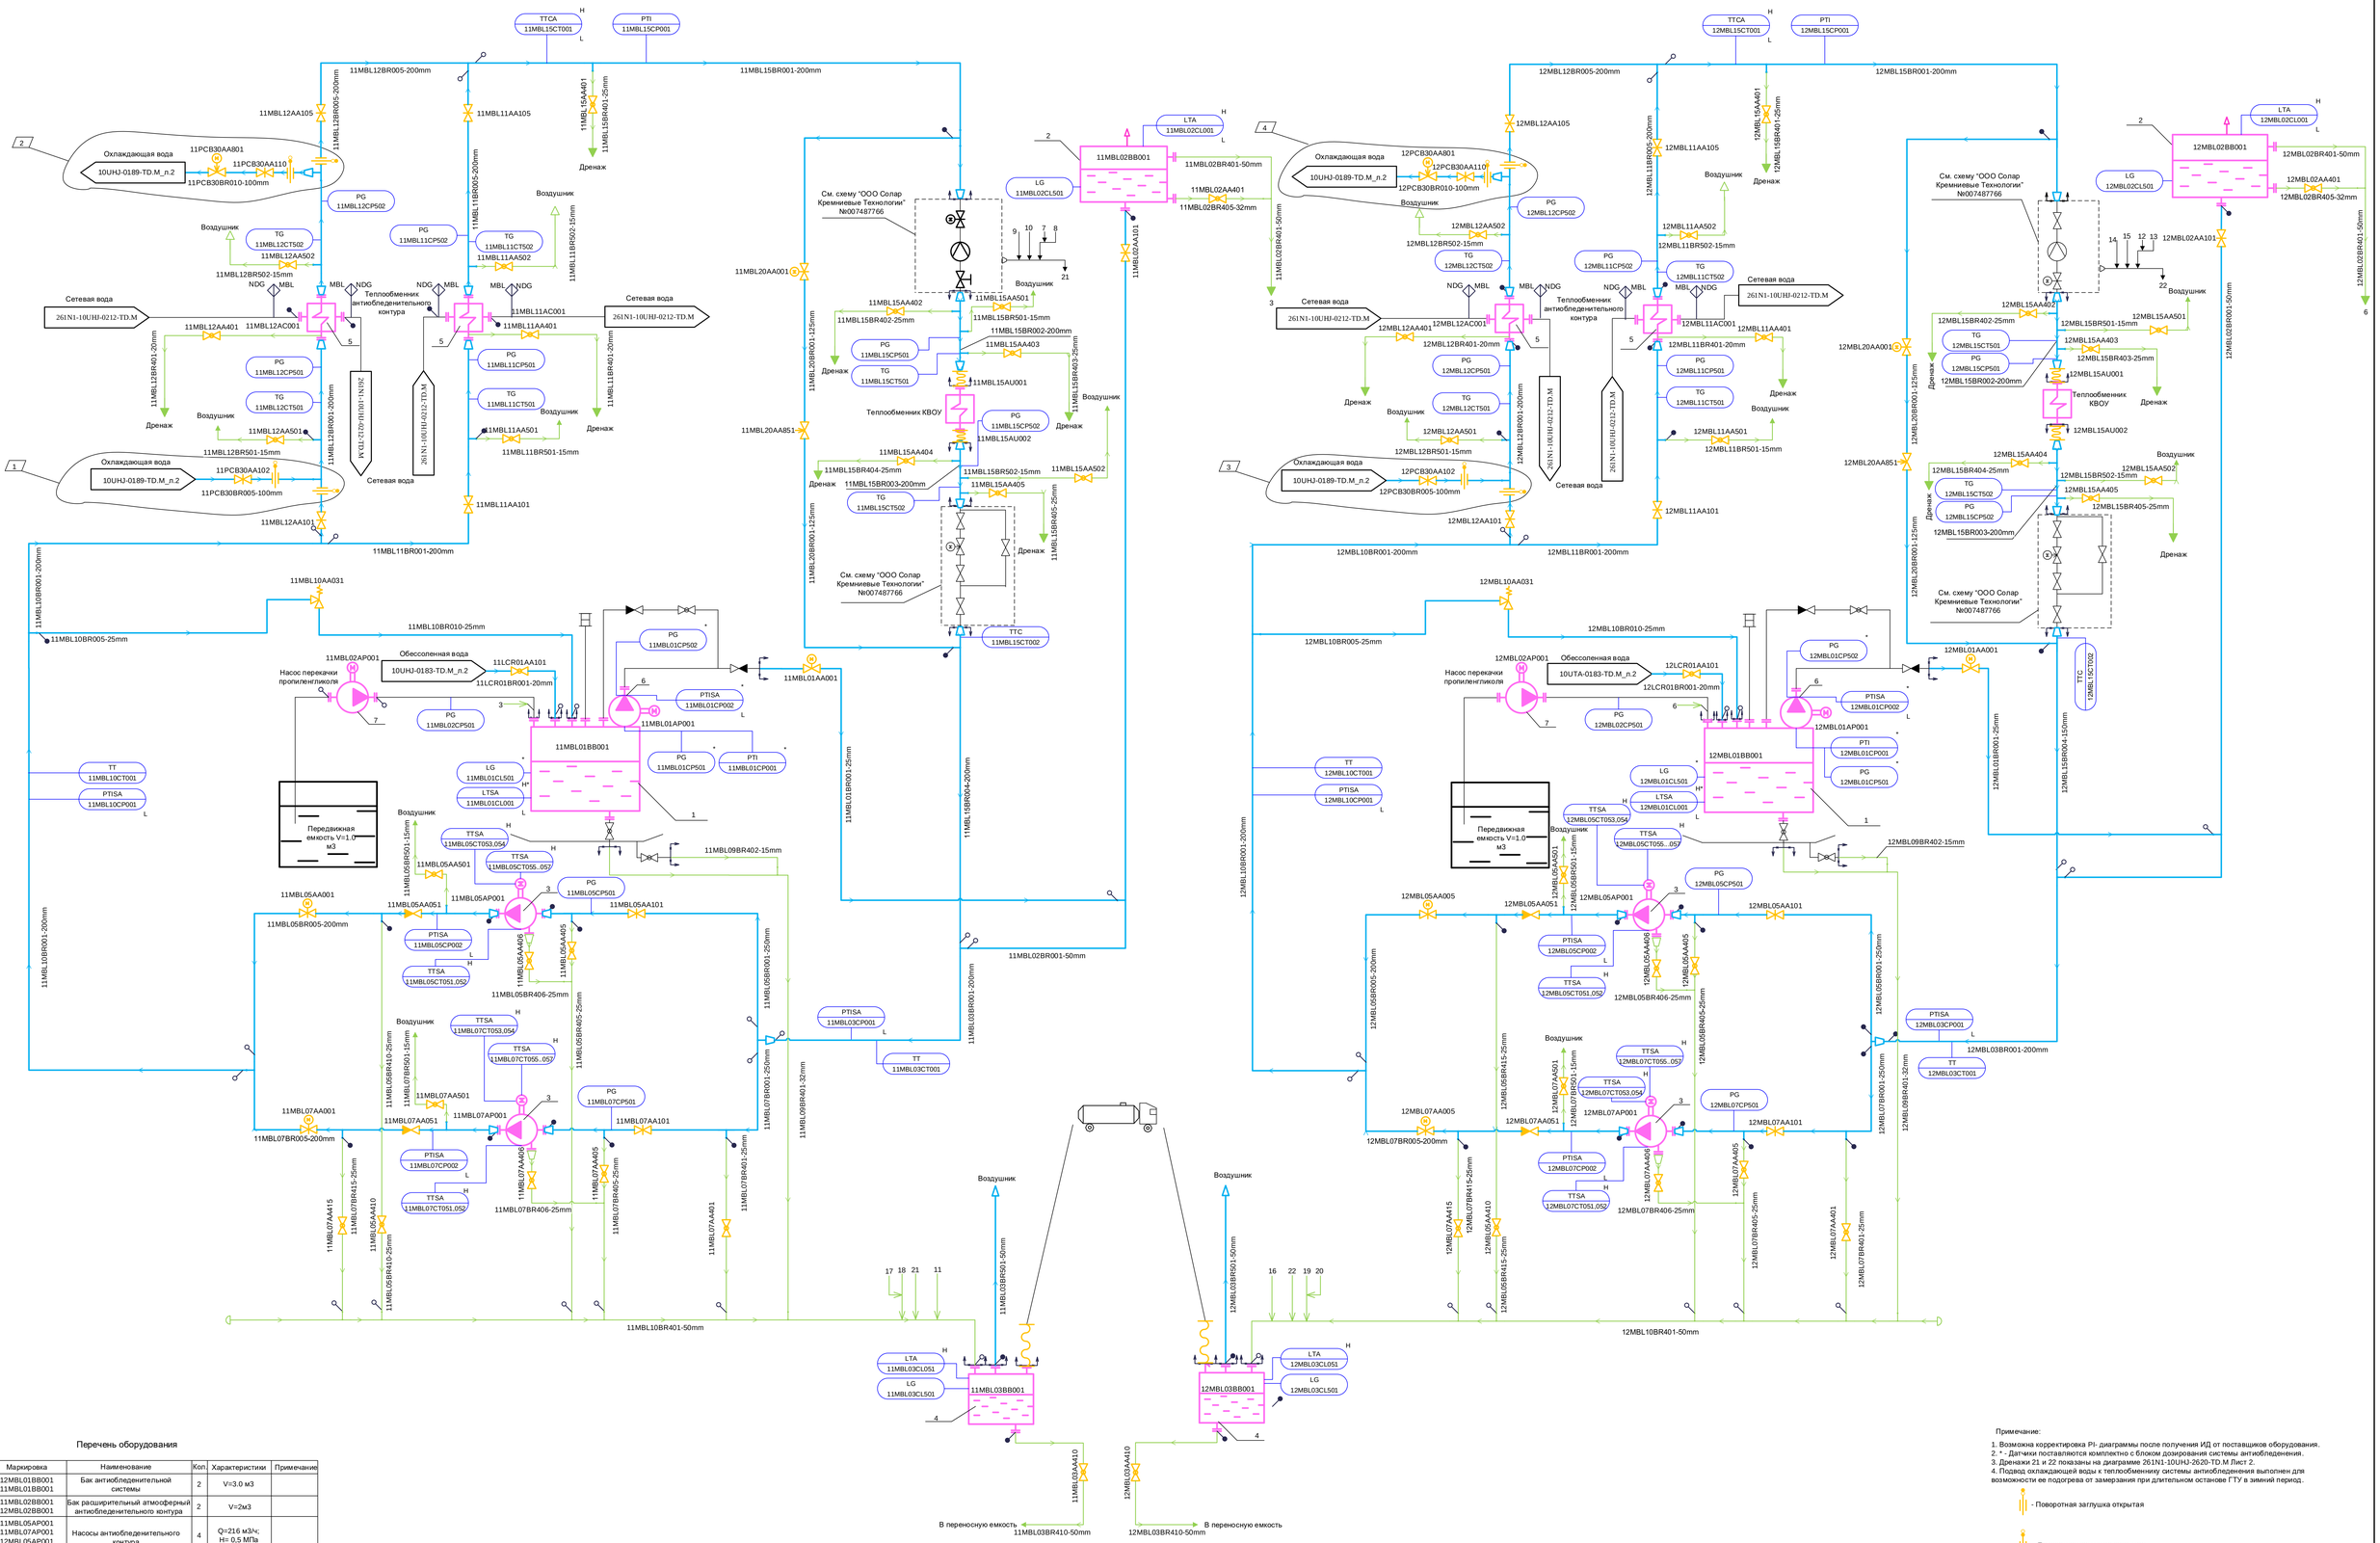

Перечень оборудования

Поз.	Маркировка	Наименование	Кол.	Характеристики	Примечание
1	12MBL01BB001 11MBL01BB001	Бак антибледенительной системы	2	V=3.0 м3	
2	11MBL02BB001 12MBL02BB001	Бак расширительный атмосферный антибледенительного контура	2	V=2м3	
3	11MBL05AP001 11MBL07AP001 12MBL05AP001 12MBL07AP001	Насосы антибледенительного контура	4	Q=216 м3/ч; H= 0,5 МПа	
4	11MBL03BB001 12MBL03BB001	Бак опорожнения контура антибледенения	2	V=8.0 м3	
5	11MBL12AC001 11MBL11AC001 12MBL12AC001 12MBL11AC001	Теплообменник антибледенительного контура	4	Q=11,2 Гкал/ч	
6	12MBL01AP001 11MBL01AP001	Насос антибледенительной системы диафрагменный	2	Q=0,94 м3/Ч H=0,96 МПа	
7	12MBL02AP001 11MBL02AP001	Насосы перекачки пропиленгликоля	2	-	

Примечание:

1. Возможна корректировка PI- диаграммы после получения ИД от поставщиков оборудования.
2. * - Датчики поставляются комплектно с блоком дозирования системы антибледенения.
3. Дренажи 21 и 22 показаны на диаграмме 261N1-10UHJ-2620-TD.M Лист 2.
4. Подвод охлаждающей воды к теплообменнику системы антибледенения выполнен для возможности ее подогрева от замерзания при длительном останове ГТУ в зимний период.

- Поворотная заглушка открытая

- Поворотная заглушка закрытая

						261N1-10UHJ-0165-TD.M	
3	4	Зам.	15-6-26		01.26	Южно-Якутская ТЭС. Рабочая документация.	
Инв.	Кол.уч	Лист	№ док.	Подп.	Дата		
Разработал		Евстифеев				Главный корпус. P&I-диаграмма трубопроводов антибледенительной системы	Стадия: Р; Лист: 2; Листов:
Проверил		Лаврякова					
Глав.спец		Сергеева					
Н. контр.		Черемушкина				P&I-диаграмма трубопроводов антибледенительной системы. Система MBL.	АКЦИОНЕРНОЕ ОБЩЕСТВО ТЕЛЕЭНЕРГОПРОЕКТ г. МОСКВА

Согласовано

ОАСУ

Взам. инв. №

Подпись и дата

Инв. № подл.

Формат А1