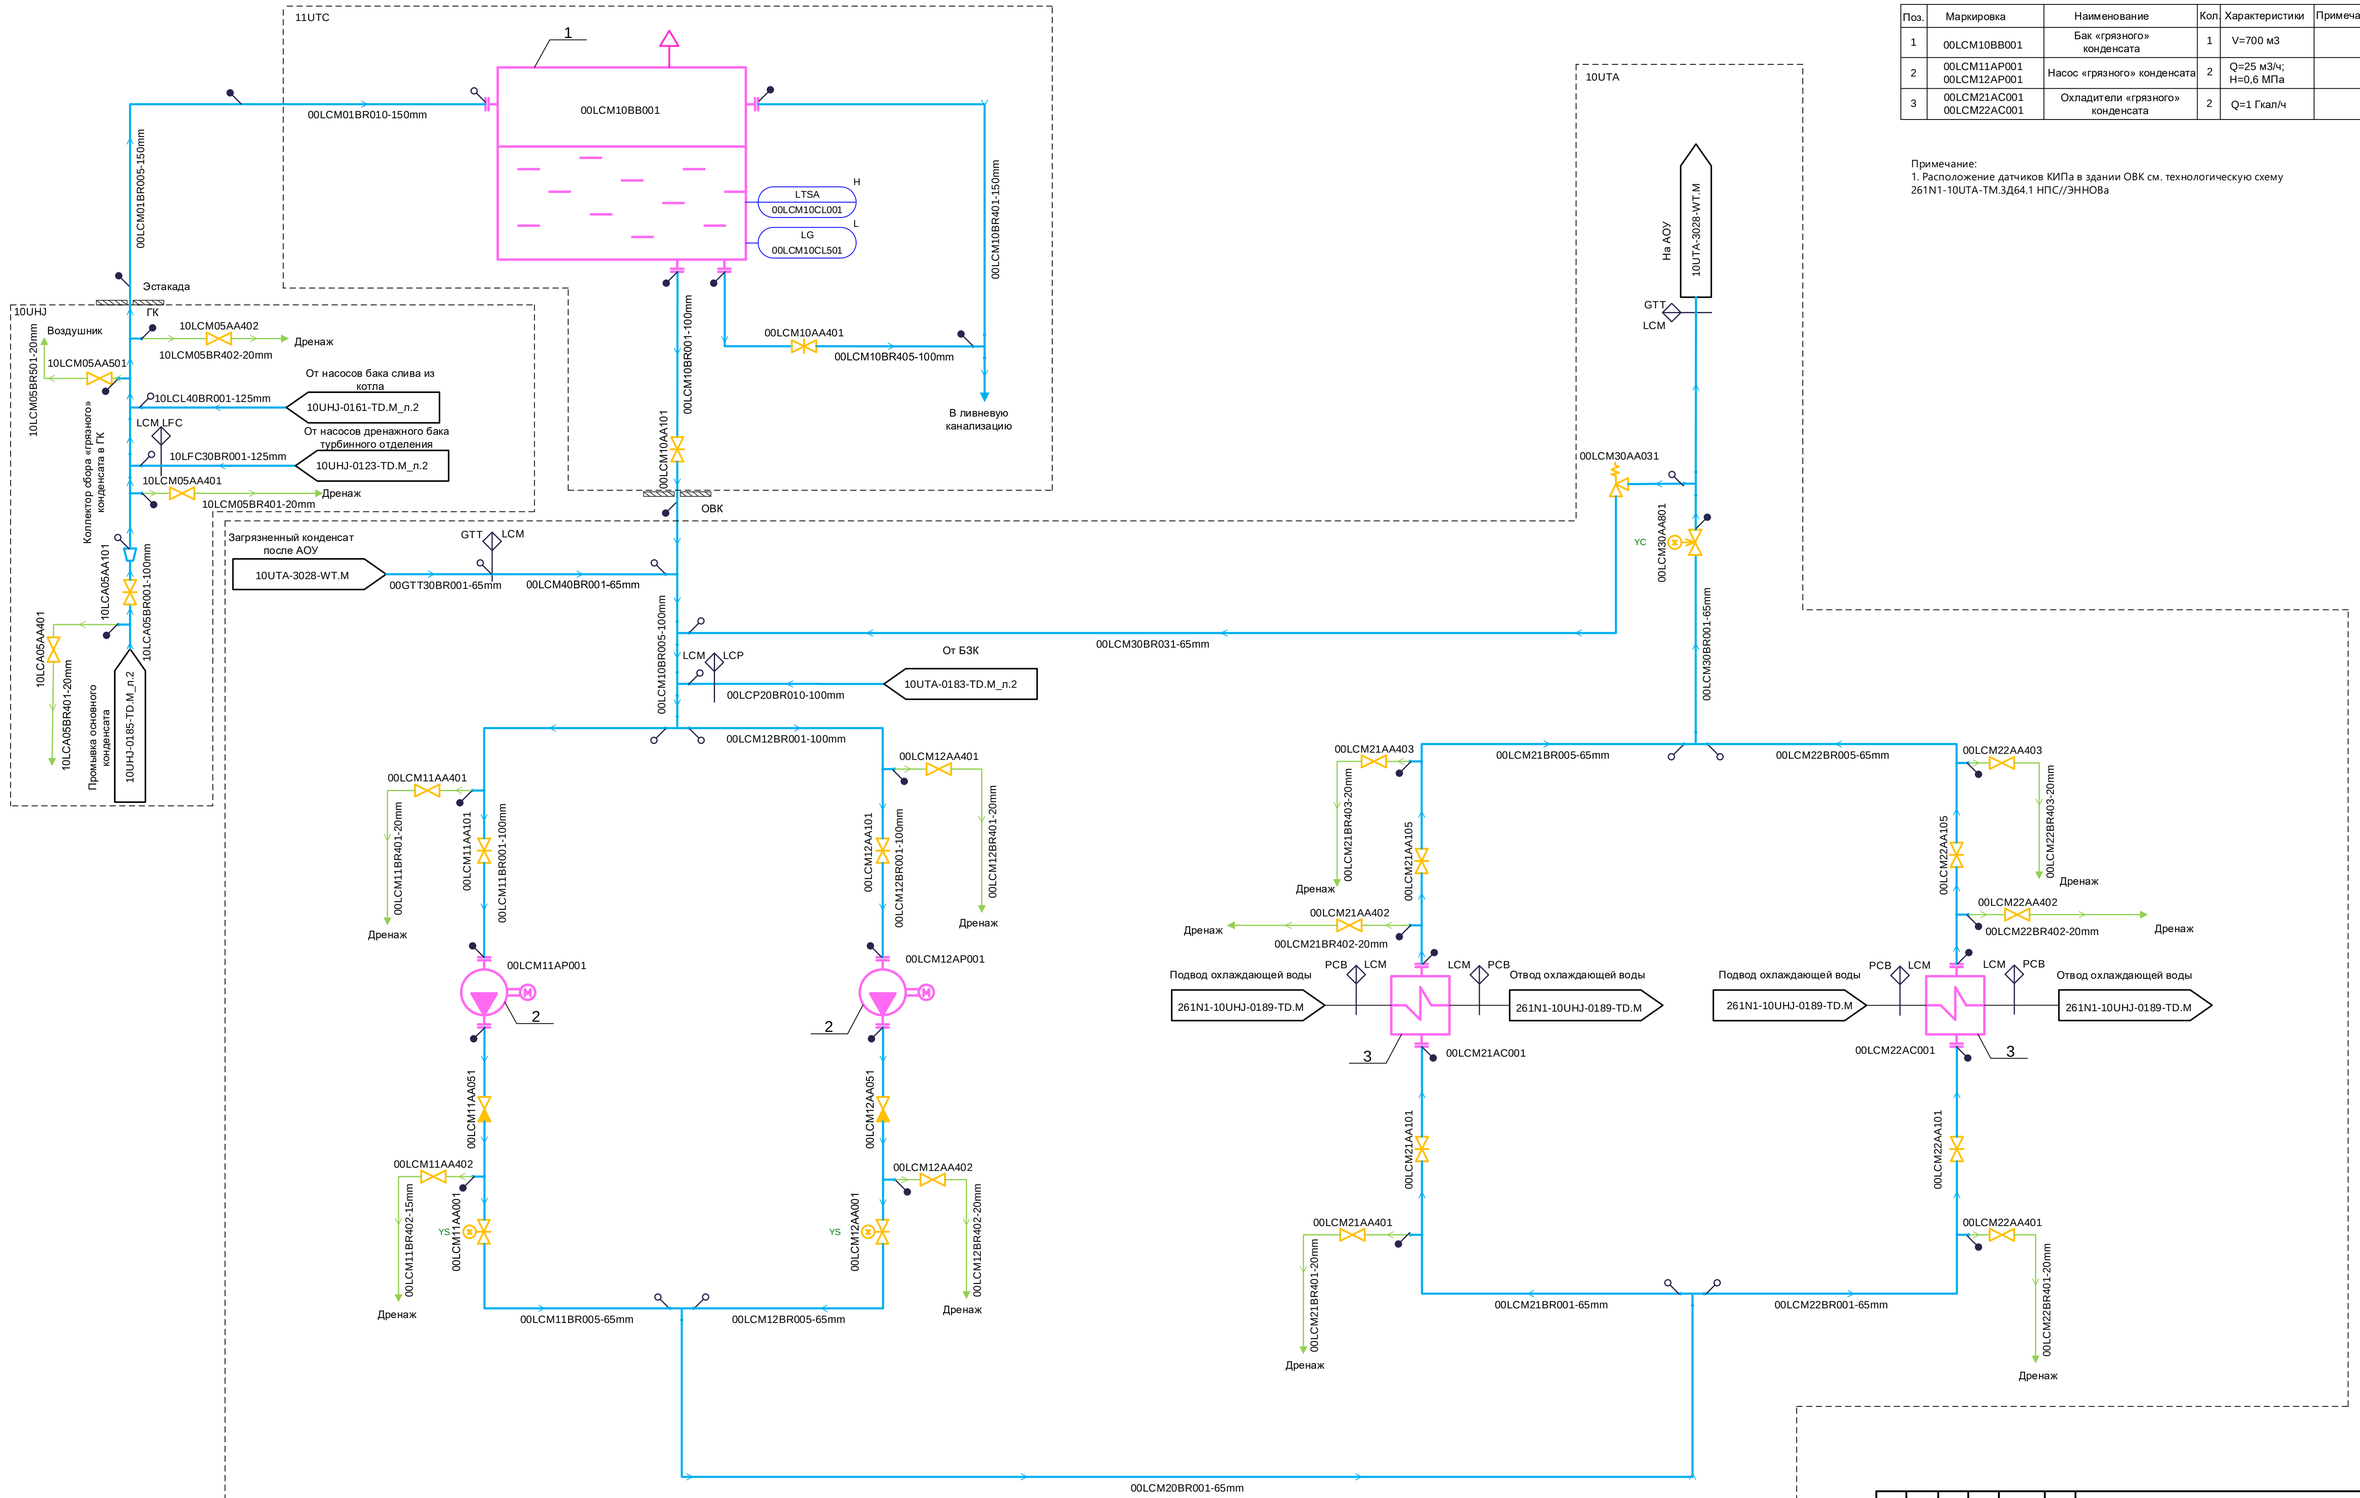

Перечень оборудования

Поз.	Маркировка	Наименование	Кол.	Характеристики	Примечание
1	00LCM10BB001	Бак «грязного» конденсата	1	V=700 м3	
2	00LCM11AP001 00LCM12AP001	Насос «грязного» конденсата	2	Q=25 м3/ч; H=0,6 МПа	
3	00LCM21AC001 00LCM22AC001	Охладители «грязного» конденсата	2	Q=1 Гкал/ч	

Примечание:
1. Расположение датчиков КИПа в здании ОВК см. технологическую схему 261N1-10UTA-ТМ.ЗД64.1 НПС//ЭННОВа

1		Зам	154-26		01.26	
Изм.	Кол.уч	Лист	№ док.	Подп.	Дата	
Разработал		Евстифеев				
Проверил		Лаврякова				
Гл. спец		Сергеева				
Н. контр.		Астраханцев				

261N1-10UTA-0169-TD.M

Южно-Якутская ТЭС. Рабочая документация

Объединенно-вспомогательный корпус. PI-диаграмма трубопроводов грязного конденсата

Стадия	Лист	Листов
Р	2	

PI-диаграмма трубопроводов грязного конденсата. Система LCM

АКЦИОНЕРНОЕ ОБЩЕСТВО ИНСТИТУТ ТЕПЛОЭЛЕКТРОПРОЕКТ г. МОСКВА

Согласовано

ОАСУ

Взам. инв. №

Подпись и дата

Инв. № подл.

Формат А1