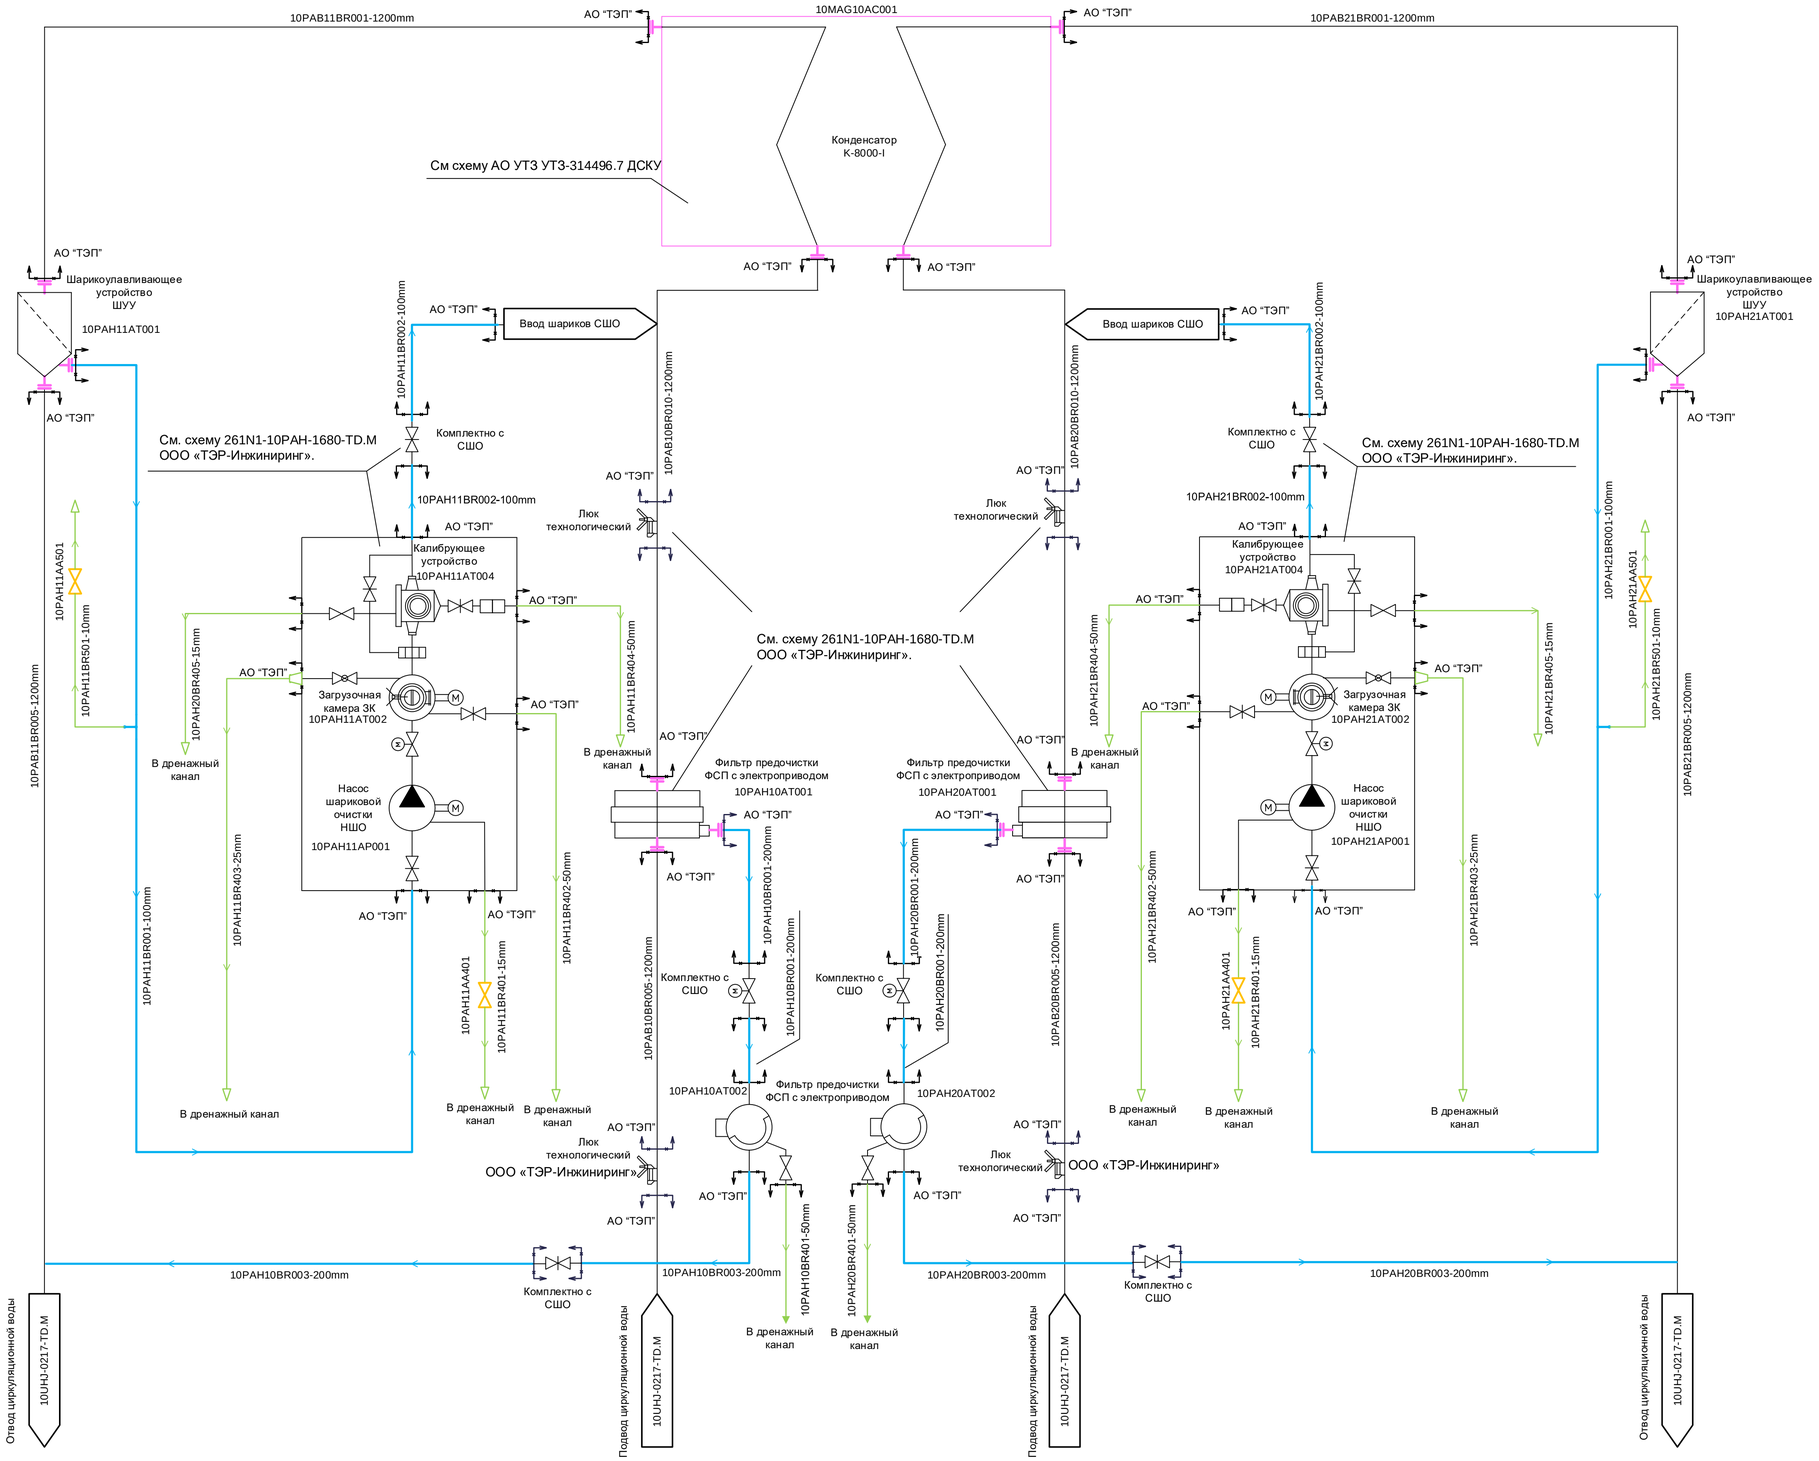

Примечание:
1. Оборудование КИПиА поставляется комплектно с СШО, см. документацию ООО «ТЭР-Инжиниринг» 261N1-10PAH-1680-TD.M.
2. См. схему 261N1-10PAH-1680-TD.M ООО «ТЭР-Инжиниринг».
3. См. схему АО УТЗ УТЗ-314496.7 ДСКУ

						261N1-10UHJ-0175-TD.M		
1			1785-25		05.25	Южно-Якутская ТЭС. Рабочая документация		
Изм.	Кол.уч	Лист	№ док.	Подп.	Дата			
Разработал		Харитонов				Главный корпус. P&I-диаграмма трубопроводов шариковой очистки конденсатора турбины	Стадия	Лист	Листов
Проверил		Лаврякова					Р	2	
Глав.спец.		Супонина							
Н. контр.		Черемушкина				P&I-диаграмма трубопроводов шариковой очистки конденсатора турбины. Система РАН	АКЦИОНЕРНОЕ ОБЩЕСТВО ИНСТИТУТ ТЕПЛОЭЛЕКТРОПРОЕКТ г. МОСКВА		

Согласовано
ОАСУ
Взам. инв. №
Подпись и дата
Инв. № подл.

Формат А1