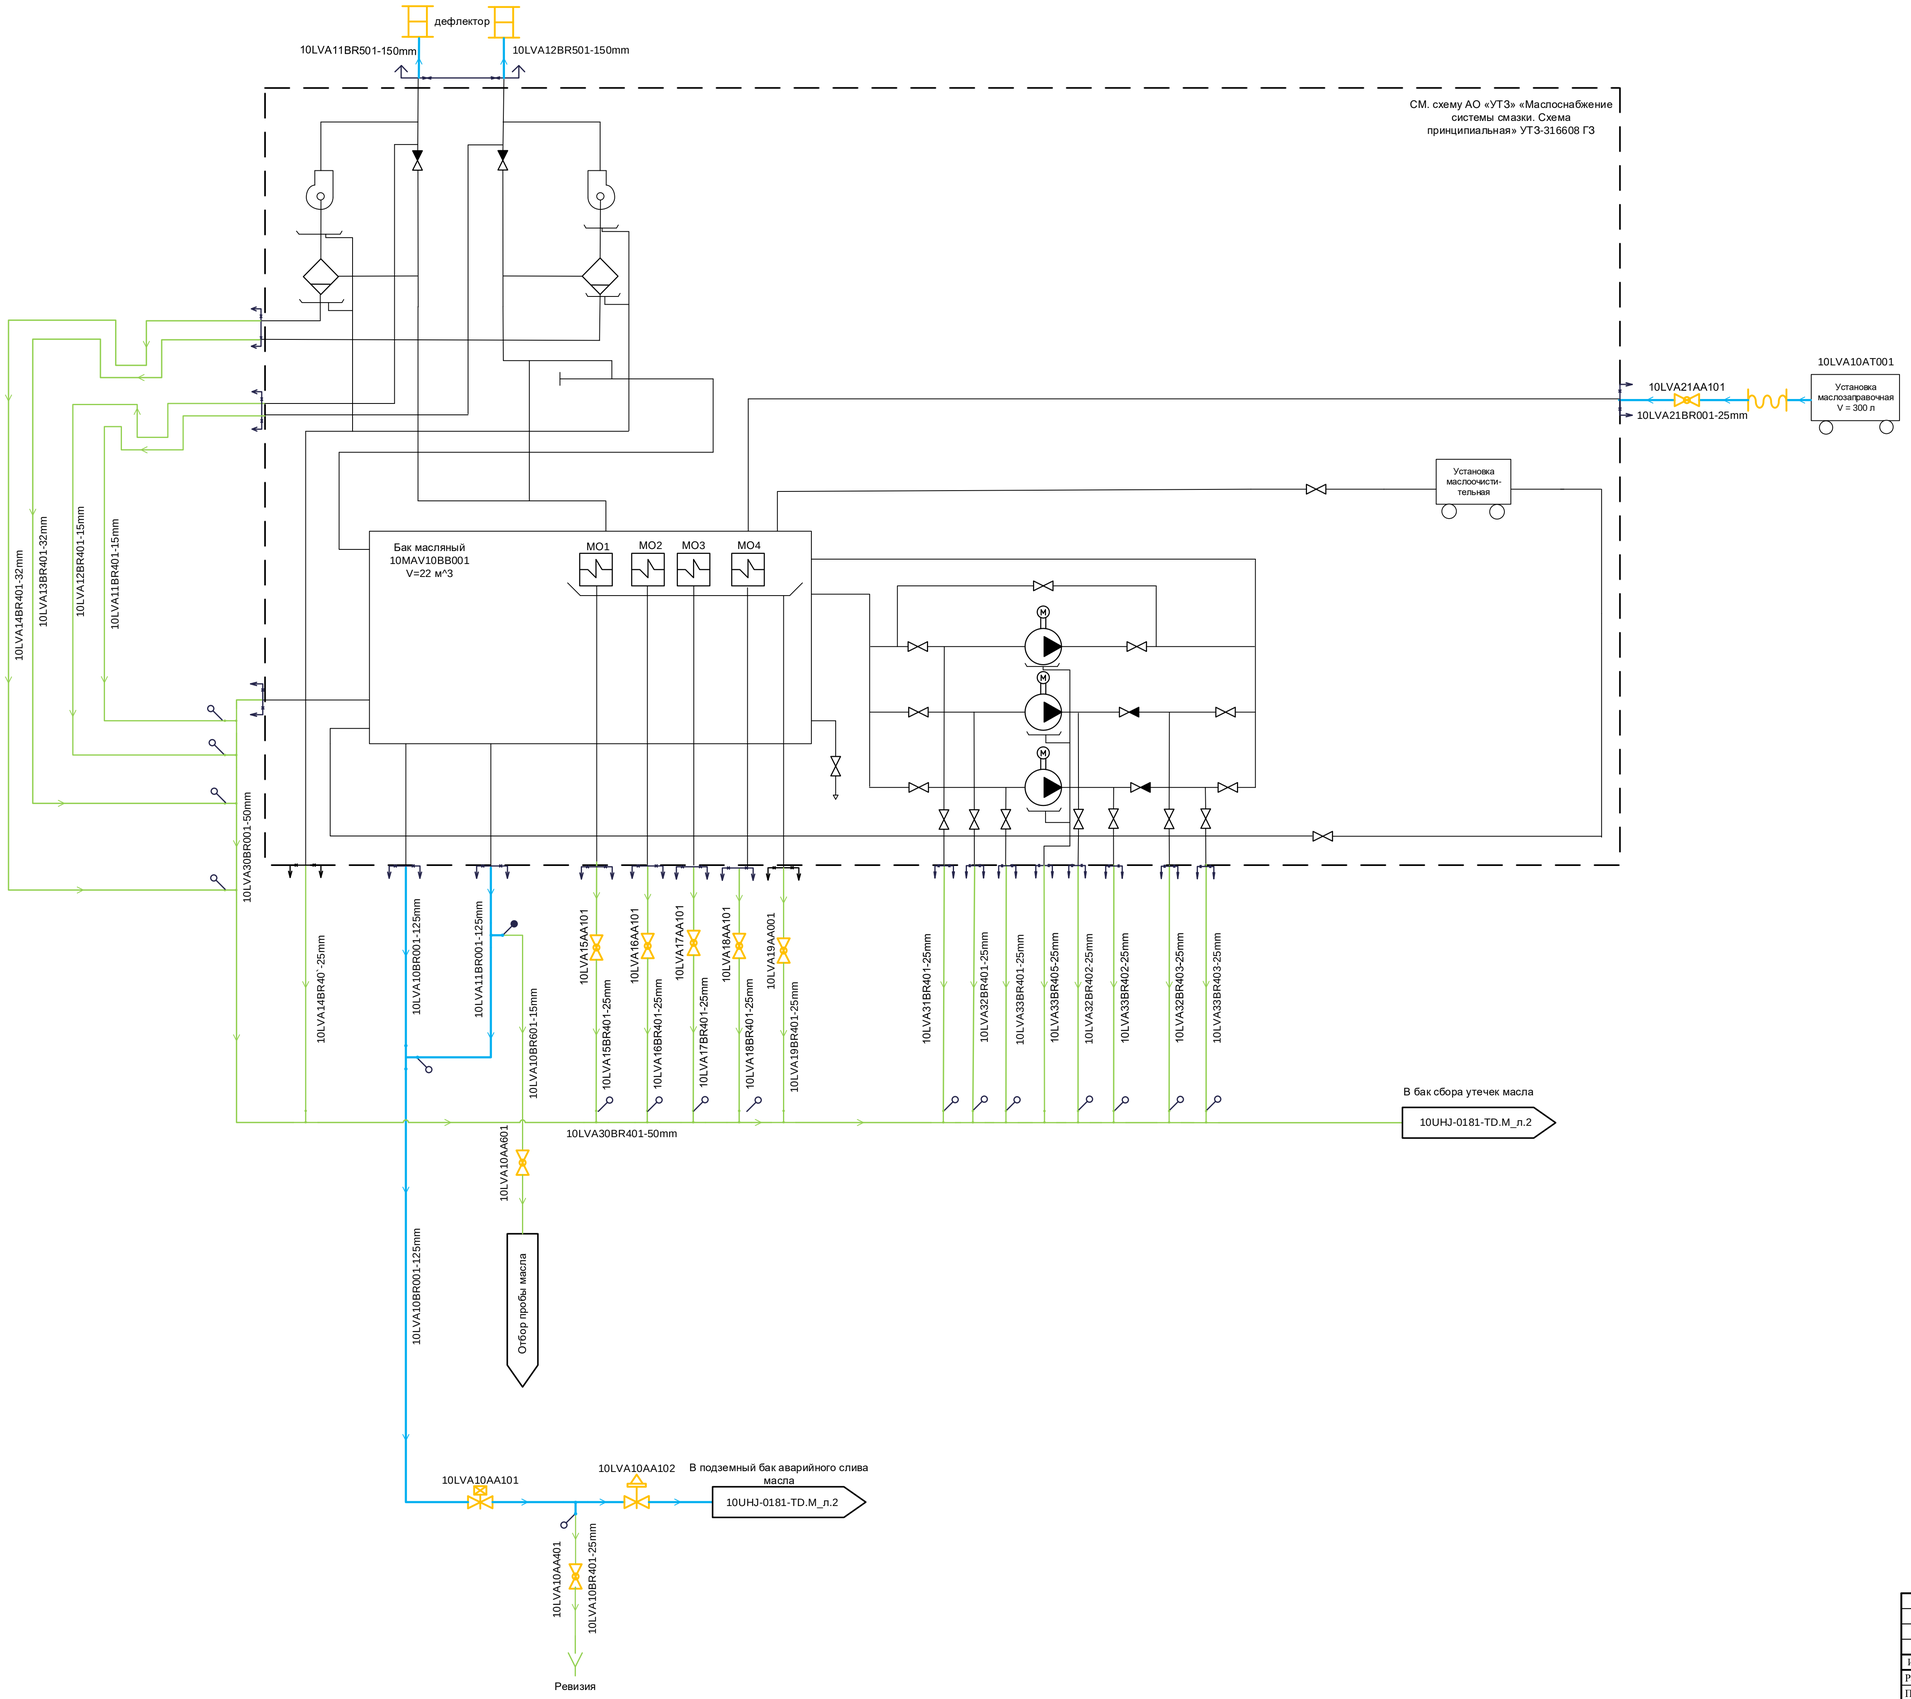

Примечание:
1. Трубопроводы аварийного слива и сбора утечек масла заглушить до ввода 2-го этапа.
2. Задвижка 10LVA10AA102 оснащена колонковым приводом.
3. Задвижка 10LVA10AA101 оснащена замковым устройством.

1			1538-25		04.25	261N1-10UHJ-0179-TD.M
Изм.	Кол.уч	Лист	№ док.	Подп.	Дата	Южно-Якутская ТЭС. Рабочая документация
Разработал		Харитонов				Главный корпус. PI-Диаграмма трубопроводов маслосистемы ПТ
Проверил		Лаврякова				Стадия: Р; Лист: 2; Листов:
Глав.спец.		Супонина				
Н. контр.		Черемушкина				PI-диаграмма трубопроводов маслосистемы ПТ. Система LVA

АКЦИОНЕРНОЕ ОБЩЕСТВО ИНСТИТУТ ТЕПЛОЭЛЕКТРОПРОЕКТ г. МОСКВА

Согласовано

Взам. инв. №

Подпись и дата

Инв. № подл.

Формат А1