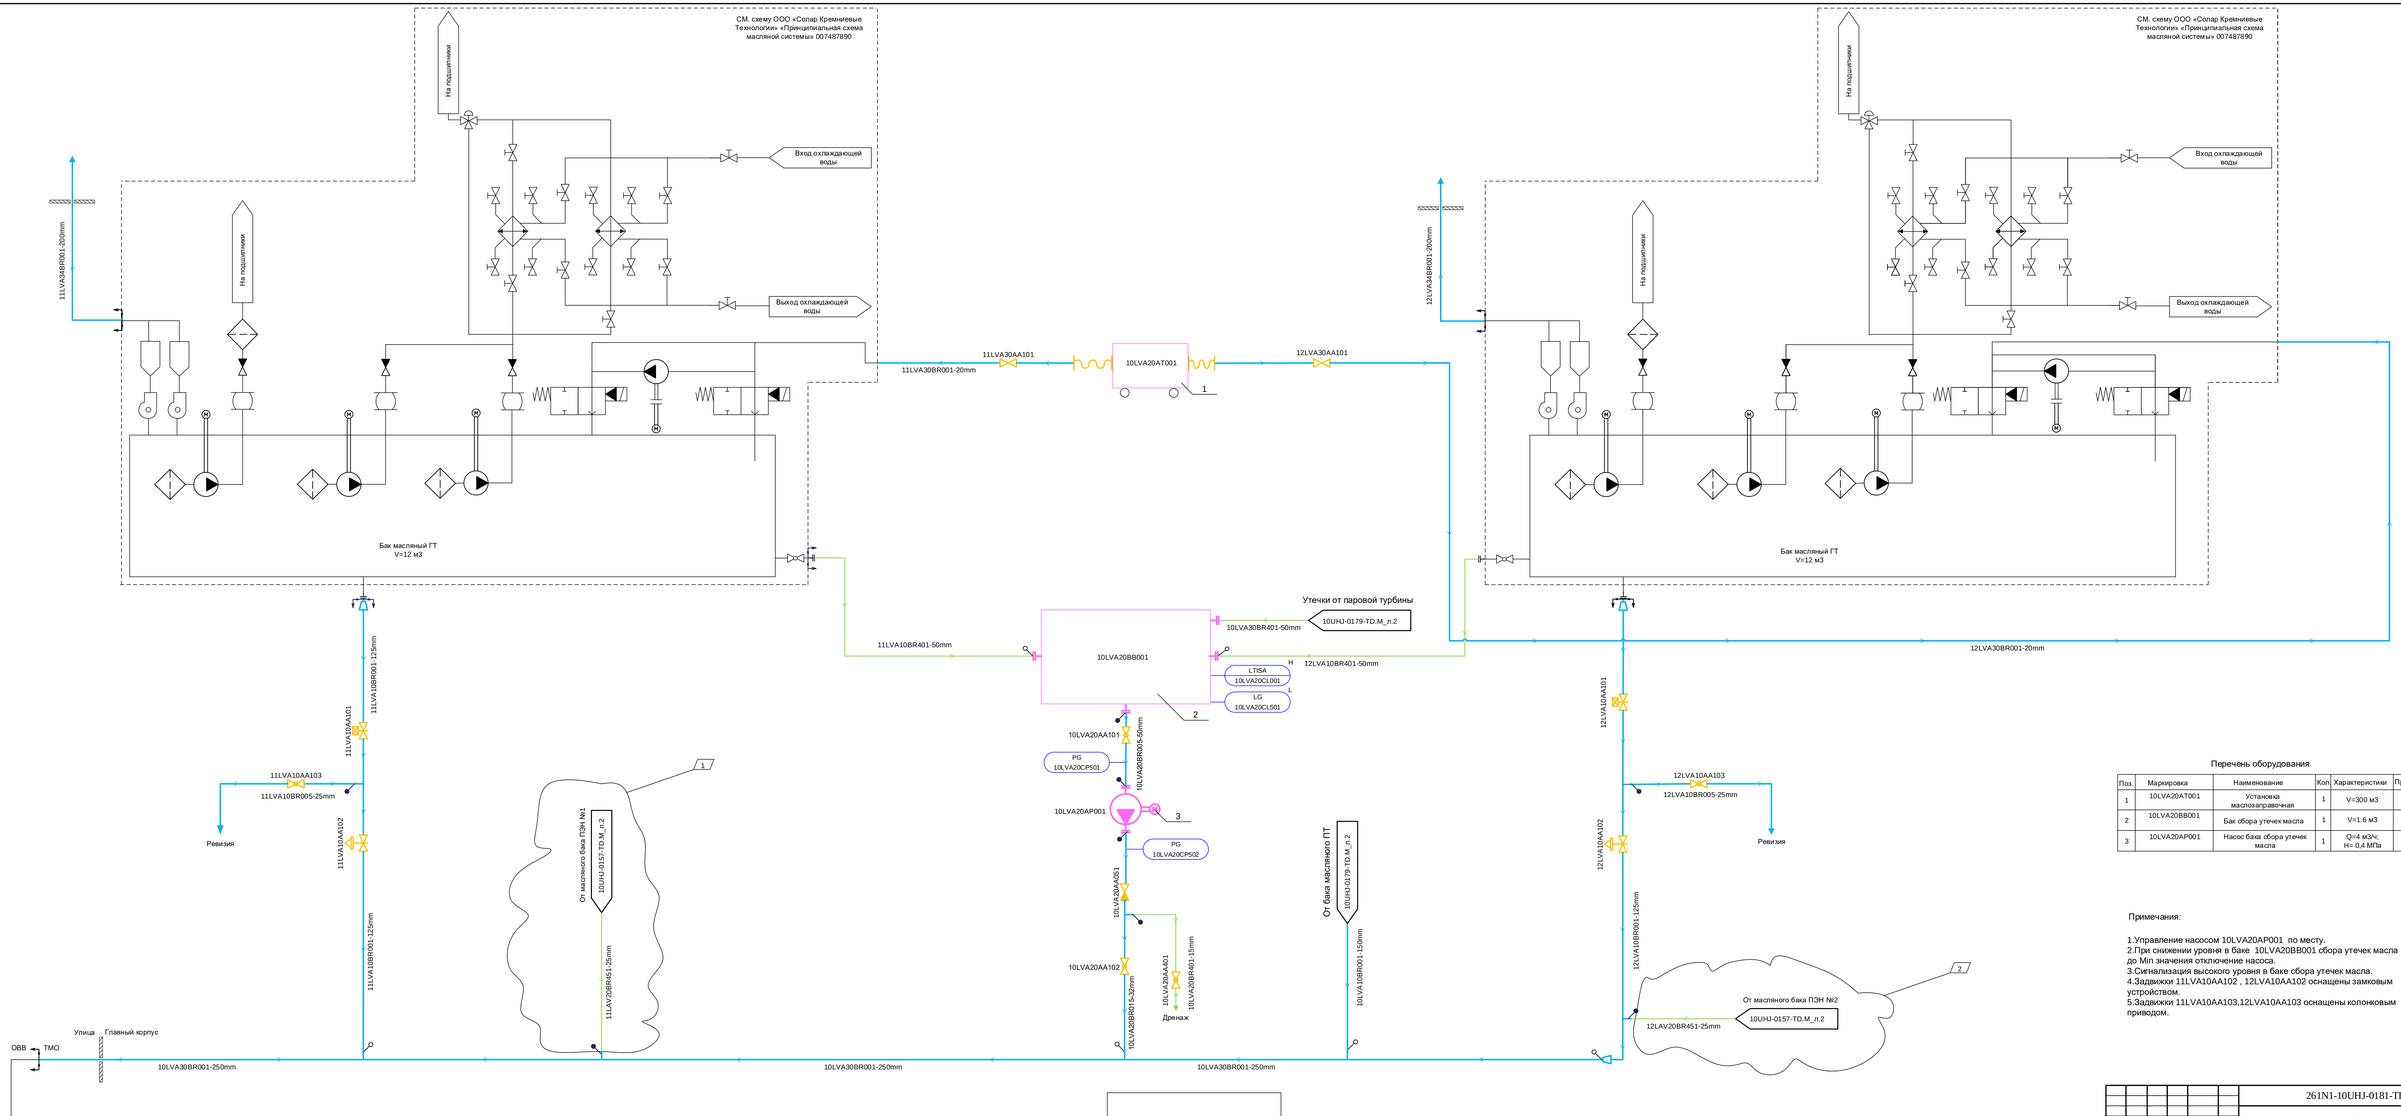

Перечень оборудования

Поз.	Маркировка	Наименование	Кол.	Характеристики	Примечание
1	10LVA20AT001	Установка маслозаправочная	1	V=300 м3	
2	10LVA20BB001	Бак сбора утечек масла	1	V=1,6 м3	
3	10LVA20AP001	Насос бака сбора утечек масла	1	Q=4 м3/ч; H= 0,4 МПа	

Примечания:

1.Управление насосом 10LVA20AP001 по месту.
2.При снижении уровня в баке 10LVA20BB001 сбора утечек масла до Min значения отключение насоса.
3.Сигнализация высокого уровня в баке сбора утечек масла.
4.Задвижки 11LVA10AA102 , 12LVA10AA102 оснащены замковым устройством.
5.Задвижки 11LVA10AA103,12LVA10AA103 оснащены колонковым приводом.

1	2	Зам	154-26			01.26	261N1-10UHJ-0181-TD.M
Изм.	Кол.уч.	Лист	№ док.	Подп.	Дата		Южно-Якутская ТЭС. Рабочая документация
Разработал		Евстифеев					Главный корпус. P&I-диаграмма трубопроводов маслоснабжения ГТУ
Проверил		Лаврикова					
Гл. спец.		Сергеева					
Н. контр.		Черемушкина					P&I-диаграмма трубопроводов маслоснабжения ГТУ. Система LVA.

Стадия	Лист	Листов
Р	2	

АКЦИОНЕРНОЕ ОБЩЕСТВО «ТЕХЭНЕРГОПРОМ» МОСКВА

Согласовано

Взам. инв. №

Подпись и дата

Инв. № подл.

Формат А2х3