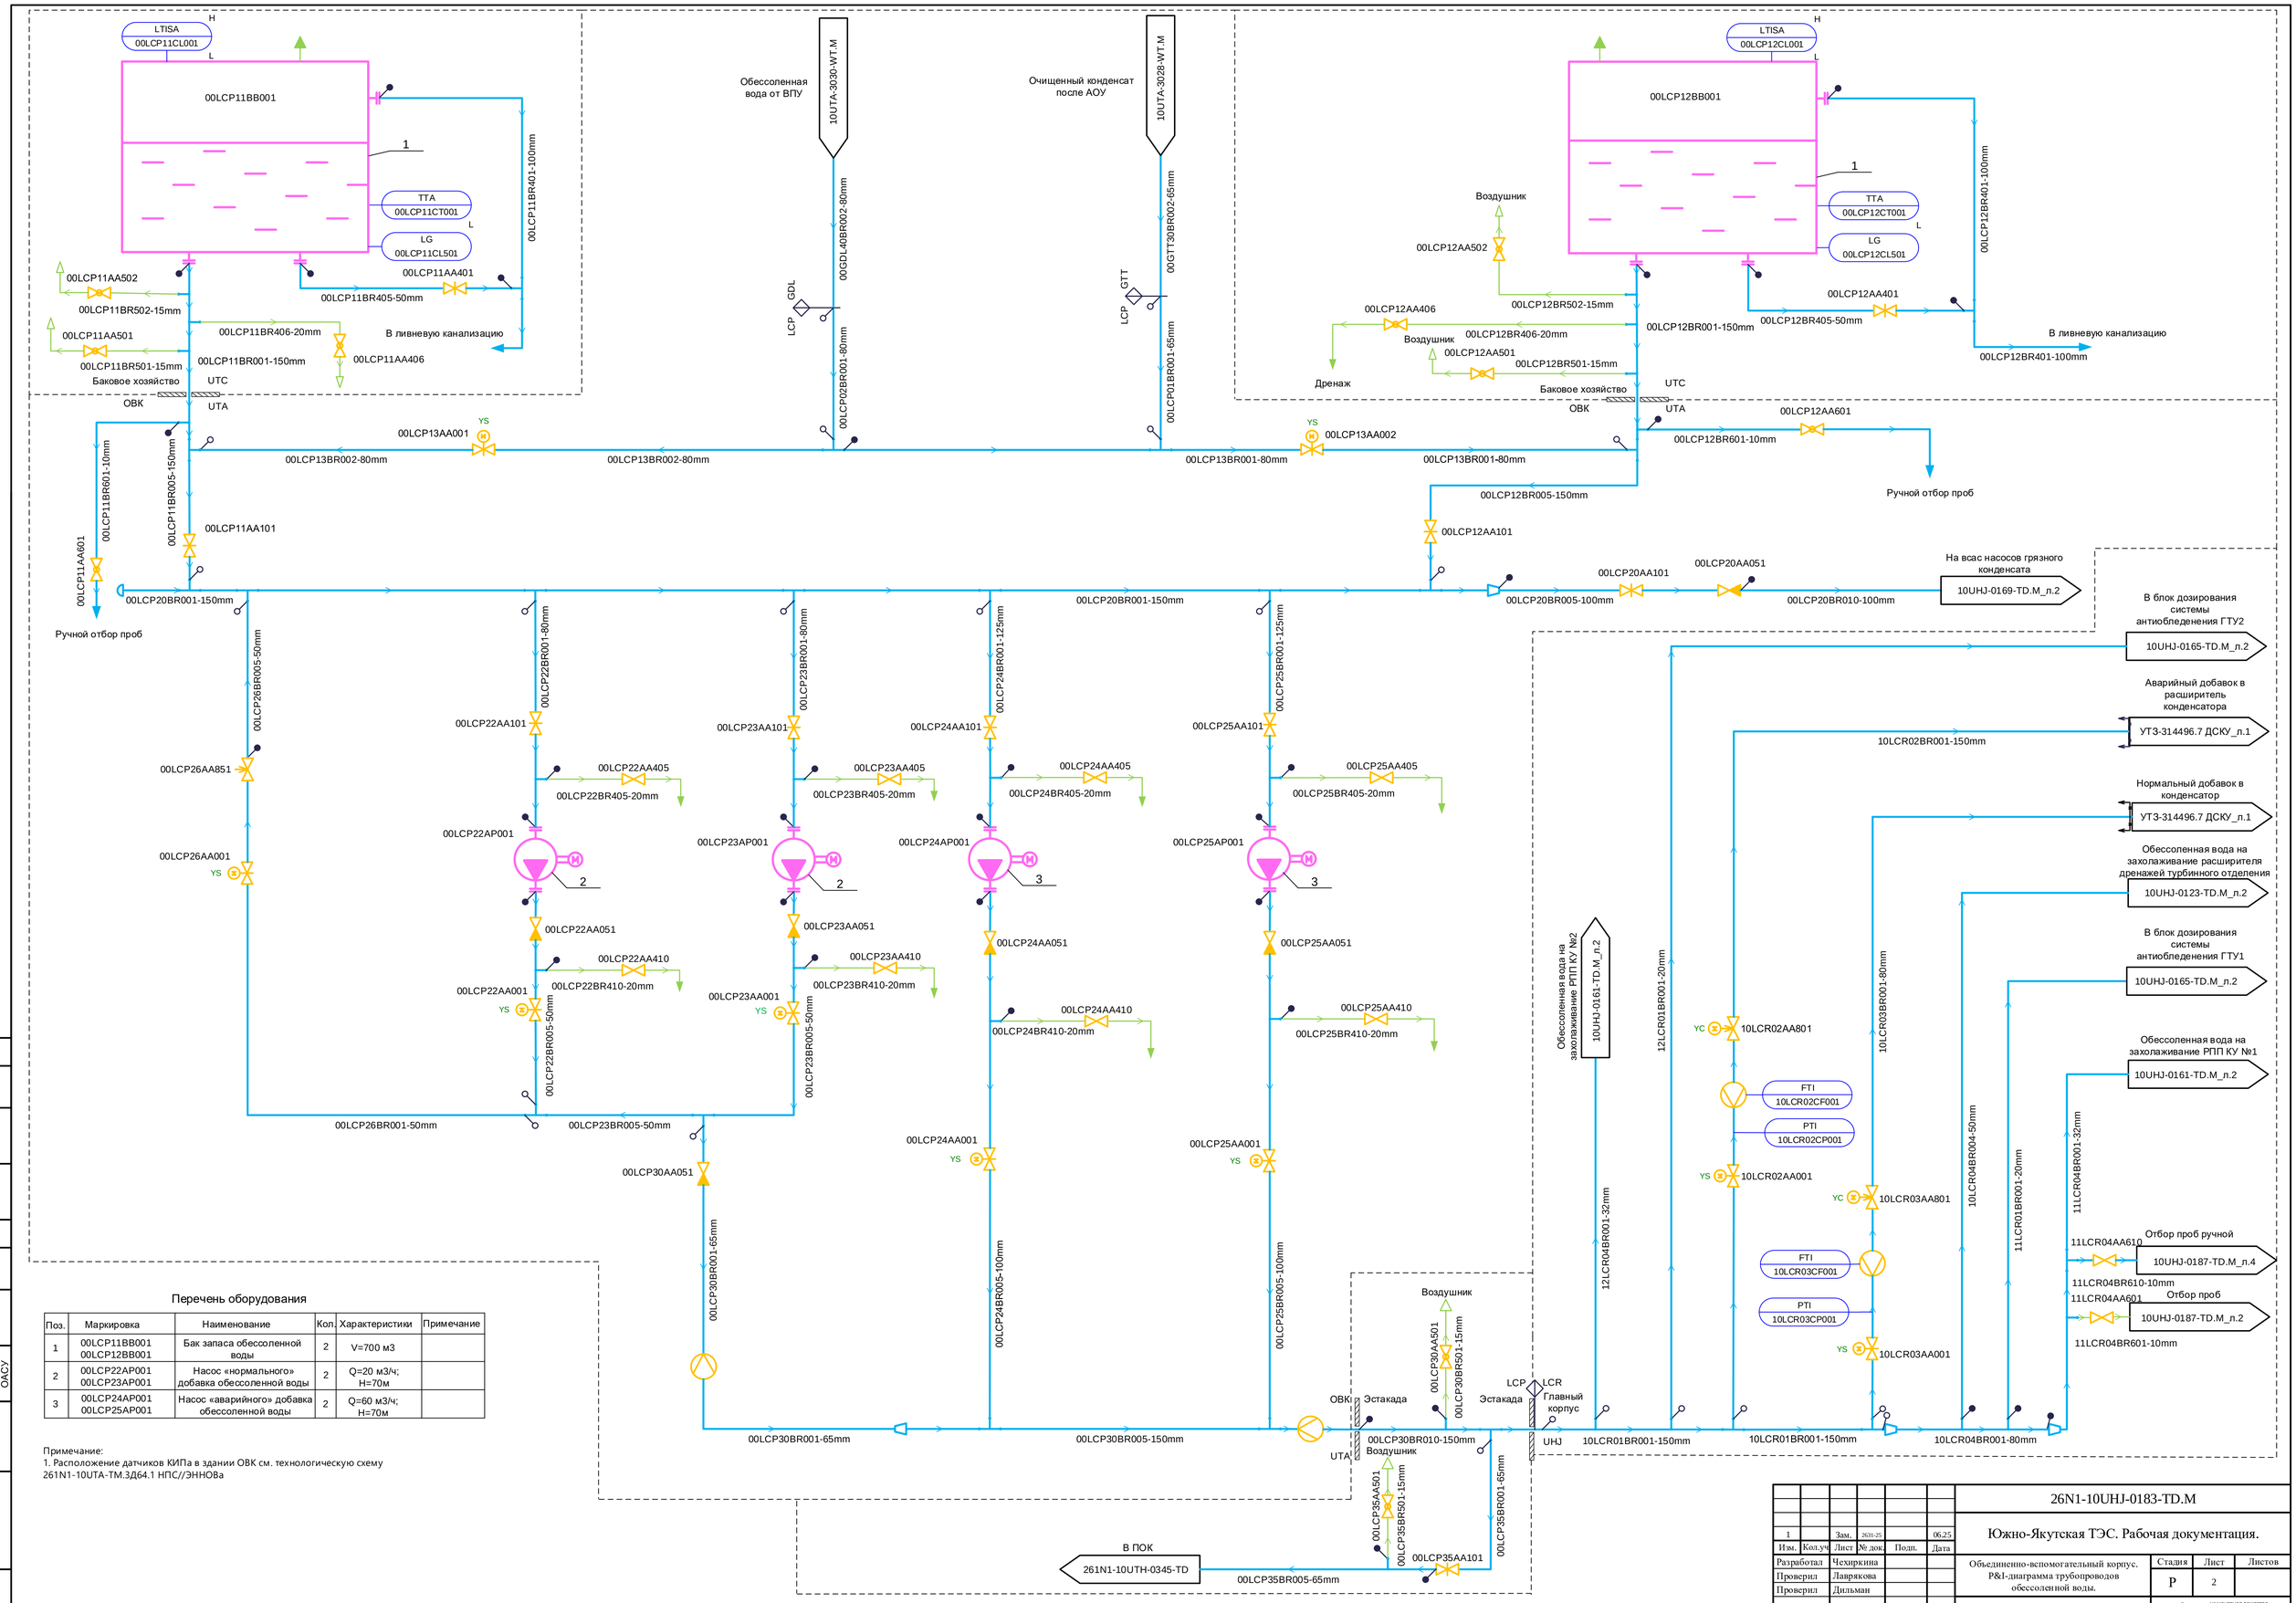

Перечень оборудования

Поз.	Маркировка	Наименование	Кол.	Характеристики	Примечание
1	00LCP11BB001 00LCP12BB001	Бак запаса обессоленной воды	2	V=700 м3	
2	00LCP22AP001 00LCP23AP001	Насос «нормального» добавка обессоленной воды	2	Q=20 м3/ч; H=70м	
3	00LCP24AP001 00LCP25AP001	Насос «аварийного» добавка обессоленной воды	2	Q=60 м3/ч; H=70м	

Примечание:
1. Расположение датчиков КИПа в здании ОВК см. технологическую схему 261N1-10UTA-ТМ.3Д64.1 НПС//ЭННОВа

1		Зам.	263I-25		06.25	26N1-10UHJ-0183-TD.M
Изм.	Кол.уч	Лист	№ док.	Подп.	Дата	Южно-Якутская ТЭС. Рабочая документация.
Разработал		Чехиркина				Объединенно-вспомогательный корпус. P&I-диаграмма трубопроводов обессоленной воды.
Проверил		Лаврякова				Стадия: Р; Лист: 2; Листов:
Проверил		Дильман				
Н. контр.		Черемушкина				P&I-диаграмма трубопроводов обессоленной воды. Система LCP, LCR.

АКЦИОНЕРНОЕ ОБЩЕСТВО ИНСТИТУТ ТЕПЛОЭЛЕКТРОПРОЕКТ Г. МОСКВА

Согласовано
ОАСУ
Взам. инв. №
Подпись и дата
Инв. № подл.

Формат А1