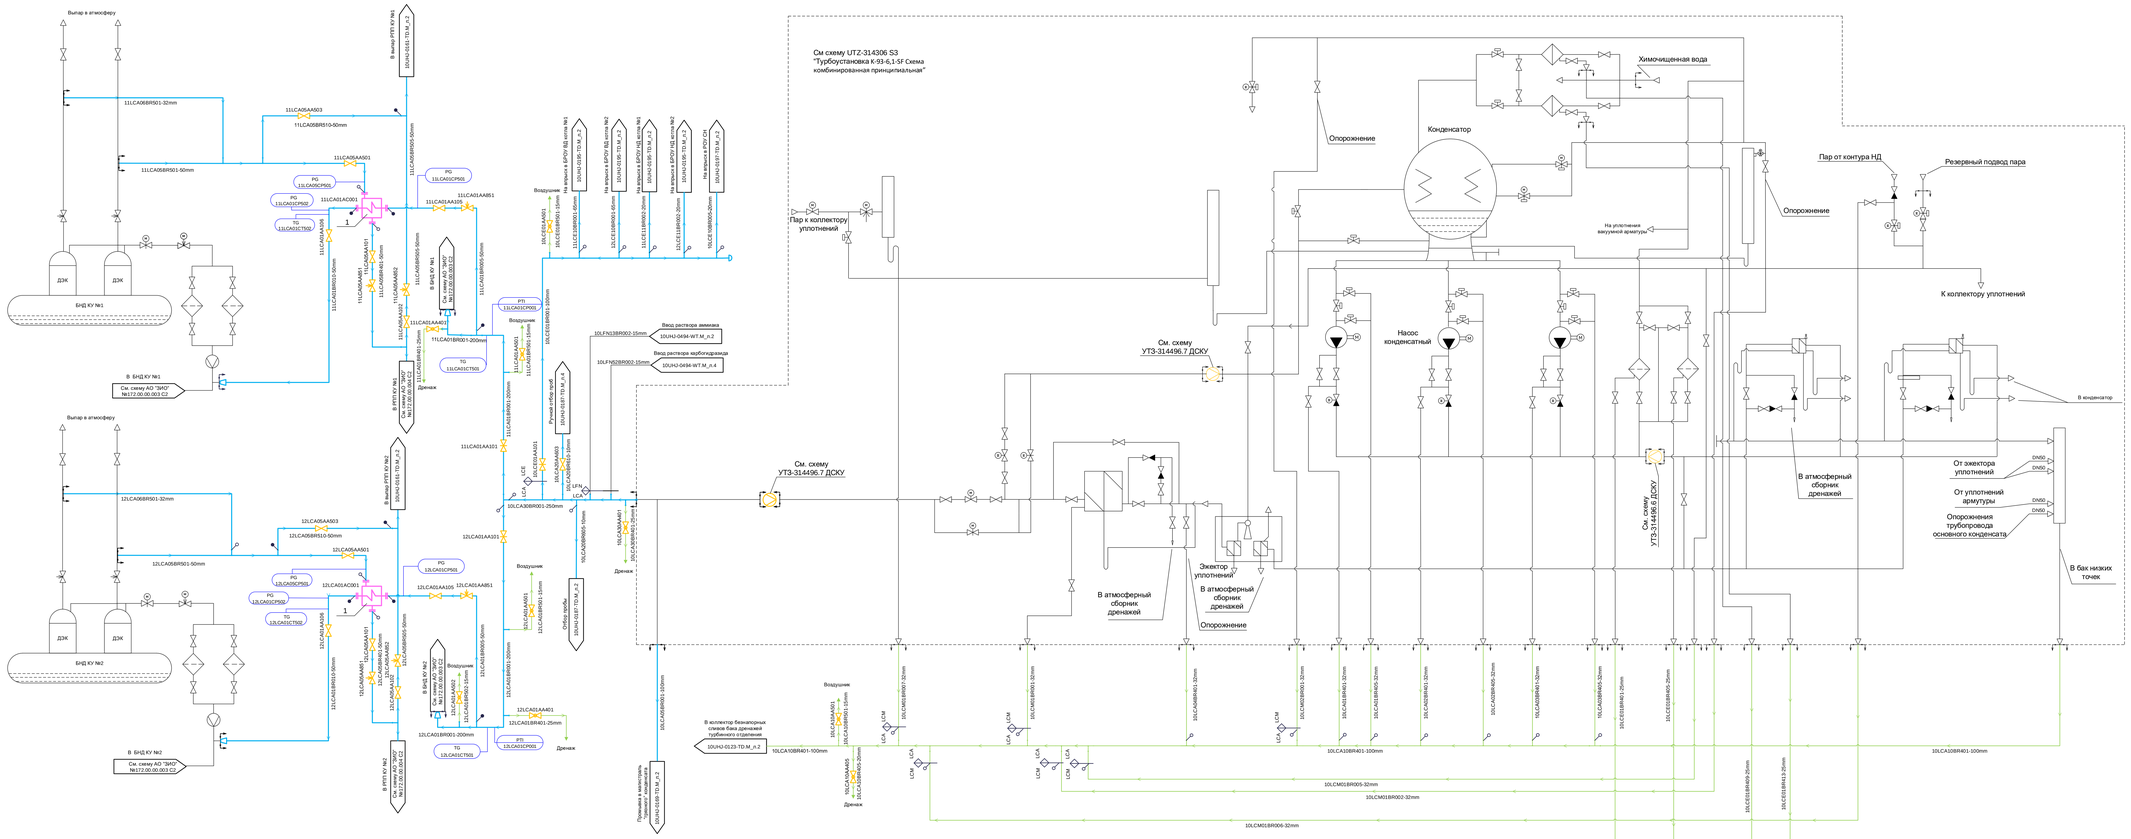

Перечень оборудования

Поз.	KKS	Наименование	Кол	Хар-ки	Примечание
1	11LCA01AC001 12LCA01AC001	Охладитель выпара дваерашенных колонок БНД КУ	2	Q = 0.416 Гкал/час	-

									26N1-10UHJ-018S-TD.M
Изм.	Кол.уч.	Лист	N док.	Подп.	Дата				Южно-Якутская ТЭС. Рабочая документация.
Разработал	Пастухова					01.25			
Проверил	Баранова								
Гл. спец.	Сергеев						Стадия	Лист	Листов
Н. контр.	Черносвитов						Р	2	
							Ф-диаграмма трубопроводов основного конденсата.		

Формат А1х2